

PLAN A — THE SPRINGBROOK

2 BR / 2 BA, 1 story, 2-car front-loaded garage recessed 5'-0", covered front porch, rear patio

AREA TABULATION — computed by tools/floorplans.py from the wall-face polygons

Conditioned (heated) area	1,406 SF	outside face of ext. walls
2-car garage	458 SF	outside face / centreline
Covered front porch	102 SF	slab
TOTAL UNDER ROOF	1,966 SF	cond. + garage + porch
Rear patio (uncovered, not under roof)	72 SF	slab

Program target 1,444 conditioned (FACTS §4 nominal 38'-0" × 38'-0"); Lilburn Table 4.1 R-2 cottage min heated 1,000 SF.

ROOM SCHEDULE (clear, inside face)

2-CAR GARAGE	20'-4" × 21'-2"	430 SF
HALL	3'-6" × 26'-4"	92 SF
BEDROOM 2	12'-2" × 10'-10"	148 SF
CLOSET	5'-6" × 2'-2"	12 SF
BATH 2	12'-2" × 7'-10"	95 SF
COAT	2'-8" × 4'-4"	12 SF
PANTRY	9'-2" × 4'-4"	40 SF
LAUNDRY / MUD	6'-8" × 10'-4"	69 SF
KITCHEN / DINING	16'-4" × 10'-6"	172 SF
W.I.C.	13'-4" × 5'-4"	71 SF
PRIMARY BATH	13'-4" × 8'-2"	109 SF
PRIMARY BEDROOM	13'-4" × 10'-2"	136 SF
SUITE HALL	4'-0" × 7'-2"	29 SF
GREAT ROOM	19'-4" × 13'-10"	289 SF

ROOF / HEIGHT

main gable (rear block): span 25'-0", 8:12 → ridge 17'-10" above FF (plate 9'-0" + heel + rise)

front-wing gable (extended over the porch): span 17'-0", 8:12 → ridge 15'-2" above FF (plate 9'-0" + heel + rise)

garage gable: span 21'-0", 6:12 → ridge 14'-9" above FF (plate 9'-0" + heel + rise)

Max ridge 17'-10" ≤ 24 ft program cap; Ord. 2023-603 Table 4.1 R-2 max height 40 ft — appears consistent.

ACCESSIBILITY CHECKLIST (voluntary)


- Zero-step entries — front porch (slab flush with finished floor) and garage-to-mud-room door, patio door ≤ 1/2-in threshold [design intent]
- Door clear width — all passage doors 36 in (3'-0"); closets 30 in; french door 6'-0" [design intent]
- Hall width — main hall 3'-0" clear (42 in); suite hall 4'-0" clear [design intent]
- Turning circles — 5'-0" (60 in) circle drawn and checked clear in both baths [checked by script]
- Curbless shower — primary bath 5'-0" × 3'-10" curbless (recessed slab per 03 30 00 §2.05) [design intent]
- Grab-bar blocking — 2×10 solid blocking 33–36 in AFF at all toilets, tub and showers (2024 IRC (GA 2026) — voluntary; ANSI A117.1 Type C-type) [design intent — VERIFY blocking heights with architect]
- Plate height / vaulted — 9'-0" plate, great room vaulted [design intent]
- Single-level living — 1 story, no interior steps; laundry on the living level [design intent]
- Lever hardware, rocker switches, 48-in max reach — to be specified (Division 08 / 26) [later stage]
- Lilburn §734 visitability — applies to attached dwellings only; voluntarily exceeded (100% zero-step) [appears consistent with Ord. 2023-603 §734 (not applicable)]

LEGEND

- Exterior wall — 2×6 @ 6 in (poché)
- Interior partition — 2×4 @ 4 in
- Cased opening / ceiling beam (no wall)
- Window (triple line), width noted
- Door leaf + swing, width noted (36 in typ.)
- 5'-0" turning circle (ANSI A117.1-type)
- Closet shelf + rod
- Covered porch slab
- Uncovered patio slab

NOTES

- Illustrative architectural plan for the rezoning application (Lilburn Zoning Ordinance 2023-603 §1003-4 renderings/elevations item). NOT FOR CONSTRUCTION. DRAFT — to be superseded by sealed drawings by a Georgia-registered architect.
- Dimensions are to the outside face of exterior walls (2×6, 6 in nominal) and to the centreline of interior partitions (2×4, 4 in). Plate height 9'-0"; great room vaulted; roof 8:12 main gables, 4:12 porch shed, architectural shingles.
- Accessibility (voluntary) — Ord. 2023-603 §734 applies to attached dwellings only); zero-step entries at the porch and garage/mud room; 36-in passage doors; 42-in halls; 5'-0" turning circles in both baths; curbless primary shower; 2×10 blocking for grab bars at all toilets, tub and showers.
- Garage door 16'-0" × 7'-0" recessed 5'-0" behind the front wall of the dwelling — appears consistent with Ord. 2023-603 Table 4.2 (front-loaded garages recessed ≥ 5 ft). Garage clear 20'-4" × 21'-2" ≥ 20 × 21 program minimum.
- Life safety: NFPA 13D residential sprinklers (mitigation for the single access road, IFC 2024 (GA) App. D107.1); smoke/CO alarms per 2024 IRC (GA 2026) R314/R315; bedroom egress windows per 2024 IRC (GA 2026) R310 — VERIFY net clear opening at unit selection.
- Program body is nominally 38'-0" × 38'-0" (1,444 SF). With the 2-car garage as a front wing (the only way to keep the 40-ft width cap), the conditioned envelope is an L: 17'-0" × 25'-10" front wing + 38'-0" × 25'-0" rear block = 1,406 SF conditioned (~2.6%); overall body 38'-0" × 51'-10" plus porch and patio.
- Rear patio drawn 12'-0" × 7'-0"; the program 12 × 9 slab would end 10 in inside the 20-ft rear buffer easement on a 100-ft lot (15 + 6 + 5 + 21'-10" + 25 + 8 = 80'-10"). VERIFY with Planning staff whether an at-grade uncovered slab is a buffer encroachment; otherwise hold the patio at 7 ft.
- Areas are computed by tools/floorplans.py from the wall face polygons (conditioned = outside face of exterior walls; total under roof = conditioned + garage + covered porch; the uncovered patio is excluded).

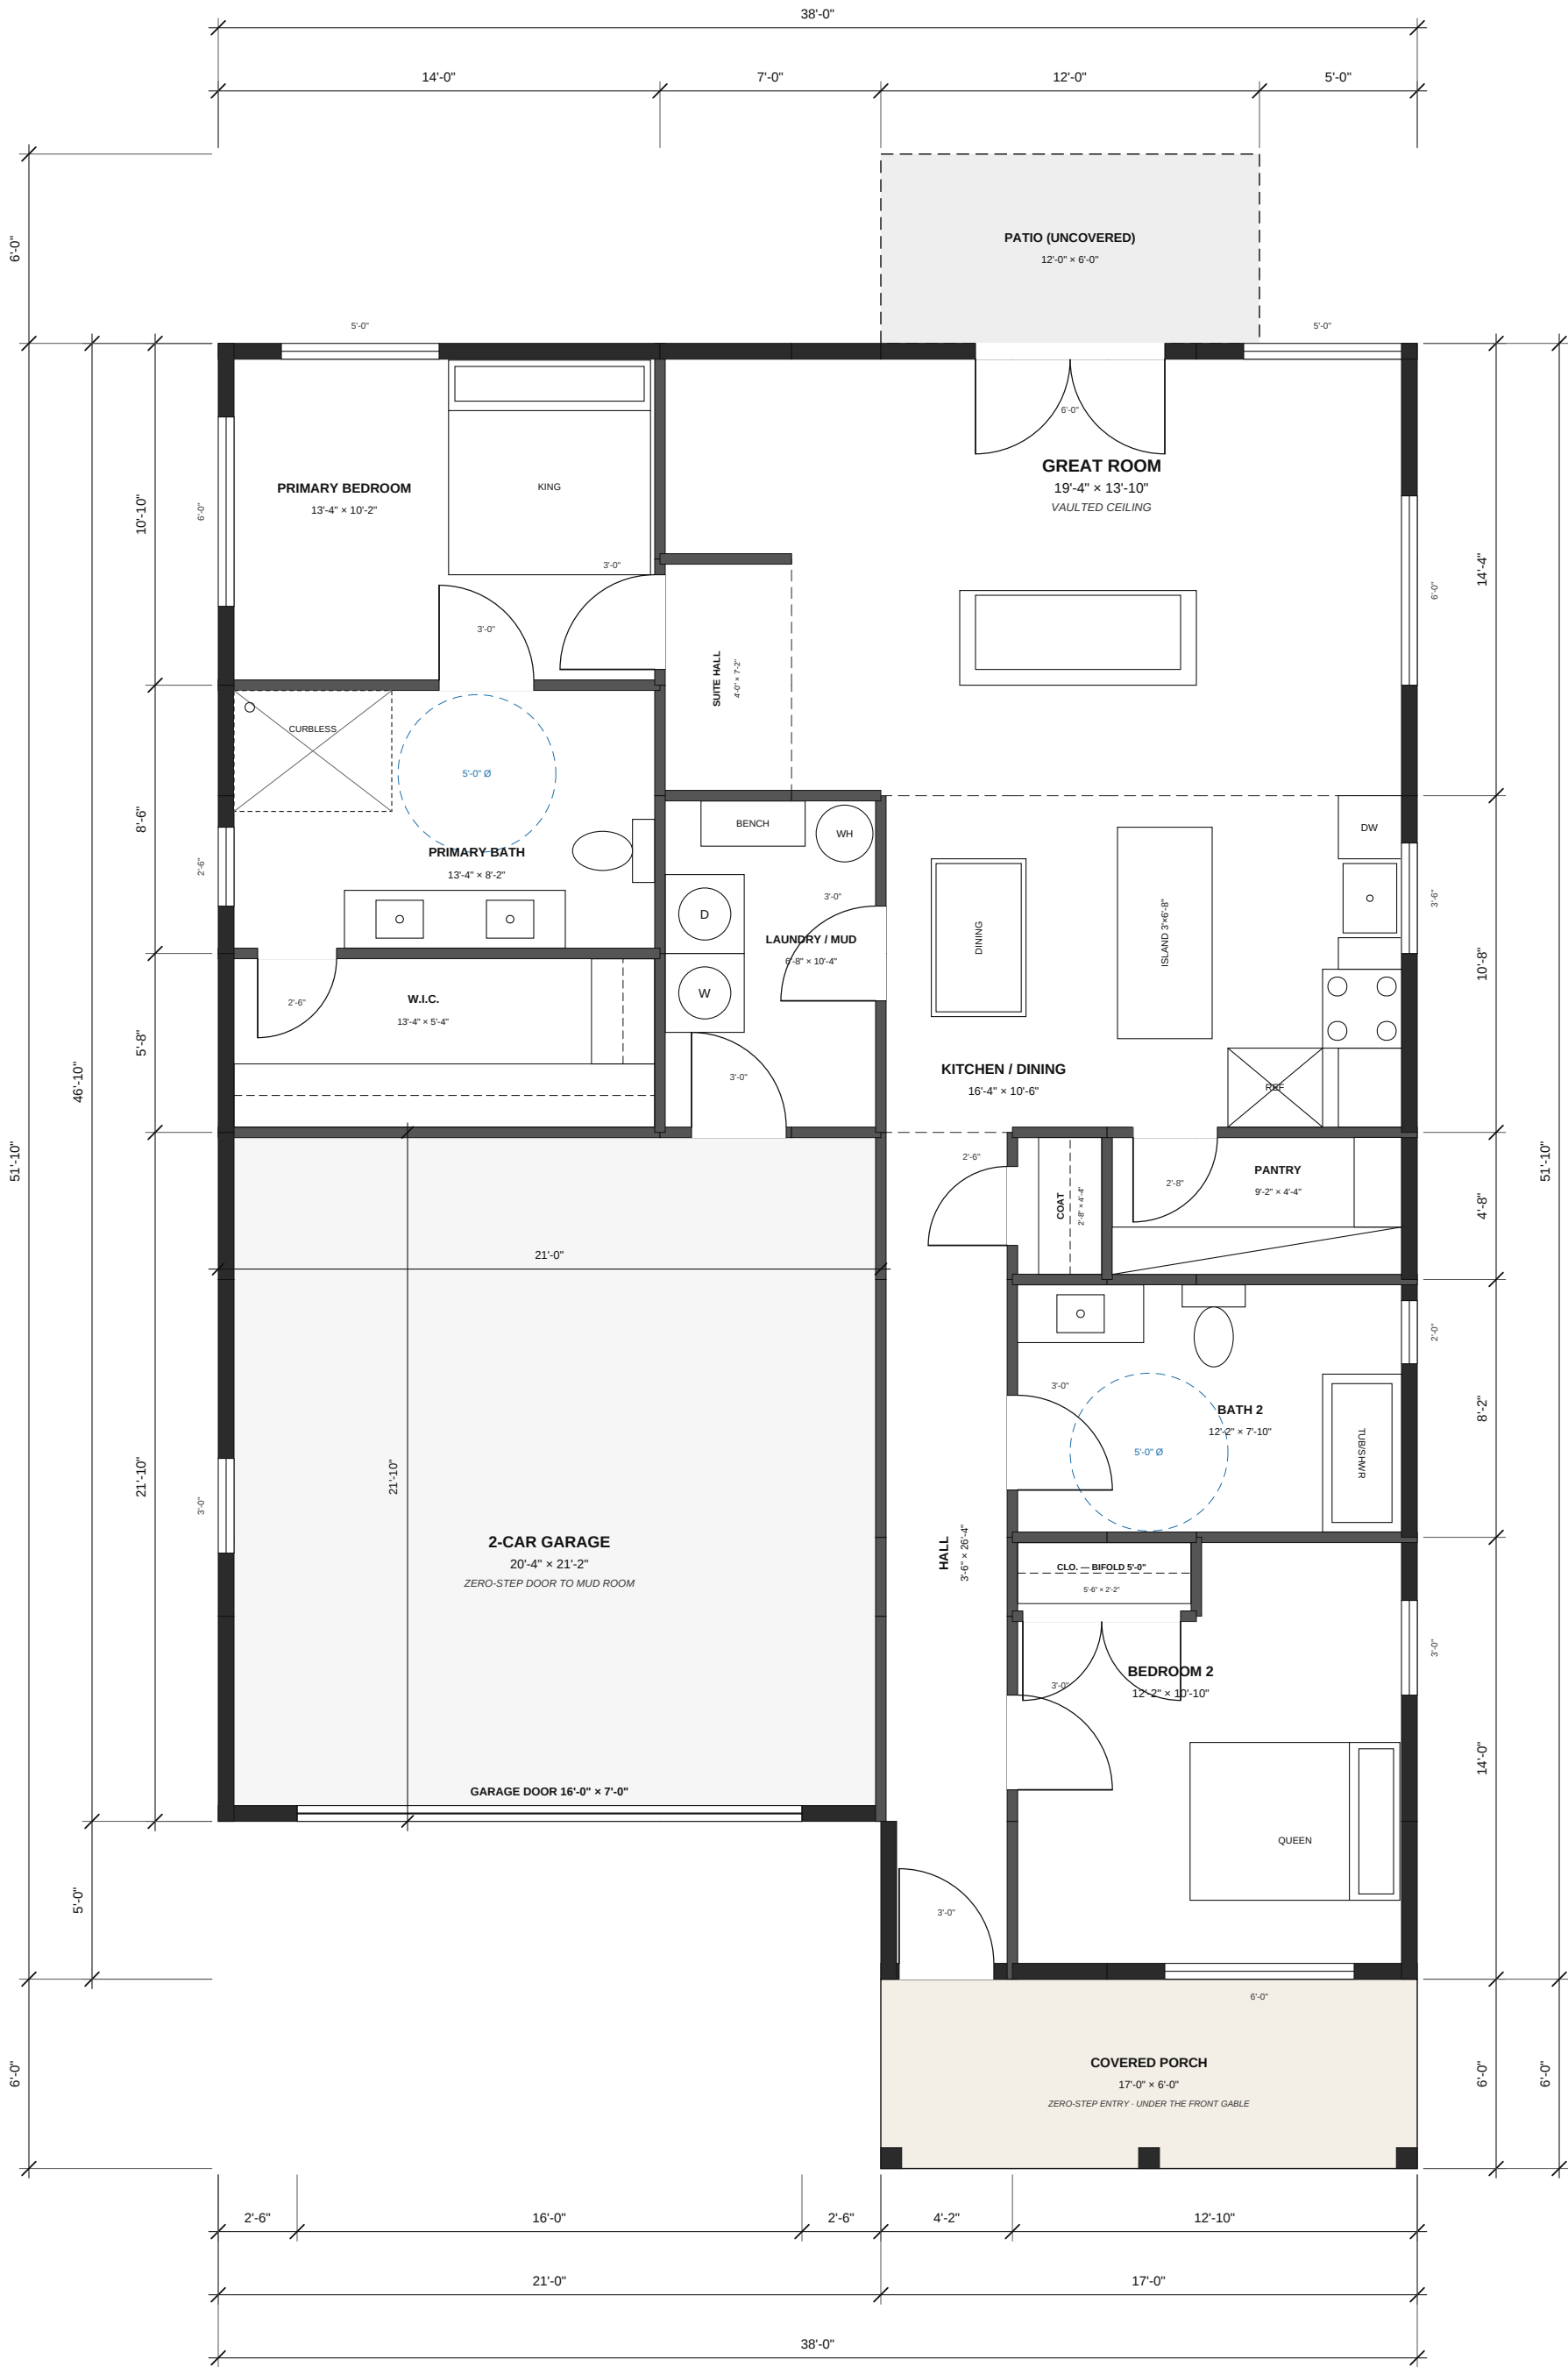

▼ FRONT — TOWARD THE LANE (ENTRY, GARAGE, PORCH FACE AT THE 15-FT SETBACK LINE) ▼

PLAN A — THE SPRINGBROOK — ILLUSTRATIVE ARCHITECTURAL PLAN — NOT FOR CONSTRUCTION — 2026-08-28

THE COTTAGES AT ARCADE SPRINGS — R-1 — R-2 REZONING (Lilburn Zoning Ordinance 2023-603 §1003-4) — 4535/4537/4539/4541 Arcade Rd SW, Lilburn GA 30047 — Land Lot 123, 6th District, Gwinnett County

Sheet A-1 - The Springbrook · Scale 3/16" = 1'-0" on ARCH C (18 × 24 in) · Prepared by the owner-applicant (Mohammed Awad) with AI drafting tools · DRAFT — to be superseded by sealed drawings (GA-registered architect)

Disclaimer: This is an AI-generated analysis for preliminary planning purposes. All findings must be verified by a licensed professional before use in design, permitting, or regulatory submissions.

<- architecture-studio/requires-disclaimer ->

GRAPHIC SCALE — 4 FT (1 FT DIVISIONS)



NORTH: see site plan (lots face the lane; N 28°43' W along the strip)