

PLAN B — THE LAUREL

2 BR + den / 2 BA, 1 story, 2-car front-loaded garage recessed 5'-0", covered front porch, covered rear porch 14'x6' (recessed), fireplace, walk-in pantry, laundry/mud room off the garage

AREA TABULATION — computed by tools/floorplans.py from the wall-face polygons

Conditioned (heated) area	1,492 SF	outside face of ext. walls
2-car garage	504 SF	outside face / centreline
Covered front porch	102 SF	slab
Covered rear porch (recessed under main roof)	84 SF	slab
TOTAL UNDER ROOF	2,182 SF	cond. + garage + porches

Program target 1,520 conditioned (FACTS §4 nominal 38'-0" × 40'-0"); Lilburn Table 4.1 R-2 cottage min heated 1,000 SF.

ROOM SCHEDULE (clear, inside face)

2-CAR GARAGE	20'-4" × 23'-4"	474 SF
FOYER / HALL	3'-6" × 28'-6"	100 SF
DEN	12'-2" × 8'-10"	107 SF
BEDROOM 2	12'-2" × 11'-2"	124 SF
CLOSET	4'-6" × 2'-2"	10 SF
BATH 2	12'-2" × 7'-8"	93 SF
LAUNDRY / MUD	6'-8" × 10'-8"	71 SF
PANTRY	3'-10" × 5'-8"	22 SF
KITCHEN	12'-2" × 10'-10"	151 SF
W.I.C.	13'-4" × 5'-8"	76 SF
PRIMARY BATH	13'-4" × 8'-2"	109 SF
PRIMARY BEDROOM	13'-4" × 13'-4"	178 SF
GREAT ROOM	23'-4" × 11'-10" + 9'-4" × 6'-0"	309 SF

ROOF / HEIGHT

main gable (rear block): span 28'-6", 8:12 ~ ridge 19'-0" above FF (plate 9'-0" + heel + rise)
front-wing gable (extended over the porch): span 17'-0", 8:12 ~ ridge 15'-2" above FF (plate 9'-0" + heel + rise)
garage gable: span 21'-0", 6:12 ~ ridge 14'-9" above FF (plate 9'-0" + heel + rise)
Max ridge 19'-0" ≤ 24 ft program cap; Ord. 2023-603 Table 4.1 R-2 max height 40 ft — appears consistent.

ACCESSIBILITY CHECKLIST (voluntary)


- Zero-step entries — front porch (slab flush with finished floor), garage-to-laundry/mud-room door and recessed rear porch (french door ≤ 1/2-in threshold) [design intent]
- Door clear width — all passage doors 36 in (3'-0"); closets/pantry 30–32 in; french doors 5'-0" (den) and 6'-0" (porch) [design intent]
- Hall width — foyer/hall 3'-6" clear (42 in), kitchen corridor 3'-10" clear [design intent]
- Turning circles — 5'-0" (60 in) circle drawn and checked clear in both baths [checked by script]
- Curbless shower — primary bath 5'-0" × 3'-10" curbless (recessed slab per 03 30 00 §2.05) [design intent]
- Out-swinging bath door — primary bath door swings into the bedroom (fall-rescue clearance) [design intent]
- Grab-bar blocking — ≥10 solid blocking 33–36 in AFF at all toilets, tub and showers (2024 IRC (GA 2026) — voluntary; ANSI A117.1 Type C-type) [design intent — VERIFY blocking heights with architect]
- Plate height / vaulted — 9'-0" plate; great room vaulted [design intent]
- Single-level living — 1 story; no interior steps; laundry/mud room on the living level off the garage [design intent]
- Lever hardware, rocker switches, 48-in max reach — to be specified (Division 08 / 26) [later stage]
- Lilburn §734 visitability — applies to attached dwellings only, voluntarily exceeded (100% zero-step) [appears consistent with Ord. 2023-603 §734 (not applicable)]

LEGEND

- Exterior wall — 2x6 @ 6 in (poché)
- Interior partition — 2x4 @ 4 in
- Cased opening / ceiling beam (no wall)
- Window (triple line), width noted
- Door leaf + swing, width noted (36 in typ.)
- 5'-0" turning circle (ANSI A117.1-type)
- Closet shelf + rod
- Covered porch slab
- Uncovered patio slab

NOTES

1. Illustrative architectural plan for the rezoning application (Lilburn Zoning Ordinance 2023-603 §1003-4 renderings/elevations item). NOT FOR CONSTRUCTION. DRAFT — to be superseded by sealed drawings by a Georgia-registered architect.
2. Dimensions are to the outside face of exterior walls (2×6, 6 in nominal) and to the centreline of interior partitions (2×4, 4 in). Plate height 9'-0"; great room vaulted; roof 8:12 main gables, 4:12 front-porch shed, architectural shingles; the rear porch is recessed under the main roof.
3. Accessibility (voluntary — Ord. 2023-603 §734 applies to attached dwellings only): zero-step entries at the front porch, garage/mud room and rear porch; 36-in passage doors; 3'-6" (42-in) clear foyer/hall; 5'-0" turning circles drawn and checked clear in both baths; curbless primary shower; out-swinging primary bath door; 2×10 blocking for grab bars at all toilets, tub and showers.
4. Garage door 16'-0" × 7'-0" recessed 5'-0" behind the front wall of the dwelling — appears consistent with Ord. 2023-603 Table 4.2 (front-loaded garages recessed ≥ 5 ft). Garage clear 20'-4" × 23'-4" ≥ the 20'-0" × 20'-0" program minimum (extra bay depth for storage / golf cart).
5. Life safety: smoke and CO alarms per 2024 IRC (GA 2026) R314/R315; bedroom emergency escape and rescue openings per 2024 IRC (GA 2026) R310 (note 9), NFPA 13D residential sprinklers are offered as a VOLUNTARY condition, not as code-required mitigation: IFC 2024 as adopted and modified by Ga. Comp. R. & Regs. R. 120-3-3-.04 replaces Appendix D107.1's 30-unit trigger with 120 dwelling units, so at 43 units a second fire-apparatus access road is not required and no sprinkler exception is being relied on. (The 1,754-ft dead-end lane still needs IFC 2024 (GA) Appendix D103.4 special approval — a site-plan issue, not a house-plan issue.)
6. BODY WIDTH — why 38'-0" and not the 40'-0" of the program brief. A 50'-0" lot less two 5'-0" side yards (Ord. 2023-603 Table 4.1, R-2) leaves 40'-0" of buildable width, and the ROOF has to fit inside it, not just the walls: at an 8-in overhang on each side wall a 40'-0" body measures 41'-4" roof to roof and does not fit. Ord. 2023-603 was searched and contains no provision permitting a projection or encroachment into a required yard (VERIFY at pre-application). The body is therefore 38'-0" wide — 38'-0" + 2 × 0'-8" = 39'-4" roof to roof, 4 in of clearance to each side-yard line — and the depth was increased 1'-0" to 58'-6" to recover floor area. Conditioned area 1,530 SF, against 1,595 SF for the superseded 40'-0" × 57'-6" version (~4.1%).
7. BODY DEPTH — why 58'-6" is the maximum. On the typical 50'-0" × 100'-0" lot the front porch face sits on the 15-ft front setback, the porch is 6'-0" deep and the rear 20'-0" of the lot is the undisturbed buffer easement (Ord. 2023-603 Table 4.1 rear yard; §313(1) buffer-in-lot reading): 100 – 15 – 6 – 20 = 59'-0" of available body depth. At 58'-6" the rear wall stands 20'-6" from the rear lot line — 6 in outside the buffer easement (the ROOF is a separate question: see the first VERIFY item — the drawn 12-in rear eave reaches 19'-6" from the rear line). Verified against data/layout.json (Plan B lot 2: lot 50 × 100, setback envelope 15 ft front / 20 ft rear, porch rect 6 ft deep).
8. Rear porch: recessing the 14'-0" × 6'-0" covered porch under the main roof keeps the roof edge on the line of the rear wall, so nothing projects past 58'-6" and the 20-ft buffer easement is not touched. No uncovered patio is proposed (an added at-grade slab would reach the buffer line — VERIFY with Planning staff).
9. EGRESS. Both bedrooms have an emergency escape and rescue opening in an exterior wall: BEDROOM 2 a 6'-0" × 5'-0" twin on the right side wall, the PRIMARY BEDROOM a 5'-0" × 5'-0" unit on the rear wall, sills at 2'-0" (22 in) above the finished floor, well under the 44-in maximum (2024 IRC (GA 2026) R310.2.2). The egress leaf of each unit is specified as a 3'-0" × 5'-0" CASEMENT: taking a 3-in allowance all round for frame, sash and hardware, net clear opening = 2'-6" × 4'-6" = 30 in × 54 in = 11.25 SF ≥ 5.7 SF, net clear width 30 in ≥ 20 in, net clear height 54 in ≥ 24 in ~ appears consistent with 2024 IRC (GA 2026) R310.2.1. A 3'-0" × 5'-0" single-hung is NOT relied on: its net clear height is roughly half the unit height and the resulting area is marginal against 5.7 SF. Companion leaves and all other windows may be single-hung.
10. Program body is nominally 38'-0" × 40'-0" = 1,520 SF (re-proportioned 2026-09-03 from the FACTS §4 nominal 40'-0" × 40'-0" = 1,600 SF — see note 6). With the 2-car garage as a front wing and the 14'-0" × 6'-0" rear porch recessed under the main roof, the conditioned envelope is a 17'-0" × 29'-0" front wing + a 38'-0" × 29'-6" rear block less the 84-SF porch notch = 1,530 SF conditioned (+0.7% on the 1,520-SF nominal); overall body 38'-0" × 58'-6" plus the front porch, 1,530 SF exceeds the ≥ 1,400-SF voluntary condition (docs/10 item 14) and the 1,000-SF minimum heated floor area for a cottage home in R-2 (Ord. 2023-603 Table 4.1).
11. Areas are computed by tools/floorplans.py from the wall-face polygons (conditioned = outside face of exterior walls; total under roof = conditioned + garage + both covered porches).

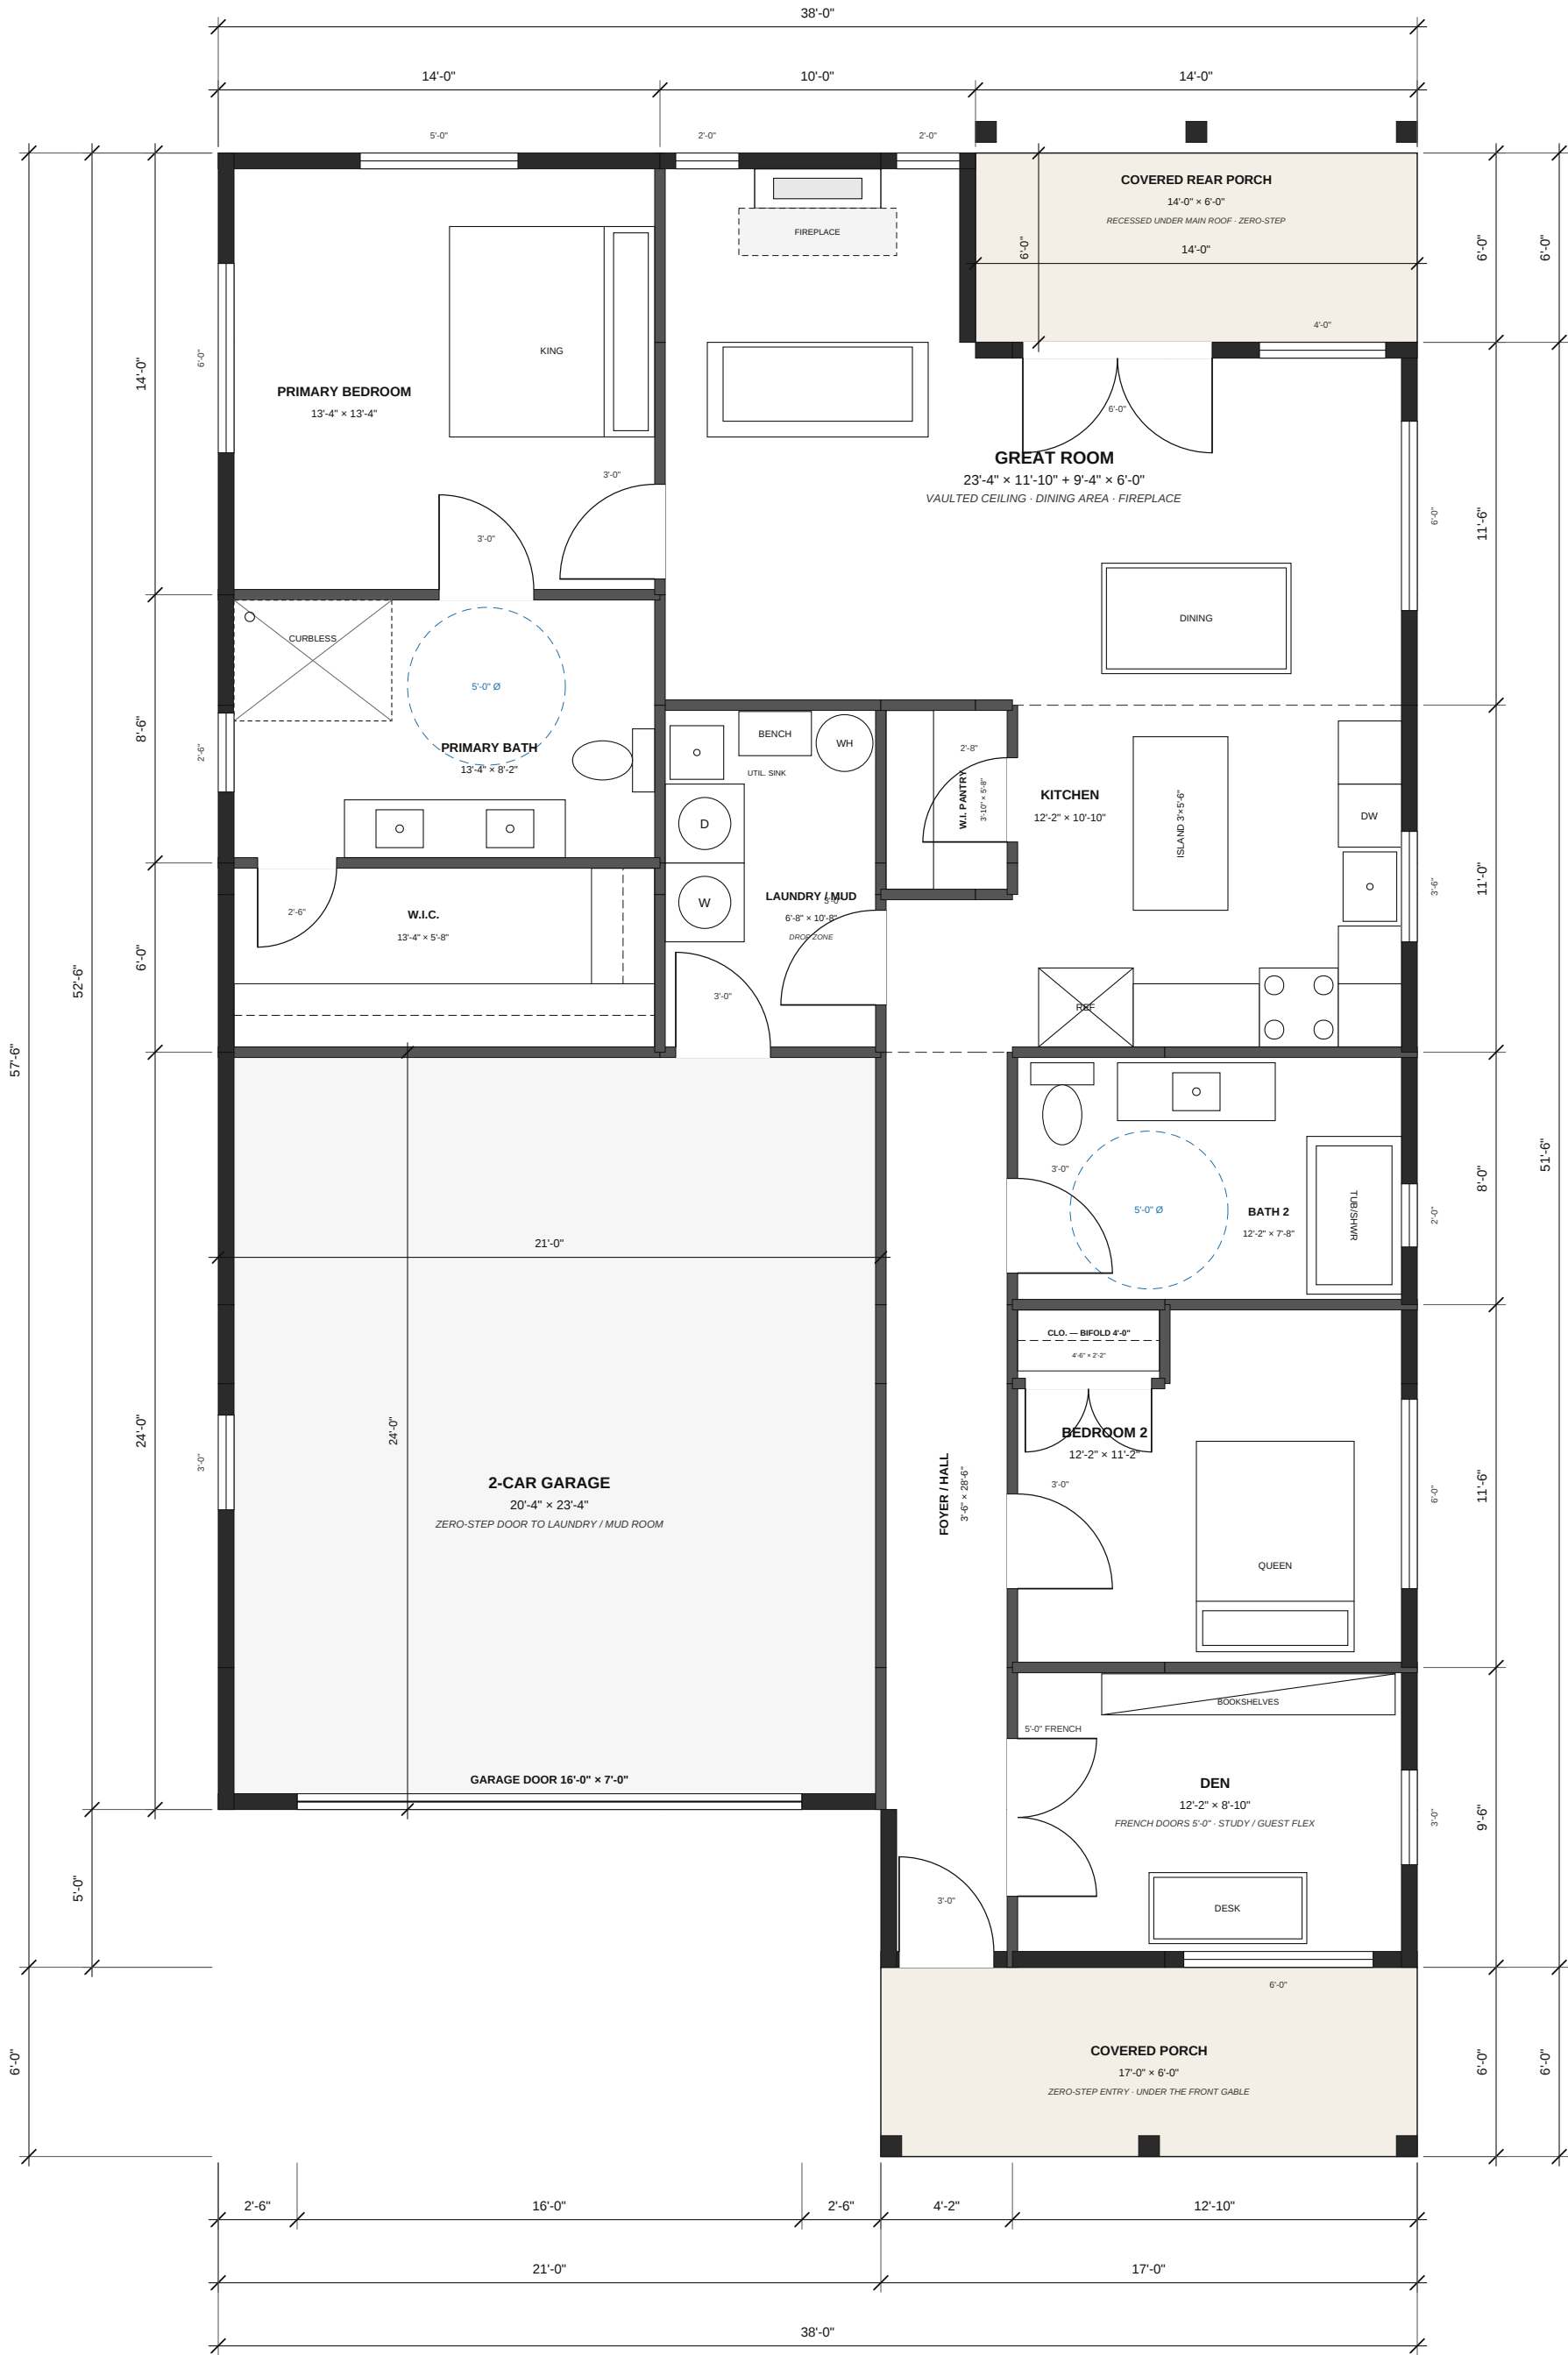

▼ FRONT — TOWARD THE LANE (ENTRY, GARAGE, PORCH FACE AT THE 15-FT SETBACK LINE) ▼

PLAN B — THE LAUREL — ILLUSTRATIVE ARCHITECTURAL PLAN — NOT FOR CONSTRUCTION — 2026-08-28

THE COTTAGES AT ARCADE SPRINGS — R-1 – R-2 REZONING (Lilburn Zoning Ordinance 2023-603 §1003-4) — 4535/4537/4539/4541 Arcade Rd SW, Lilburn GA 30047 — Land Lot 123, 6th District, Gwinnett County

Sheet A-2 : The Laurel - Scale 3/16" = 1'-0" on ARCH C (18 × 24 in) . Prepared by the owner-applciant (Mohammed Awad) with AI drafting tools . DRAFT — to be superseded by sealed drawings (GA-registered architect)

Disclaimer: This is an AI-generated analysis for preliminary planning purposes. All findings must be verified by a licensed professional before use in design, permitting, or regulatory submissions.

<-- architecture-studio/requirements-disclaimer -->

GRAPHIC SCALE — 4 FT (1 FT DIVISIONS)



NORTH: see site plan (lots face the lane; N 28°43' W along the strip)