




24'-0" MAXIMUM RIDGE ABOVE FINISHED GRADE — VOLUNTARY ZONING CONDITION (Ord. 2023-603 Table 4.1 R-2 allows 40'-0")

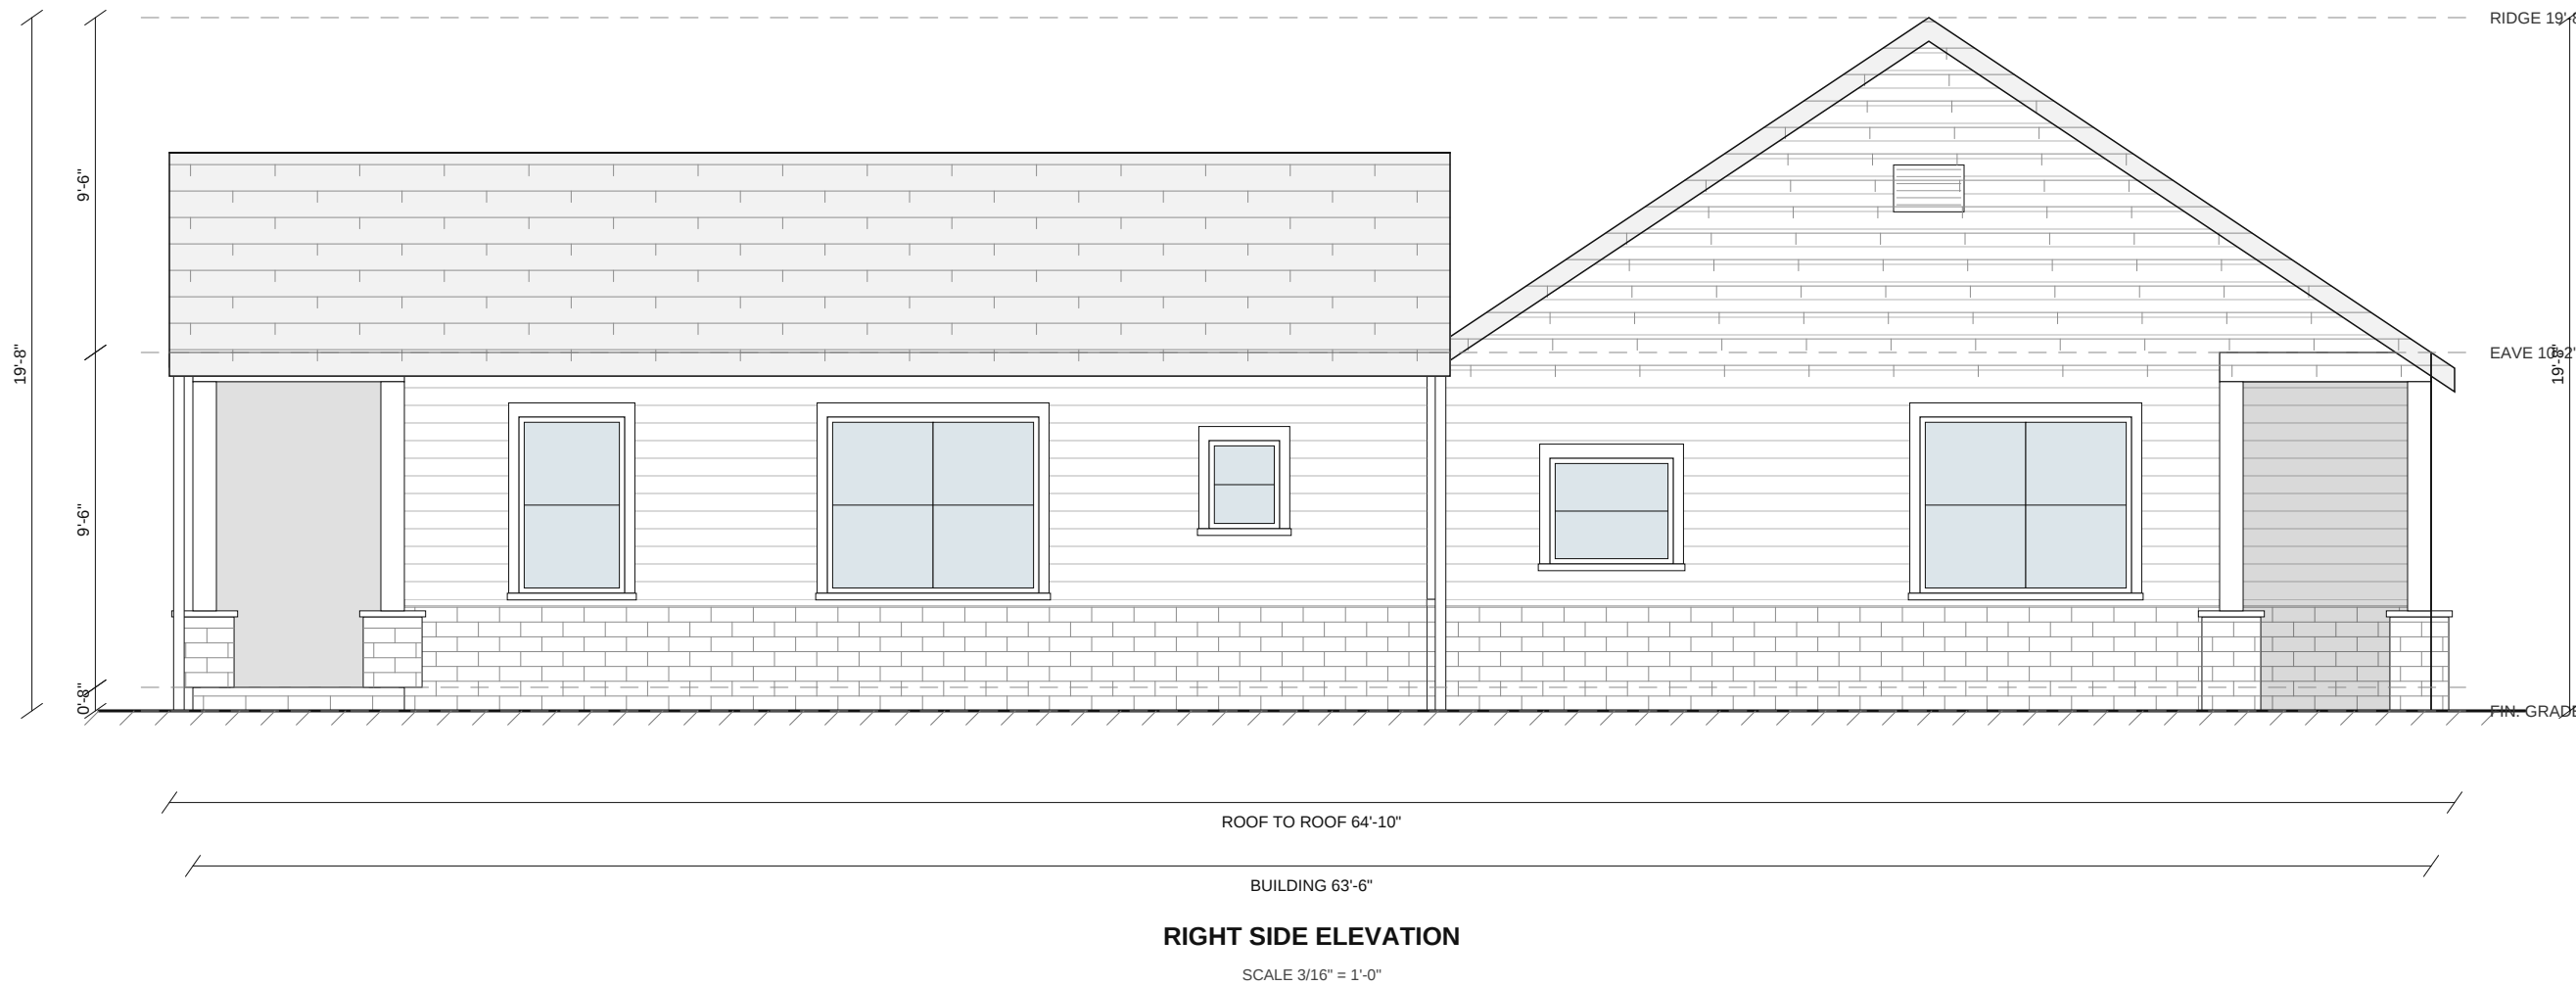


24'-0" MAXIMUM RIDGE ABOVE FINISHED GRADE — VOLUNTARY ZONING CONDITION (Ord. 2023-603 Table 4.1 R-2 allows 40'-0")

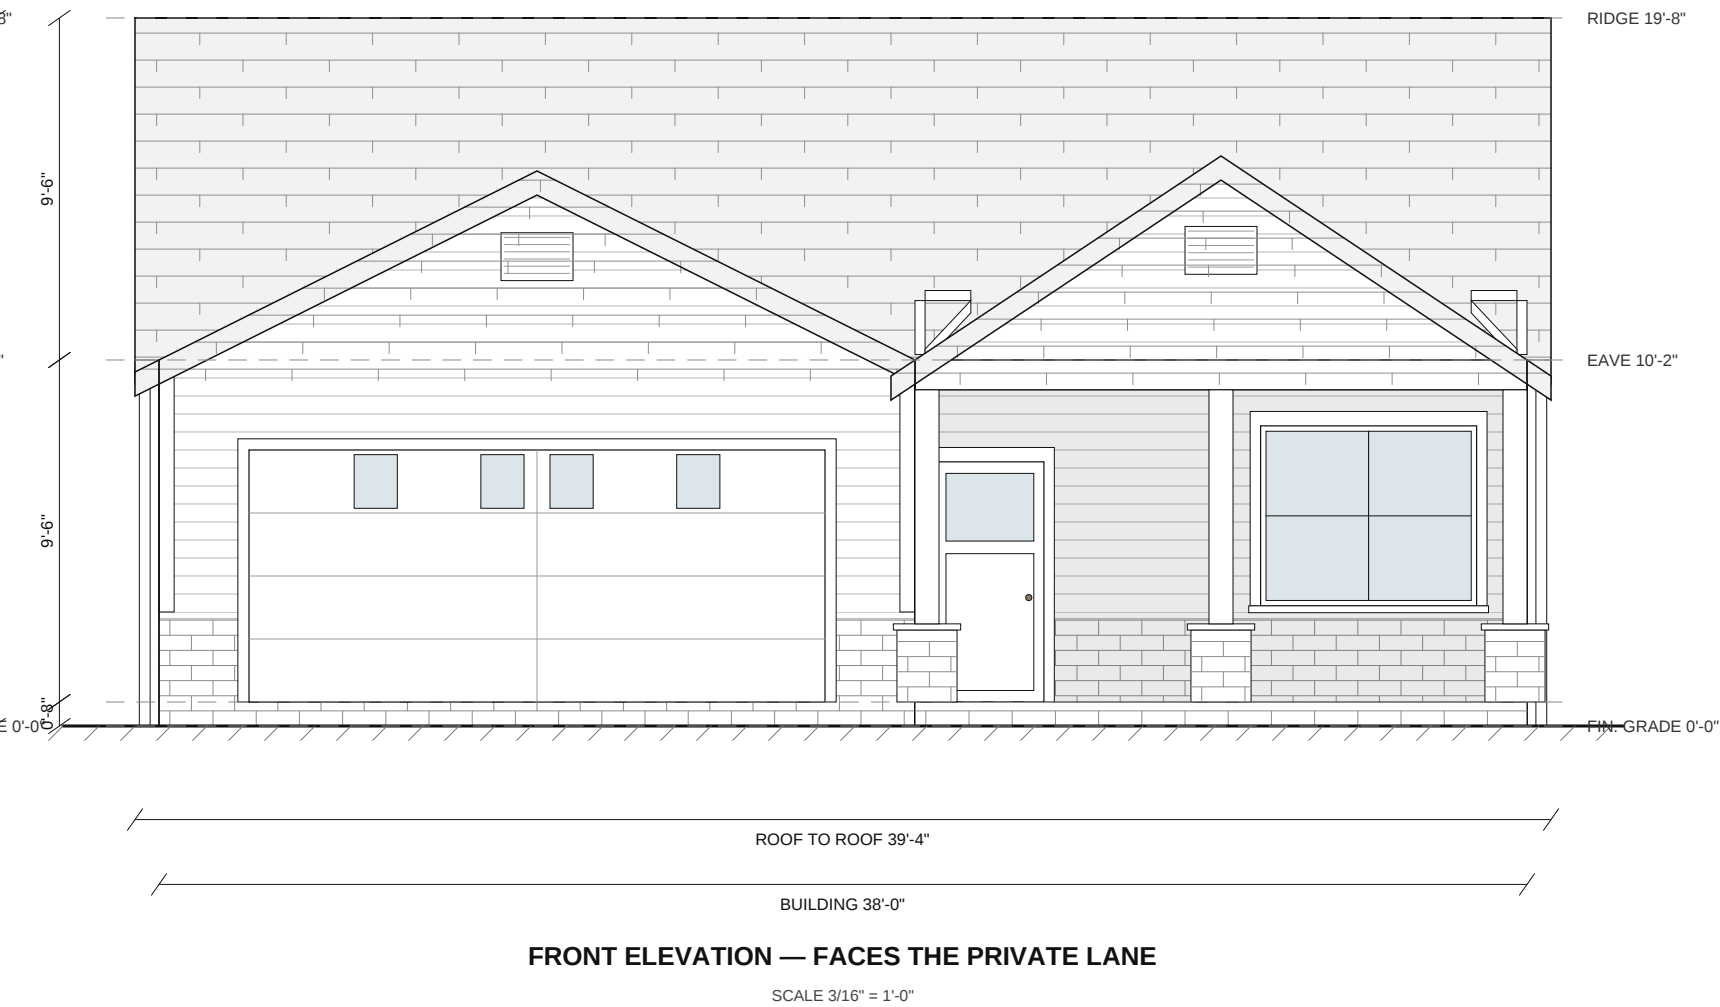

24'-0" MAXIMUM RIDGE ABOVE FINISHED GRADE — VOLUNTARY ZONING CONDITION (Ord. 2023-603 Table 4.1 R-2 allows 40'-0")

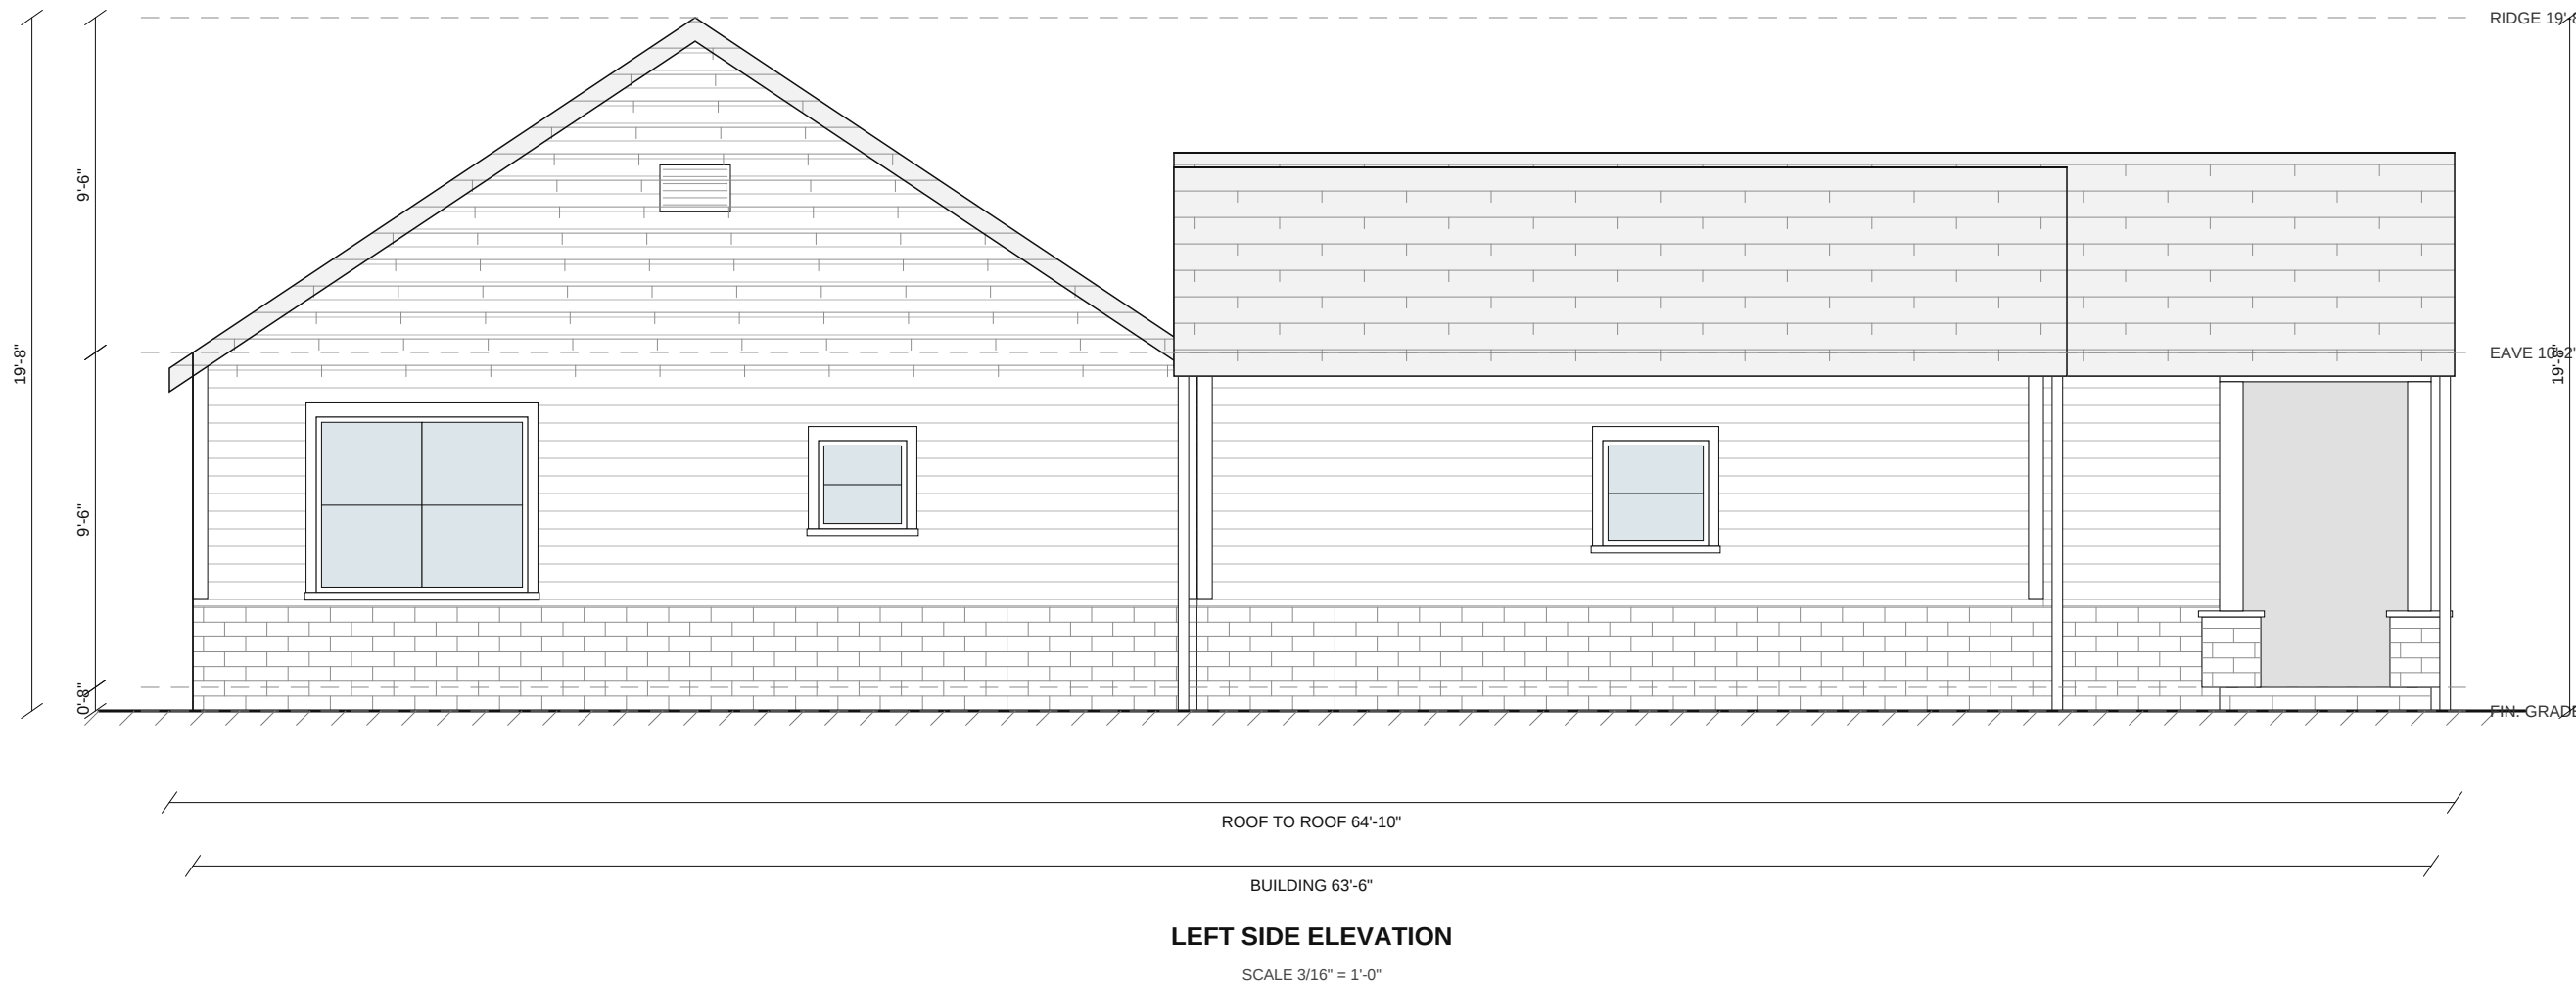

24'-0" MAXIMUM RIDGE ABOVE FINISHED GRADE — VOLUNTARY ZONING CONDITION (Ord. 2023-603 Table 4.1 R-2 allows 40'-0")

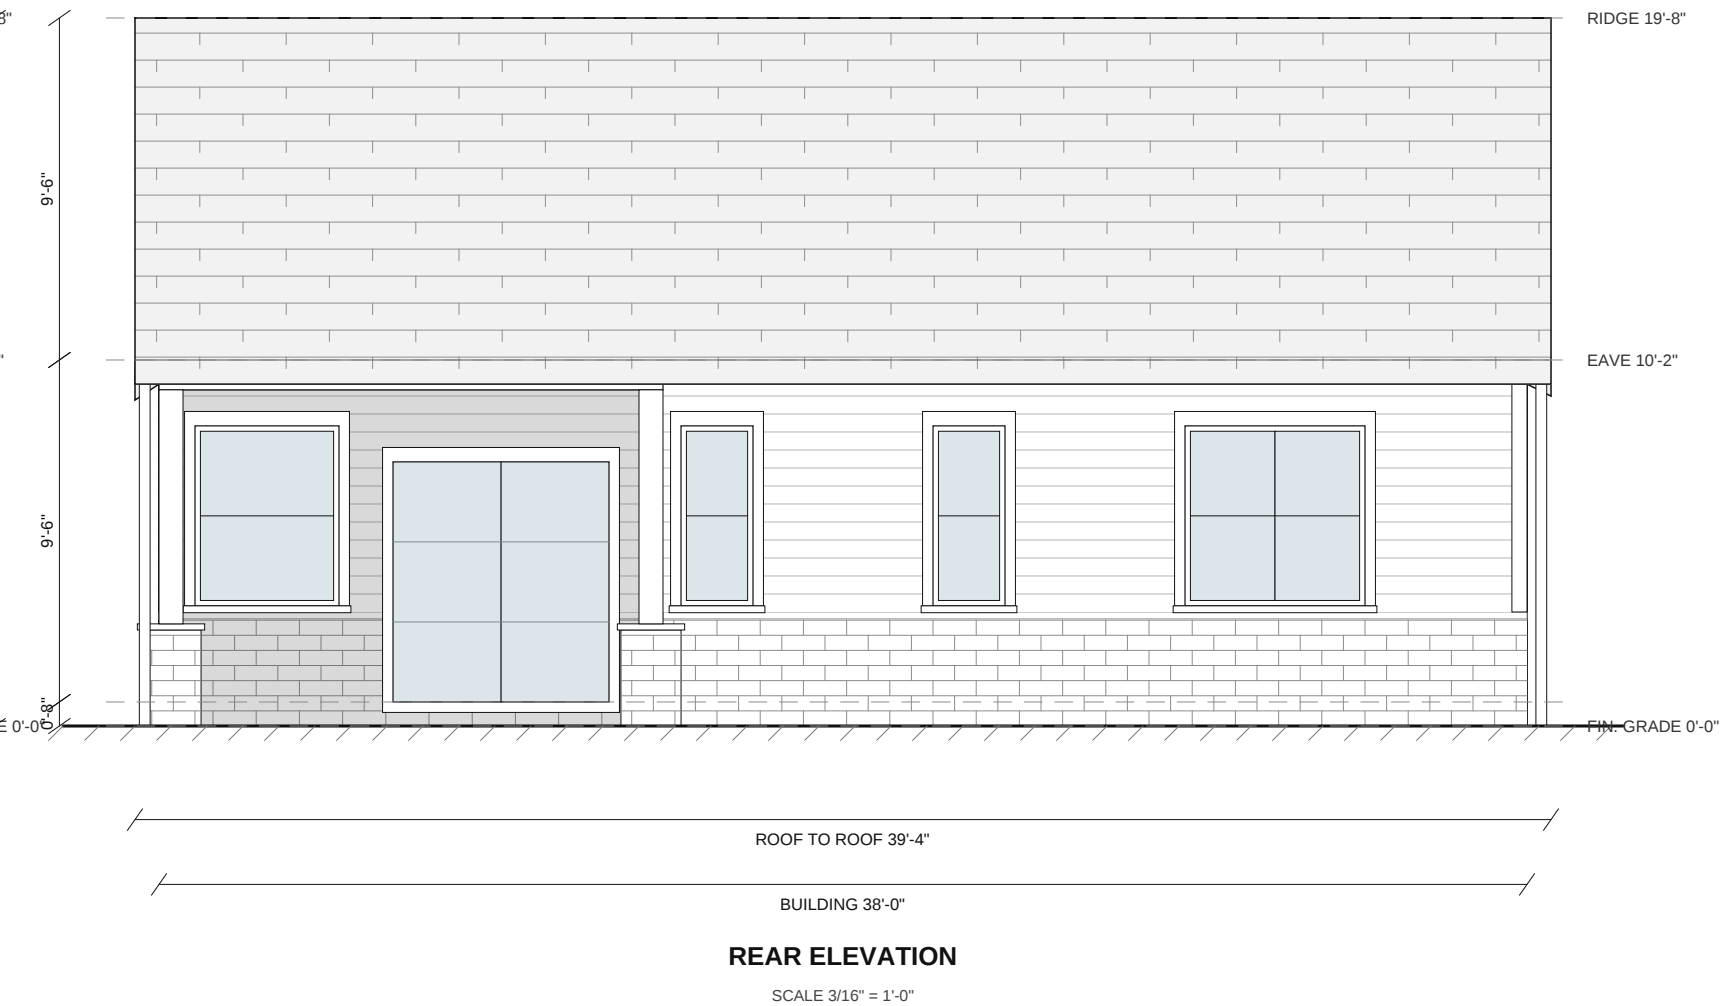

MATERIALS AND COLOURS — Application Instructions item (11)

- 1 ROOF (07 31 00)**
Architectural asphalt shingle, 30-year, over synthetic underlayment; ridge vent; 5-in K-style aluminium gutters and downspouts (07 71 00). Colour by scheme.
- 2 WALL (07 46 46)**
Fiber-cement siding: 7-1/4-in lap at 6-in exposure (schemes 2 and 3) or vertical panel with 12-in battens (scheme 1); factory finish. S/4 cellular-PVC or fiber-cement trim, corner boards and frieze (06 20 00).
- 3 BASE (04 20 00 / 04 40 00)**
Masonry water table 30 in above finished floor and porch piers: modular brick veneer (scheme 2) or adhered ledge stone (schemes 1 and 3), cast-stone cap sloped with drip.
- 4 PORCH (06 20 00)**
8x8 nominal Western Red Cedar posts on 20-in square masonry piers with cast-stone caps; cedar brackets at the gable; beadboard porch ceiling, 9'-0" flat porch ceiling.
- 5 WINDOWS (08 53 13)**
Vinyl (fiberglass alternate) single-hung and fixed units, white; 4-in flat casing with a sloped sill; grilles at the front elevation only.
- 6 DOORS (08 14 00 / 08 36 13)**
Insulated fiberglass entry door 3'-0" x 6'-8" with a glazed upper panel; carriage-style sectional garage door 16'-0" x 7'-0" with a top row of lites.

WALL SIGNS: none proposed on any dwelling, the clubhouse or an accessory structure. One ground-mounted monument entry sign not exceeding 32 SF is proposed at the Arcado Road entrance — see sheet A-4 for its elevation, dimensions, materials and colours.

HEIGHT: maximum ridge 19'-8" above finished grade — within the 24'-0" voluntary condition and well below the 40'-0" maximum of Ord. 2023-603 Table 4.1 (R-2). One story throughout; no basement.

GRADE: elevations are drawn on level finished grade. Finished floor is 0'-3" above finished grade at the front porch so the entry walk stays at or under 1.20 (zero-step entry, voluntary accessibility condition); grade falls away at the sides and rear. Lot grading is shown on sheet C-3.

THE COTTAGES AT ARCADE SPRINGS — PLAN B "The Laurel" — EXTERIOR ELEVATIONS

R-1 ~ R-2 REZONING (Lilburn Zoning Ordinance 2023-603 §1003-4; 2026 Application Instructions item (11)) — 4535 / 4537 / 4539 / 4541 Arcado Rd SW, Lilburn GA 30047 — Land Lot 123, 6th District, Gwinnett County

Scale 3/16" = 1'-0" on ARCH C (24 x 18 in) · Rev B — 2026-09-03 · Prepared by the owner-applicant (Mohammed Awad) with AI drafting tools · ILLUSTRATIVE — NOT FOR CONSTRUCTION · DRAFT, to be superseded by sealed drawings by a Georgia-registered architect

Disclaimer: This is an AI-generated analysis for preliminary planning purposes. All findings must be verified by a licensed professional before use in design, permitting, or regulatory submissions.

<- architecture-studio requires disclaimer ->

A-2.2

PLAN B "The Laurel"
2026-09-03