



CLUBHOUSE — FLOOR PLAN

2,400 SF under roof on the 60'-0" x 40'-0" footprint of Sheet C-1 — SCALE 1/8" = 1'-0"

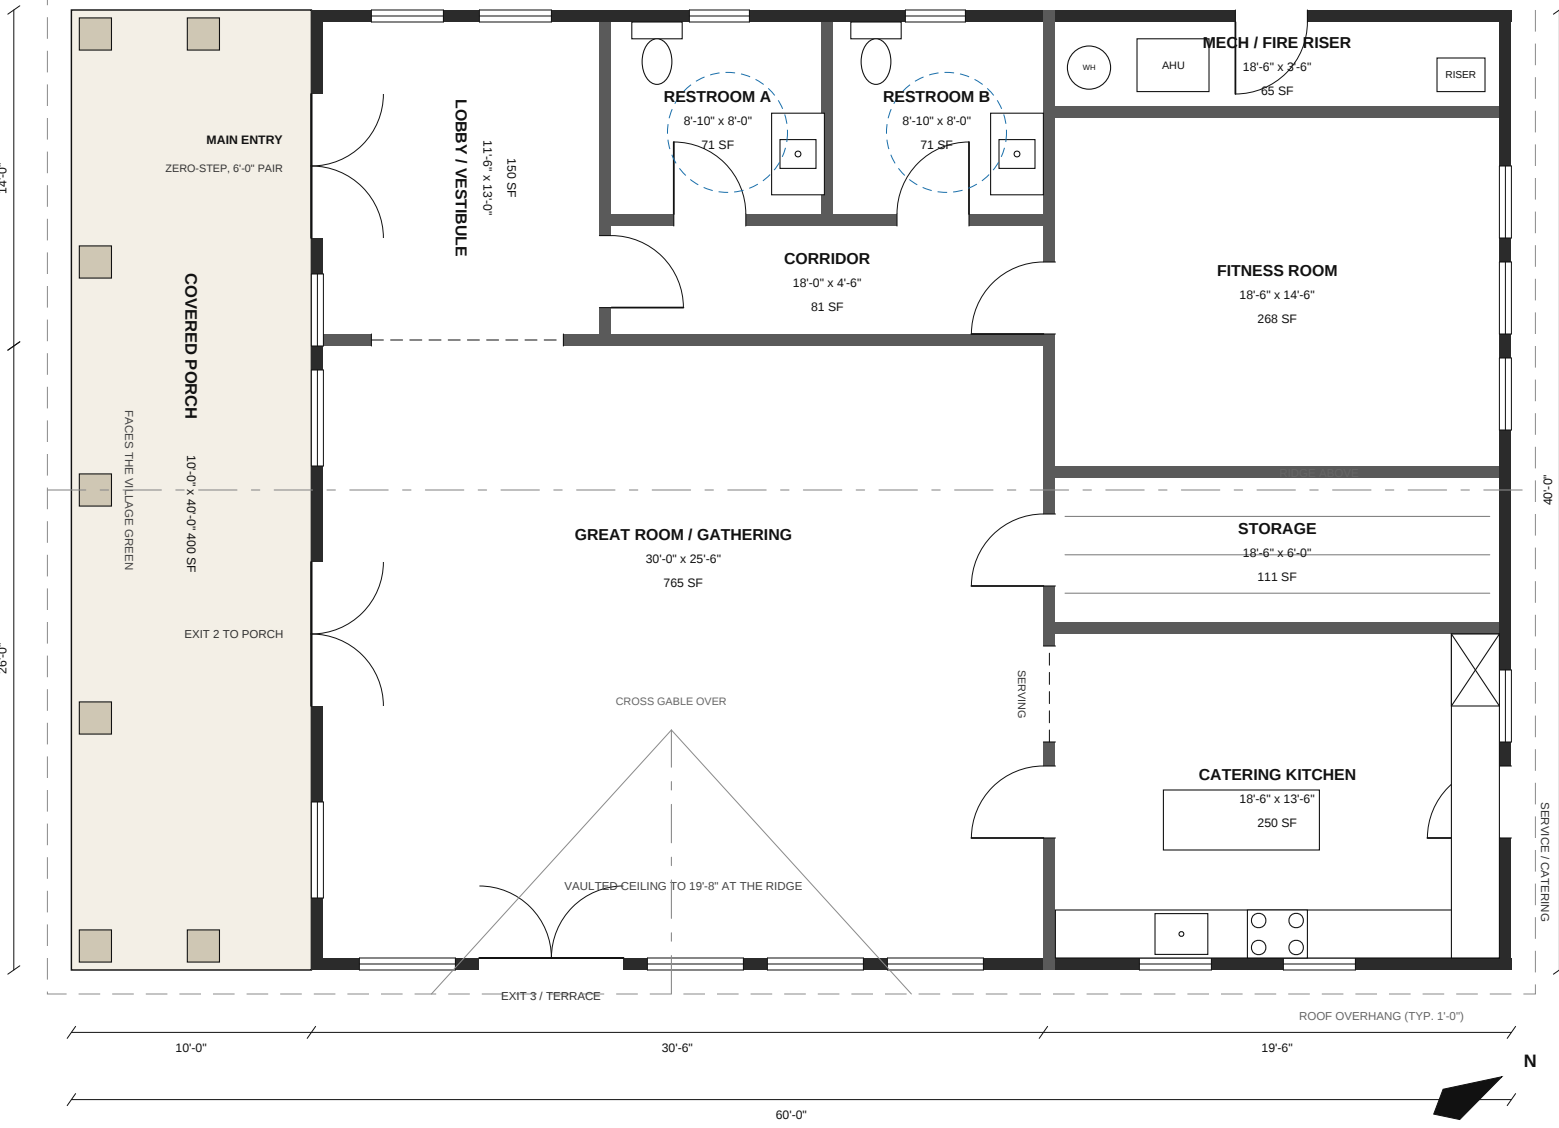


MAIL KIOSK — USPS CLUSTER BOX UNIT SHELTER

16'-0" x 10'-0" shelter and its four short-term spaces, from data/layout.json — SCALE 1/4" = 1'-0"

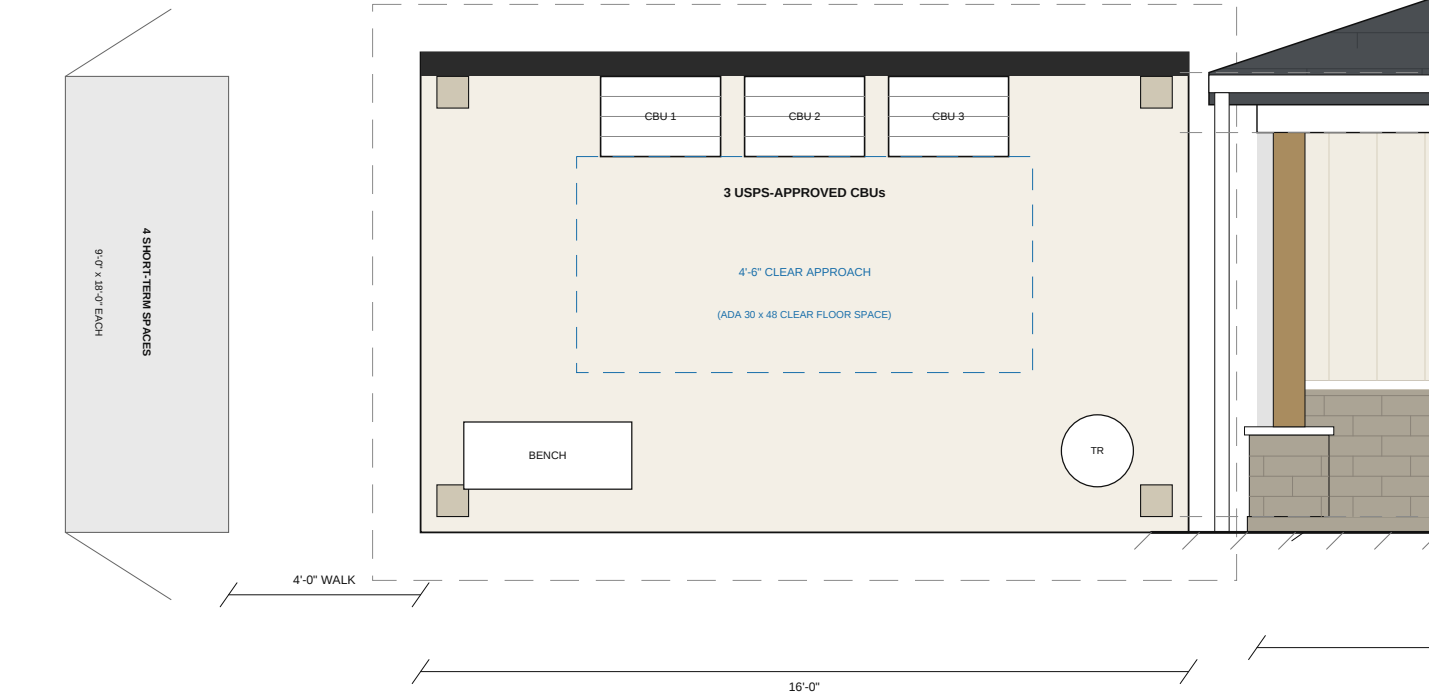

KEY PLAN — FRONT AMENITY BLOCK

The front block only — the full site is Sheet C-1 — SCALE 1" = 80'-0"

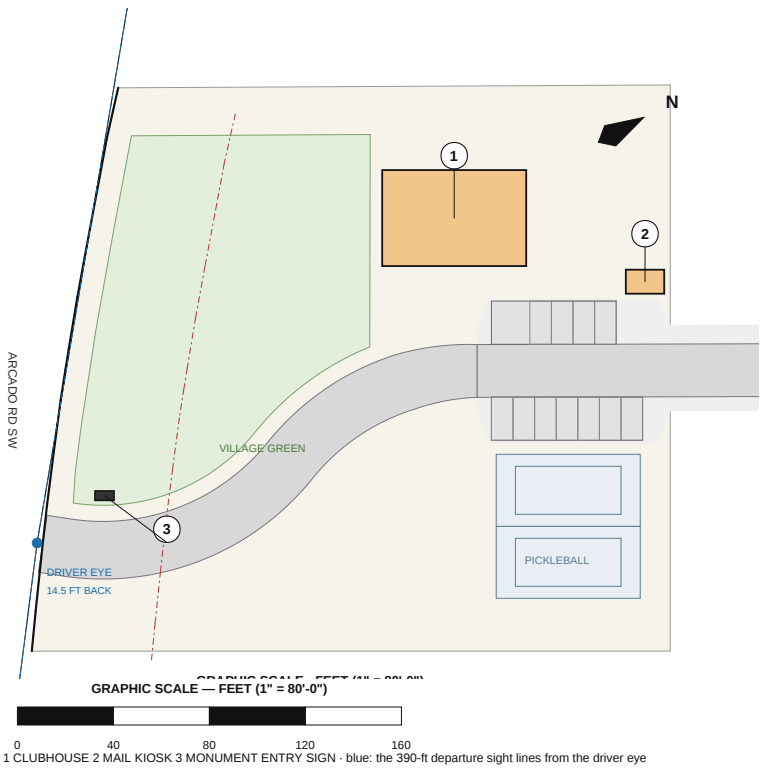

MATERIALS AND COLOURS — Application Instructions item (11)

All three non-dwelling structures are built in SCHEME 1 - WARM WHITE - the palette of Sheets A-2.1 / A-2.2 / A-2.3 and docs/12-outline-specifications.mxd. The three cottage schemes are distributed among the dwellings.



- 1. ROOF (07 31 00) Architectural asphalt shingle, 30-year, over synthetic underlayment, ridge vent, 5-in K-style aluminum gutters and downspouts (07 71 00). Colour by scheme.
- 2. WALL (07 46 46) Five-centim siding, 7-1/4-in lap at 6-in exposure (schemes 2 and 3) or vertical panel with 12-in battens (scheme 1); factory finish, 5/4 cellular-PVC or fiber-cement trim, corner boards and frieze (06 20 00).
- 3. BASE (04 20 00 / 04 40 00) Masonry water table 30 in above finished floor and porch piers: modular brick veneer (scheme 2) or adhered ledge stone (schemes 1 and 3), cast-stone cap sloped with drip.
- 4. PORCH (06 20 00) 8x6 nominal Western Red Cedar posts on 20-in square masonry piers with cast-stone caps; cedar brackets at the gable; beadboard porch ceiling; 9'-0" flat porch ceiling.
- 5. WINDOWS (08 53 13) Vinyl (fiberglass alternate) single-hung and fixed units, white; 4-in flat casing with a sloped sill; grilles at the front elevation only.
- 6. DOORS (08 14 00 / 08 36 13) Insulated fiberglass entry door 3'-0" x 6'-8" with a glazed upper panel; carriage-style sectional garage door 16'-0" x 7'-0" with a top row of tiles.

CLUBHOUSE — AREAS, HEIGHT AND OCCUPANT LOAD

Building footprint (Sheet C-1)	60'-0" x 40'-0" = 2,400 SF
Enclosed (gross, outside face)	2,000 SF
Covered porch (village green)	400 SF
Net room area (sum of rooms)	1,831 SF
Eave / ridge above finished grade	11'-6" / 21'-4"
Voluntary ridge condition / Table 4.1 max	24'-0" / 40'-0"
Setback from the Arcado Rd R/W (50 ft req.)	114.8 ft
Clear of the 20-ft NE buffer band	15.0 ft
Lane-facing wall to the lane pavement edge	29'-0"
Occupant load (IBC 2024 Table 1004.5)	71
Exts required / provided	2 / 3
Ext separation req. (1/3 diagonal) / provided	21'-4" / 35'-0"
Occupant load: Great Room 765 SF / 15 = 51; Lobby 150 SF / 15 = 10; Fitness Room 268 SF / 50 = 6; Catering Kitchen 250 SF / 200 = 2; Storage 111 SF / 300 = 1; Mech 65 SF / 300 = 1	

MONUMENT ENTRY SIGN

The only sign in the project — SCALE 3/8" = 1'-0"

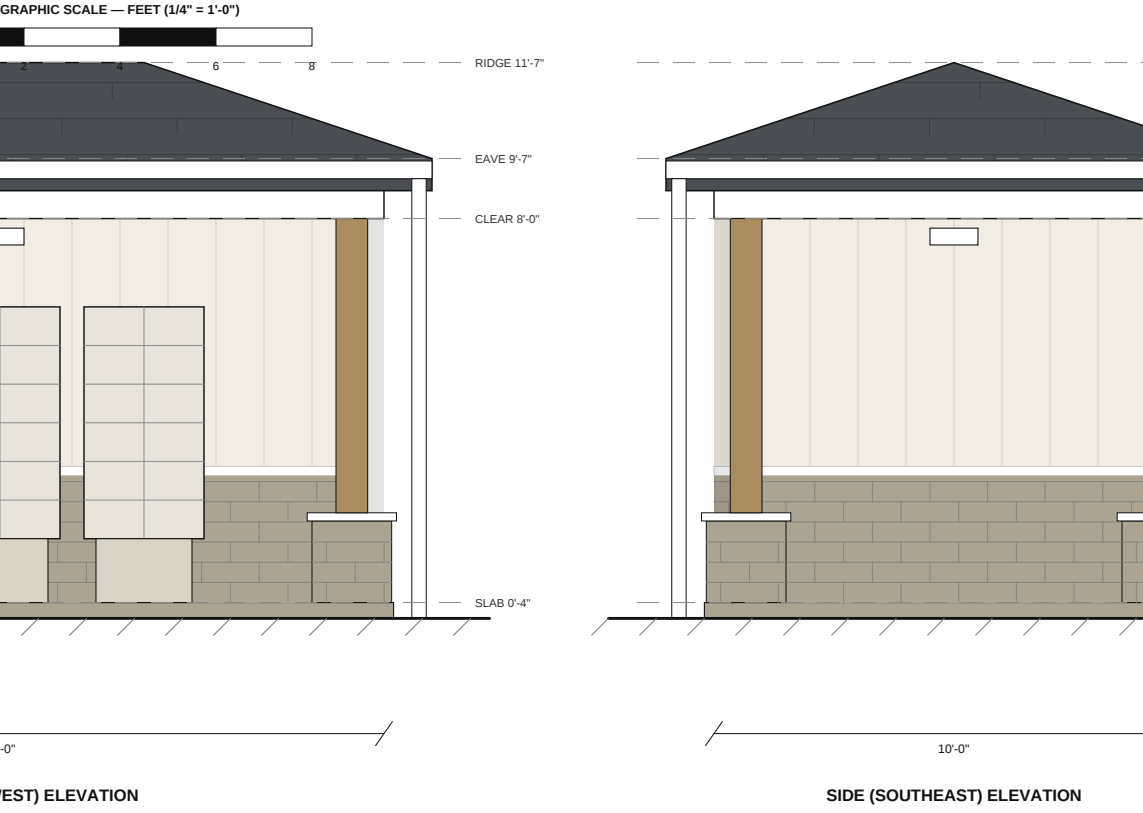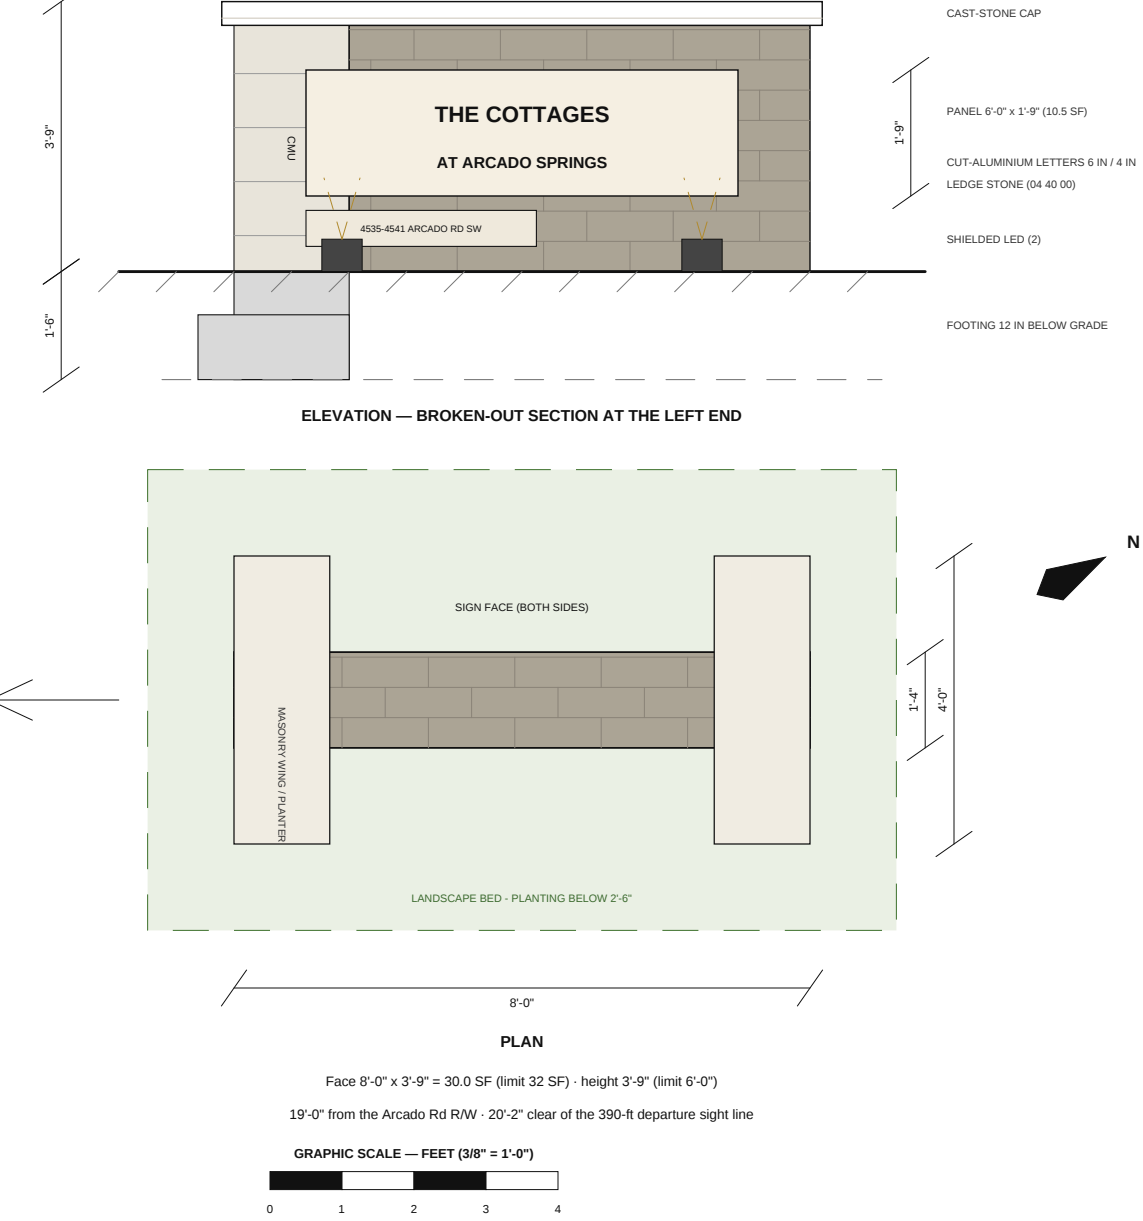

GENERAL AND CODE NOTES

- ONE GROUND-MOUNTED MONUMENT SIGN. NO WALL SIGNS ARE PROPOSED ON ANY DWELLING, ON THE CLUBHOUSE OR ON ANY ACCESSORY STRUCTURE.
- SIGN STANDARD — VERIFY: the ordinance excerpts collected for this application (site/ordinance-excerpts.mxd — Liburn Zoning Ordinance 2023-603, Articles 3 and 4, §602, §734, §81003-1005) contain NO sign article, so the permitted area, height, setback and illumination for a residential subdivision entrance sign are NOT established here. The sign is drawn to a self-imposed limit of 32 SF of face and 6'-0" of height (it is built at 30.0 SF and 5'-0"). Confirm the governing article and the area-measurement method at the pre-application conference. All signs are permitted separately and a sign easement may be required (Site Development Plan Review Checklist §4.4).
- SIGN FOOTPRINT: the 6'-0" x 4'-0" rectangle shown for the sign on Sheet C-1 is the bounding footprint of the monument, not a wall thickness: an 8'-0" long x 1'-4" thick masonry wall with a 1'-4" wide masonry wing/planter return at each end, 4'-0" deep, in a landscaped bed. Both faces carry copy, the area above is one face.
- SIGN ILLUMINATION: external only — two ground-mounted, fully shielded LED sign lights with glare louvers set in the bed and aimed at the face, cut off at the top of the cap so no light is emitted above the horizontal; 3000K maximum, photocell and timer, spill 0.1 fc or less at any property line. A shielded, downward-directed cap-mounted LED downlight is an approved alternate. No internal illumination, no exposed lamps, no changeable copy (docs/12 10 14 00 2.05).
- SIGHT DISTANCE: intersection sight distance 350 ft at 35 mph (Gwinnett County Unified Development Ordinance §900-40 Table 900.2, AASHTO Case B1; docs/08 Memo A, docs/11 59). The departure sight triangle is struck from a driver eye 14.5 ft behind the rear edge of the travelled way on the drive centreline. The sign stands 20'-0" behind that point and its nearest corner is 20'-2" clear of the nearer sight line; no part of the sign or its bed lies within the triangle. Planting in the bed is held below 2'-6". A field sight-distance survey and the Gwinnett DOT driveway permit govern - VERIFY.
- MAIL DELIVERY (City of Lilburn Site Development Plan Review Checklist §4.1): a cluster-box system is proposed for the entire project and one street name serves all house numbers. Contact the Lilburn Post Office Growth Manager before construction drawings. The checklist directs "accessory structure details with protection from the elements" — the shelter above provides a roofed, three-sided enclosure over the boxes with a closed northeast wall, a clear approach and a bench.
- CLUBHOUSE OCCUPANCY AND SPRINKLERS: Group A-2 with accessory Group B, Type V-B construction, one story, no basement (IBC 2024 (GA 2026) §303.4, Table 603). Sprinklered throughout under NFPA 13 and monitored; the 43 dwellings are sprinklered under NFPA 13D (voluntary condition 5, docs/0C Memo E). Knox box at the clubhouse. Fire-riser room with a direct exterior door on the northeast elevation. VERIFY the occupant load, exiting and panic hardware with the Gwinnett County Fire Marshal at plan review.
- ACCESSIBILITY: accessible route from the van-accessible space in the guest bay across the lane at a marked crossing with flush ramps to the porch and a zero-step entry (finished floor 0'-0" above finished grade, entry walk 1.20 ft or flatter). Two single-user accessible toilet rooms, each with a 60-in turning circle and grab-bar blocking; 36-in doors throughout; a 34-in accessible counter segment in the kitchen. 2010 ADA Standards and ICC A117.1-2017 - final layouts by the Architect.
- PLUMBING: as an occupant load of 71, IPC 2024 (GA 2026) Table 403.1 (A-3) calls for 1 water closet and 1 lavatory per sex, a drinking fountain and a service sink. Two single-user accessible toilet rooms, a bottle-filler/fountain at the corridor and a service sink in the kitchen appear consistent - VERIFY at plan review.
- HEIGHTS (Checklist §4.4, height at the highest point): clubhouse ridge 21'-6", mail kiosk ridge 11'-7", monument sign 9'-9" above finished grade — each below the 24'-0" voluntary ridge condition and the 40'-0" maximum of Ord. 2023-603 Table 4.1 (R-2). The clubhouse gable is 6.12, not the cottages: 8.12, over the 40'-0" span an 8.12 roof puts the ridge 24'-10" above finished grade, above the voluntary condition. Materials, trim, porch and detailing are the cottages: Kiosk 4-12 to, subordinate.
- CLUSTER BOX UNITS: 41 dwellings served by 3 USPS-approved 16-compartment CBUs = 48 tenant compartments (7 spare, 15%) and 6 parcel lockers, plus an outgoing-mail slot. Compartments assigned to residents needing accessible reach are to fall between 15 in and 48 in above the slab (ICC A117.1-2017 308, USPS-STD-4C). Model, dimensions and the final count are VERIFY items with USPS.
- PARKING AT THE KIOSK: 4 short-term spaces, 9'-0" x 18'-0" each (Checklist §4.4), in an 36'-0" x 18'-0" bay 4'-0" southeast of the shelter slab; 8 guest spaces (one van-accessible) serve the clubhouse across a marked crossing of the lane (Sheet C-1). The shelter slab stands 21'-0" from the edge of the 22'-0" lane pavement and 14'-0" behind the back of the 5'-0" sidewalk (11'-0" pavement half-width + 2'-0" strip + 5'-0" walk).
- Accessory structures are set back at least 5 ft from any lot line and any required buffer (Checklist §4.1 and §4.4); the clubhouse stands 114.8 ft from the Arcado Rd R/W against the 50-ft collector setback of Ord. 2023-603 Table 4.1 and 15.0 ft clear of the 20-ft northeast buffer band.
- DRAFT - NOT SEALED. These are concept drawings by the owner-applicant for the rezoning hearing. The clubhouse and the kiosk must be designed and sealed by a Georgia-registered architect and engineer before permit; the sign requires a separate sign permit and, if it exceeds 6 ft or 32 SF, a Georgia PE footing design (docs/12 10 14 00 1.09).

CLUBHOUSE — EXTERIOR ELEVATIONS, ALL FOUR SIDES

Application Instructions item (11): an elevation of each side visible from the street — SCALE 1/8" = 1'-0" — SCHEME 1 - WARM WHITE



CLUBHOUSE ROOF AND HEIGHT — HOW THE NUMBERS ARE DERIVED

ROOF GEOMETRY, computed from this plan: plate 10'-0" above finished floor + 0'-10" raised heel = eave 10'-10" AFF; main gable span 40'-0" (eave plate to eave plate) at 6.12 gives a rise of 10'-0", so the ridge is 20'-10" AFF and, with the finished floor 0'-8" above finished grade, 21'-6" above finished grade. The cross gable over the great room spans 20'-0" at 6.12, 15'-10" AFF, and dies into the main roof 10'-0" in from the eave. Roof overhangs 1'-0" at the eaves and 1'-0" at the rakes; the 60'-0" x 40'-0" rectangle on Sheet C-1 is the wall and porch-slab footprint, not the roof edge.

THE COTTAGES AT ARCADE SPRINGS — CLUBHOUSE, MAIL KIOSK AND ENTRY MONUMENT SIGN — PLANS, ELEVATIONS AND DETAILS

R-1 ~ R-2 REZONING (Liburn Zoning Ordinance 2023-603 §1003-4; 2026 Application Instructions item (11)) — 4535 / 4537 / 4539 / 4541 Arcado Rd SW, Lilburn GA 30047 — Land Lot 123, 6th District, Gwinnett County

Scales as noted — clubhouse 1/8" = 1'-0"; mail kiosk 1/4" = 1'-0"; monument sign 3/8" = 1'-0"; key plan 1" = 80'-0" — on ARCH C (24 x 18 in) - Rev B — 2026-09-03 - Prepared by the owner-applicant (Mohammed Awad) with AI drafting tools - ILLUSTRATIVE — NOT FOR CONSTRUCTION - DRAFT, to be superseded by sealed drawings by a Georgia-registered architect

Disclaimer: This is an AI-generated analysis for preliminary planning purposes. All findings must be verified by a licensed professional before use in design, permitting, or regulatory submissions.

<- architecture studio requires disclaimer ->

A-3

CLUBHOUSE, MAIL KIOSK AND ENTRY MONUMENT SIGN

2026-09-03