

THE COTTAGES AT ARCADE SPRINGS

SHEET C-0.0 — COVER SHEET, SHEET INDEX AND VICINITY MAP

APPLICATION TO REZONE 9.44 ACRES FROM R-1 TO R-2 — 41 ONE-STORY DETACHED 55+ (HOPA) COTTAGE HOMES ON FEE-SIMPLE LOTS, 4.34 DU/AC

Use: "Single-family (cluster-cottage, creative lot configuration)" — permitted in R-2 by Lilburn Zoning Ordinance 2023-603 §602 Use Table. No special use permit requested.

4535, 4537, 4539 and 4541 Arcado Road SW, Lilburn, Georgia 30047 — Land Lot 123, 6th District, Gwinnett County — PINs R6123 033, R6123 015, R6123 014 and R6123 162

City of Lilburn, Gwinnett County, Georgia — Department of Planning and Zoning, 340 Main Street. Filed under Ord. 2023-603 §1003 and the 2026 Application Instructions (11 items).

DRAFT — NOT SEALED

OWNER, CONTACTS AND DESIGN PROFESSIONALS

Site Development Plan Review Checklist §1.e.1 — a blank line means no such professional is engaged

ROLE	NAME	ADDRESS	PHONE / E-MAIL
Owner / applicant	Mohammed Awad — owner of record, PINs R6123 033 and R6123 015	4541 Arcado Rd SW, Lilburn, GA 30047-3968	
Co-applicant owner	Santos C. Mendez and Lesvia Rosario Roblero de Leon — owners of record, PINs R6123 014 and R6123 162	4535 Arcado Rd SW, Lilburn, GA 30047-3968	
24-hour contact	Mohammed Awad — 24-hour emergency contact for the site	4541 Arcado Rd SW, Lilburn, GA 30047-3968	
Designer / preparer	Owner-prepared, AI-assisted drafting. NOT A DESIGN PROFESSIONAL.	As above	
Land surveyor (RLS)	NOT YET ENGAGED		
Civil engineer (PE)	NOT YET ENGAGED		
Architect (GA RA)	NOT YET ENGAGED		
Landscape architect	NOT YET ENGAGED		
Geotech. engineer	NOT YET ENGAGED		
Stream delineation	NOT YET ENGAGED		
Traffic engineer	NOT YET ENGAGED		
Attorney	NOT YET ENGAGED		
City contact	Reid Turner, Planning Director, City of Lilburn	340 Main St, Lilburn, GA 30047	(770) 279-3715 returner@cityoflilburn.com

ZONING AND PROPOSED USE DATA

Checklist §1.e.1, §4.b and §4.c ("required versus provided"); Lilburn Zoning Ordinance 2023-603 Tables 4.1, 4.2 and 8.1

ITEM	REQUIRED / PROVIDED
Existing zoning	R-1, Single-Family Residential, City of Lilburn — all four parcels (Ord. 2023-603 §401)
Proposed zoning	R-2, Medium-Density Residential, City of Lilburn (Ord. 2023-603 §402)
Proposed use	"Single-family (cluster-cottage, creative lot configuration)" — P (permitted by right) in R-2, §602 Use Table. No special use permit; no commercial, attached or multi-family use.
Occupancy	55+ Housing for Older Persons (42 U.S.C. §3607(b)(2)(C); 24 CFR Part 100 Subpart E) by voluntary condition and recorded covenants. 0 students generated.
Gross site area	9.44 ac deeded (411,206 SF) = 0.99 + 2.00 + 2.00 + 4.45 ac; 9,577 ac (417,174 SF) GIS-calculated. THE SEALED RLS SURVEY GOVERNS.
Lots / dwelling units	41 one-story detached cottage homes on fee-simple lots; 2 plan types; HOA-maintained yards
Gross density	PROVIDED 4.34 du/ac deeded (4.28 GIS) — REQUIRED max. 8.0 du/ac (Table 4.1, R-2)
Lot area / width / depth	PROVIDED 5,000 SF typical, 50'-0" x 100'-0" — REQUIRED min. 3,000 SF, 50 ft, 100 ft (Table 4.1, cottage home)
Setbacks	PROVIDED / REQUIRED from 15'-0" from the lane tract and 50'-0" from the Arcado Rd RW; side 5'-0"; rear 20'-0"; accessory 5'-0" (Table 4.1)
Buffer abutting R-1	PROVIDED / REQUIRED 20'-0" undisturbed on every line but the Arcado Rd frontage, within the lots as a recorded easement (§313(1)) — see note 14
Height / floor area	PROVIDED 1 story, ridge 19.0 ft; 1,406 and 1,492 SF conditioned (38'-0" × 51'-10" and 38'-0" × 57'-6" bodies) — REQUIRED max. 40 ft, min. 1,000 SF heated
Parking	PROVIDED 164 on lot (2-car garage + 2-car drive) + 12 guest and kiosk spaces incl. 1 van-accessible — REQUIRED 82 (Table 8.1, 2 per DU, no maximum)
Common open space	PROVIDED 141,089 SF = 3.24 ac = 33.8% of gross, in common tracts. Development Regs. §5.9 does not apply below 50 ac (note 13), so this is voluntary.
Streets	One private lane 1,754 ft long in a private tract; all components to meet the minimum public-street standards (Checklist §4.s). None offered for dedication.
Acreage disturbed	7.54 ac on site. Off-site: the Phase-2 sewer corridor, about 178 ft, quantified on Sheet C-4.0 (Checklist §4.e).
Adjoining zoning	R-1, City of Lilburn, single-family, on every property line. Nearest R-2 about 106 ft NE; unincorporated Gwinnett R-100 about 314 ft. Owners: docs/06 and Sheet C-1.0.
Water and sewer	Gwinnett County Dept. of Water Resources — water and sanitary sewer only. All other utilities by private providers (note 11).
Frontage / access	237.4 ft on Arcado Rd SW (chord); one entrance in the SW third of the frontage, about 252 ft from the Arcadia Pl centreline. No lot takes access from Arcado Rd.

Quantities are read at plot time from data/layout.json (regenerated 2026-09-03) and data/plans.json — the quantities actually drawn on Sheet C-2.0. The full required-versus-provided table for Articles 4, 5 and 8 is on Sheet C-2.0.

REZONING SUBMITTAL INDEX — 2026 APPLICATION INSTRUCTIONS

ITEM	PROVIDED
1 Application Form	docs/01-application-form-data.md
2 Application Fee	\$1,250 — see APPLICATION DATA in the title banner above
3 Standards Governing the Zoning Power (§1003-7)	docs/04 — the six §1003-7 criteria
4 Conflict of Interest Form (§36-67A-3)	docs/07 — file with the application
5 Notarized owner signatures	docs/07 — two ownership groups
6 Letter of Intent	docs/03 — states the voluntary conditions offered
7 Legal Description (metes and bounds)	docs/05 — DRAFT; sealed RLS description governs
8 Site Plan	This drawing set; Sheet C-2.0 is the site plan proper
9 Boundary Survey	NOT INCLUDED — must be commissioned (Georgia RLS)
10 List of Adjoining Property Owners	docs/06 — re-pull on the filing date
11 Architectural Renderings and Elevations	docs/09 and Sheets A-1.1 to A-4.1

SHEET INDEX

20 of 24 sheets issued as of 2026-09-03. Built by listing drawings/*.svg at plot time — see general note 16.

SHEET	TITLE	SIZE / SCALE	STATUS	FILE (drawingsf...)	T/B
C-0.0	Cover Sheet, Sheet Index and Vicinity Map	ARCH D 36 x 24 · As noted	ISSUED	cover	=
C-1.0	Existing Conditions, Boundary and Topographic Survey	ARCH D 36 x 24 · 1" = 60'	ISSUED	existing-conditions	C-0
C-1.1	Demolition and Tree Protection Plan	ARCH D 36 x 24 · 1" = 60'	NOT ISSUED	--	--
C-2.0	Master Concept Plan - Overall	ARCH D 36 x 24 · 1" = 60'	ISSUED	mcp-sheet	=
C-2.1	Master Concept Plan - Enlargement, Block A	ARCH D 36 x 24 · 1" = 30'	ISSUED	mcp-enlargement-a	=
C-2.2	Master Concept Plan - Enlargement, Block B	ARCH D 36 x 24 · 1" = 30'	ISSUED	mcp-enlargement-b	=
C-2.3	Entry, Frontage and Amenity Enlargement	ARCH C 24 x 18 · 1" = 20'	ISSUED	entry-enlargement	=
C-2.4	Fallback Lot-Depth Exhibit - 50 x 82-ft Lots	ARCH D 36 x 24 · 1" = 60'	ISSUED	fallback-layout	=
C-3.0	Grading, Drainage and Stormwater Concept	ARCH D 36 x 24 · 1" = 60'	ISSUED	grading-drainage	=
C-3.1	Stormwater Details and Sections	ARCH C 24 x 18 · As noted	NOT ISSUED	--	--
C-4.0	Utility and Phasing Concept	ARCH D 36 x 24 · 1" = 60'	ISSUED	utility-phasing	=
C-4.1	Sanitary Sewer Profiles	ARCH D 36 x 24 · 1" = 50' H / 5' V	NOT ISSUED	--	--
C-5.0	Private Lane Plan and Profile	ARCH D 36 x 24 · 1" = 50' H / 5' V	NOT ISSUED	--	--
C-6.0	Phasing, Block and Open Space Exhibit	ARCH D 36 x 24 · 1" = 60'	ISSUED	phasing-openspace	=
C-7.0	Landscape, Buffer and Tree Protection Concept	ARCH D 36 x 24 · 1" = 60'	ISSUED	landscape-buffer	=
C-8.0	Civil Details	ARCH D 36 x 24 · As noted	ISSUED	civil-details	=
A-1.1	Plan A "The Springbrook" - Floor Plan	ARCH C 24 x 18 · 3/16" = 1'-0"	ISSUED	plan-a-sheet	A-1
A-1.2	Plan B "The Laurel" - Floor Plan	ARCH C 24 x 18 · 3/16" = 1'-0"	ISSUED	plan-b-sheet	A-2
A-2.1	Plan A - Exterior Elevations (four sides)	ARCH C 24 x 18 · 3/16" = 1'-0"	ISSUED	plan-a-elev	=
A-2.2	Plan B - Exterior Elevations (four sides)	ARCH C 24 x 18 · 3/16" = 1'-0"	ISSUED	plan-b-elev	=
A-2.3	Exterior Colour Schemes and Materials	ARCH C 24 x 18 · 3/16" = 1'-0"	ISSUED	plan-colors	=
A-3.0	Clubhouse, Mail Kiosk and Entry Monument Sign	ARCH C 24 x 18 · As noted	ISSUED	amenity-sheet	A-3
A-4.0	Typical Lot - Plan A	ARCH C 18 x 24 (portrait) · 1" = 10'	ISSUED	plan-a-lot	--
A-4.1	Typical Lot - Plan B	ARCH C 18 x 24 (portrait) · 1" = 10'	ISSUED	plan-b-lot	--

T/B is the sheet number printed in that sheet's own title block: "-" matches this index, "--" means the sheet declares none, and any other value is a provisional number to be corrected at the next issue (general note 16).

ALSO IN drawings/ — EXHIBITS, NOT SHEETS OF THIS SET

FILE	WHAT IT IS
mcp-web.svg	Master concept plan, screen version — public web exhibit, not a plot sheet
plan-a.svg	Plan A floor plan, tight crop — working exhibit for docs/09 and the web page
plan-b.svg	Plan B floor plan, tight crop — working exhibit for docs/09 and the web page

SEAL BLOCKS

Blank on purpose: no Georgia RLS, PE, architect or landscape architect is yet engaged, and no sheet in this set is sealed

GEORGIA REGISTERED LAND SURVEYOR	
SEAL (BLANK)	Boundary survey plat, metes-and-bounds legal description and topographic survey — Ord. 2023-603 §1003-4.3 and §1003-4.4, Checklist §1.e.2, Sheet C-1.0.
NOT YET ENGAGED — NO SHEET IN THIS SET IS SEALED.	
SIGNATURE	DATE

GEORGIA REGISTERED PROFESSIONAL ENGINEER	
SEAL (BLANK)	Grading, drainage, certified stormwater report, sewer, water, private street design and retaining walls — Checklist §1.e.7-9, §8.a, §11.a, Sheets C-3.0 to C-5.0 and C-8.0.
NOT YET ENGAGED — NO SHEET IN THIS SET IS SEALED.	
SIGNATURE	DATE


GEORGIA REGISTERED ARCHITECT	
SEAL (BLANK)	Dwelling and clubhouse plans and elevations — 2026 Application Instructions Item (11), Sheets A-1.1 to A-4.1.
NOT YET ENGAGED — NO SHEET IN THIS SET IS SEALED.	
SIGNATURE	DATE

GA REGISTERED LANDSCAPE ARCHITECT / FORESTER / ARBORIST	
SEAL (BLANK)	Buffer and landscape plan, tree protection and preservation — Checklist §1.e.10 and §6.a, Sheets C-1.1 and C-7.0.
NOT YET ENGAGED — NO SHEET IN THIS SET IS SEALED.	
SIGNATURE	DATE

Final plan sets must be sealed, signed and dated across the seal by the licensed registered party responsible for the contents of each sheet (Georgia Board Rule 180-12-.02; Checklist §1.e).

VICINITY MAP SCALE 1" = 400'


Arcado Rd, Killian Hill Rd, Arcadia Pl, the three adjoining subdivisions and the Ride Gwinnett Route 25 stop

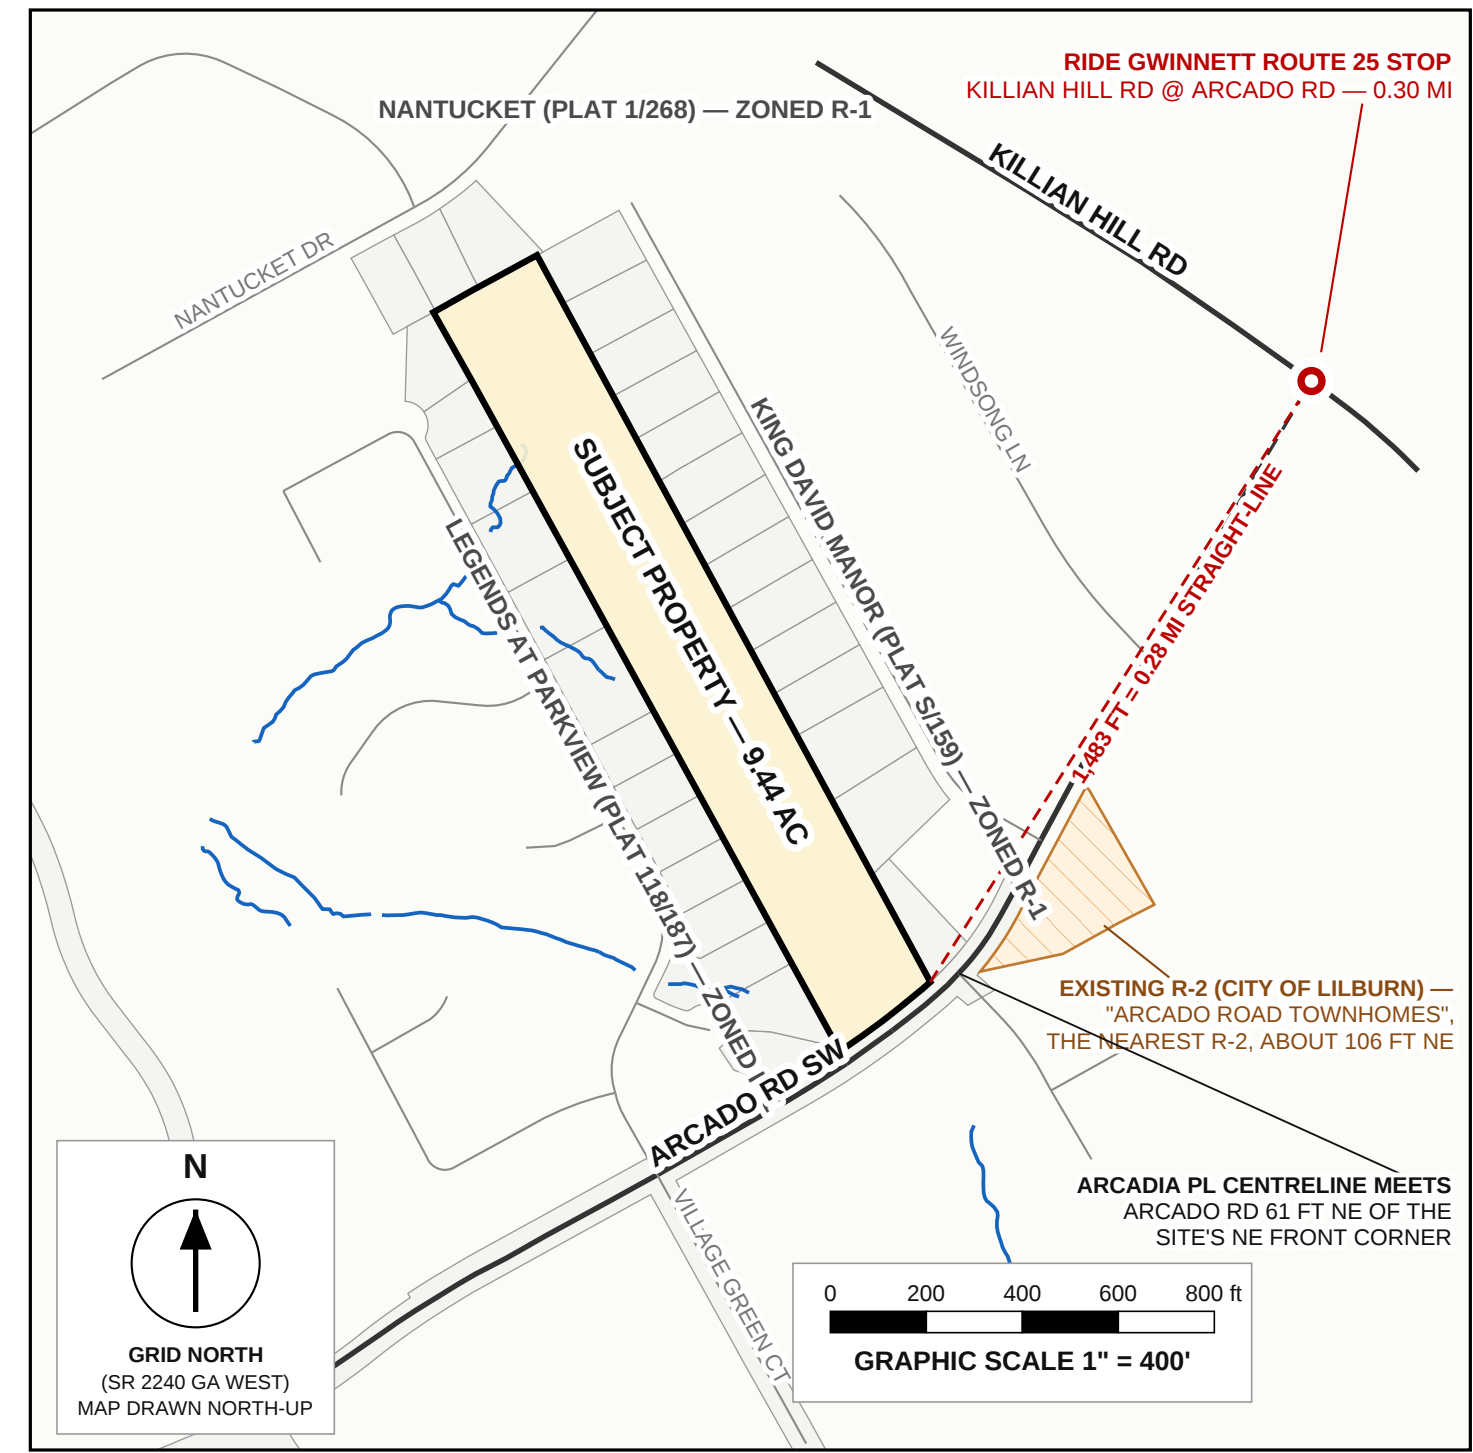

Drawn north-up from the Gwinnett County GIS street centrelines, tax-parcel fabric, zoning polygons and hydrology carried in data/site-context-local.json and from the boundary ring in data/layout.json. Adjoining parcels are the 31 abutters plus the Arcado Rd right-of-way. Route 25 runs Gwinnett Place Transit Center to Stone Mountain; weekday headway about 50 minutes, Saturday hourly, no Sunday service. Neither centreline is mapped through the Killian Hill Rd / Arcado Rd intersection, so the intersection is shown where the mapped Arcado Rd centreline, produced on its last mapped bearing, cuts the mapped Killian Hill Rd centreline: it scales 1,483 ft (0.28 mi) against the 0.30-mi straight-line distance to stops 2528 and 2578 in the GTFS feed. Not a survey.

LOCATION MAP SCALE 1" = 1,000'

The site in the City of Lilburn zoning pattern, with distance rings on the site centroid

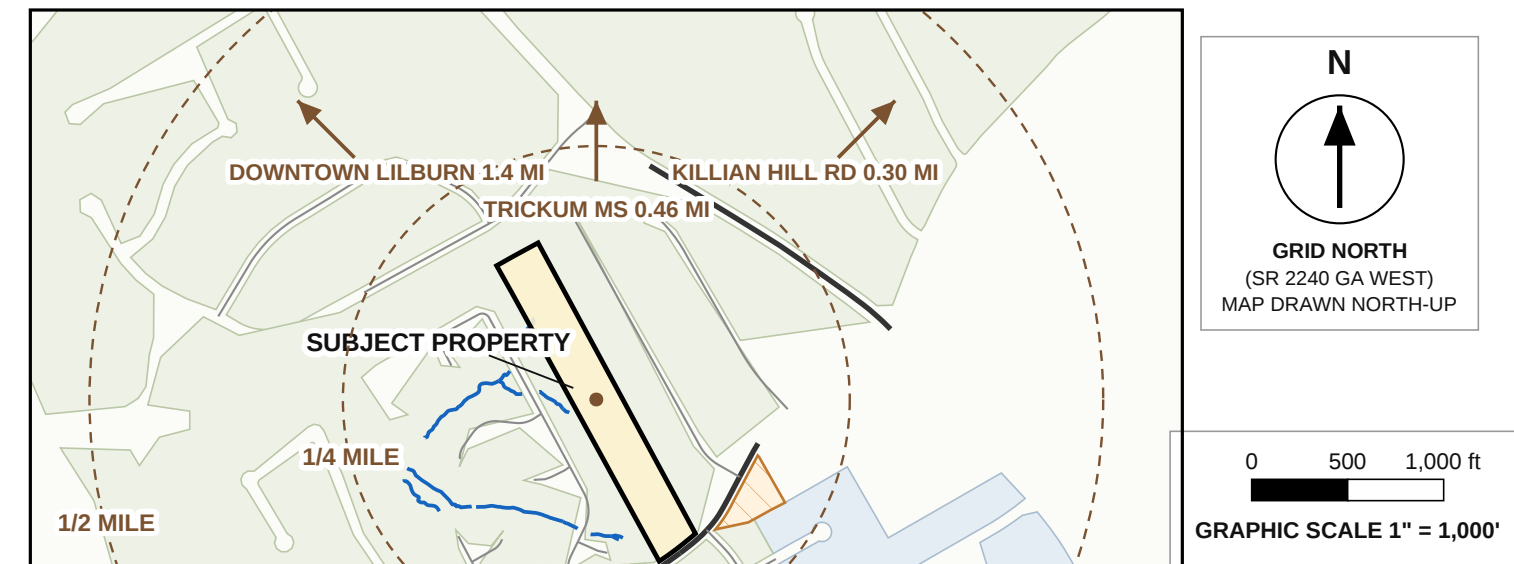

Zoning polygons and jurisdiction from the Gwinnett County GIS zoning layer; the R-1 (Lilburn) and R-100 (unincorporated Gwinnett) fills show the city limit. Off-map destinations are straight-line distances from docs/11 §6.3 and their compass directions are approximate.

LEGEND — VICINITY AND LOCATION MAPS

- Subject property — the 9.44-ac assemblage to be rezoned R-1 → R-2
- Adjoining tax parcel (Gwinnett GIS) — vicinity map
- Street centreline (Gwinnett GIS)
- Arcado Rd SW / Killian Hill Rd — county collectors
- Centreline produced — not mapped in the source data
- Stream — state waters (top of bank approximate)
- Ride Gwinnett Route 25 bus stop (GTFS feed 2026-07-02)
- Straight-line distance from the site
- Existing R-2 zoning, City of Lilburn — nearest R-2 precedent
- Existing R-1 zoning, City of Lilburn — location map
- R-100 zoning, unincorporated Gwinnett — location map
- Distance ring from the site, 1/4 and 1/2 mile — location map
- Direction and straight-line distance to an off-map destination

REVISIONS

NO.	DATE	DESCRIPTION	BY
0	2026-09-03	Issued for pre-application review — DRAFT, not sealed	M.A.

GENERAL NOTES

Notes the City of Lilburn Site Development Plan Review Checklist requires on the cover page are reproduced verbatim and identified as such

1. STATUS AND SEALS. This set is owner-prepared from public records for pre-application review and the rezoning hearing. DRAFT — NOT SEALED: no sheet is sealed by a Georgia registered land surveyor, professional engineer, architect or landscape architect, and the seal blocks are blank because none is yet engaged. Every statement of conformity reads "appears consistent with"; none is a certification of compliance. Final plan sets must be sealed, signed and dated across the seal by the licensed registered party responsible for the contents of the sheet (Georgia Board Rule 180-12-.02; Checklist §1.e).

2. APPROVAL NOTES — required on the cover by Checklist §4.a, verbatim: "APPROVAL OF THESE PLANS DOES NOT RELIEVE THE OWNER, DEVELOPER, AND/OR CONTRACTOR FROM COMPLYING WITH ALL APPLICABLE RULES, REGULATIONS, AND ORDINANCES." "DEVELOPER TO PROVIDE TO CITY CERTIFIED DETENTION POST-CONSTRUCTION (RECORD) DRAWINGS WITH THE SUBMITTAL OF THE FINAL PLAT OR ONE WEEK PRIOR TO REQUESTING A CERTIFICATE OF OCCUPANCY, SO THAT THE POST-CONSTRUCTION CONDITIONS MAY BE VERIFIED AND APPROVED. CERTIFIED RECORD DRAWINGS SHALL INCLUDE TOPOGRAPHY OF POND AND OUTLET STRUCTURE DETAIL USING POST-CONSTRUCTION SURVEY DATA. USING RECORD DRAWINGS, PROVIDE A CERTIFIED HYDROLOGY REPORT VERIFYING POND VOLUMES AND PEAK OUTFLOWS FROM REGULATED STORM EVENTS."

3. ZONING HISTORY AND CONDITIONS (Checklist §1.a, §4.b). THERE ARE NO ZONING CONDITIONS ON THIS PROPERTY. Zoning case no. RZ-2026-_____ (assigned by the City); date of approval _____; conditions _____. No special use permit, Zoning Board of Appeals variance or administrative variance is of record on any of the four parcels, and no overlay district applies. The only prior case is RZ-2025-01, a mixed-use request for 104 condominium units on this assemblage, which the Planning Commission TABLED on 2025-08-28 on a defective legal advertisement. It was never heard on its merits and never denied, so the twelve-month bar of §1003-11 does not appear to apply — confirm the file status with the Planning Director.

4. FLOODPLAIN (Checklist §9 Floodplain a, b). The property lies wholly in FEMA Zone X (area of minimal flood hazard), FIRM panel 13135C0114F, effective 2006-09-29 (FEMA National Flood Hazard Survey, Gwinnett GIS). NO SPECIAL FLOOD HAZARD AREA, FLOODWAY OR BASE FLOOD ELEVATION IS MAPPED ON THIS PROPERTY and no development is proposed in a floodplain. The Gwinnett future-conditions floodplain (www.gwinnettfoodplain.com) shall be checked before the Land Disturbance Permit; where one exists, finished floors shall be at least 1 ft above the future-conditions elevation and 3 ft above the 100-year base flood elevation (§9 Floodplain f). Lilburn Code Ch. 109 Art. III governs.

5. WETLANDS (Checklist §9 Wetlands a, b). No wetland is mapped on the property by the U.S. Fish and Wildlife Service National Wetlands Inventory. A field survey of any waters of the United States shall be made with the boundary and topographic survey; any delineation shall state its source and carry U.S. Army Corps of Engineers approval, and it is the owner's responsibility to obtain any Corps permit required.

6. STREAM BUFFERS — required by Checklist §9 Buffered State Waters e and f, verbatim: "STREAM BUFFERS ARE TO REMAIN IN A NATURAL AND UNDISTURBED CONDITION." "STREAM BUFFER SHALL BE STAKED AND PROTECTED PRIOR TO LAND DISTURBANCE." "An unnamed order-0 headwater of Jackson Creek (GAR030701030315; Georgia 2024 §303(d) list) reaches about 30 ft inside the SW property line and ends on the property. The 25-ft state buffer (O.C.G.A. §12-7-6(b)(15)), the 50-ft undisturbed buffer and the 75-ft impervious setback (Lilburn Code Ch. 109 Art. VII) are labelled on Sheets C-1.0, C-2.0 and C-2.2 from the top of bank. TOP OF BANK IS APPROXIMATE: the state waters shall be field-located and both banks delineated by a qualified professional, and that delineation governs. No buffer variance is requested with this rezoning.

7. SIGNS (Checklist §4.q). One monument entry sign not over 32 SF is proposed at the Arcado Rd entrance; its location, size and sight-triangle clearance are on Sheets C-2.3 and A-3.0. NO WALL SIGNS ARE PROPOSED ON ANY DWELLING OR ON THE CLUBHOUSE. ALL SIGNS SHALL BE PERMITTED SEPARATELY. A sign easement may be required.

8. MAIL DELIVERY (Checklist §4.r). Mail will be delivered to a cluster bus unit (CBU) kiosk in the amenity tract inside the entrance, with protection from the elements, an accessible route and four short-term spaces; detailed on Sheet A-3.0. THE LILBURN POST OFFICE GROWTH MANAGER SHALL BE CONTACTED FOR MAIL DELIVERY AND MAILBOX REQUIREMENTS. A cluster mailbox system may be required for the entire project and one street name may serve to assign all house numbers.

9. GRADING — required by Checklist §10.a on the grading plan and on all soil-erosion, sedimentation and pollution-control sheets, verbatim:

"MAXIMUM CUT OR FILL SLOPES IS 2H:1V" "CITY OF LILBURN/GWINNETT COUNTY ASSUMES NO RESPONSIBILITY FOR OVERFLOW OR EROSION OF NATURAL OR ARTIFICIAL DRAINS BEYOND THE EXTENT OF THE STREET RIGHT-OF-WAY, OR FOR THE EXTENSION OF CULVERTS BEYOND THE POINT SHOWN ON THE APPROVED AND RECORDED PLAN. THE CITY OF LILBURN/GWINNETT COUNTY DOES NOT ASSUME THE RESPONSIBILITY FOR THE MAINTENANCE OF PIPES IN DRAINAGE EASEMENTS BEYOND THE CITY/COUNTY RIGHT-OF-WAY." "STRUCTURES ARE NOT ALLOWED IN DRAINAGE EASEMENTS."

10. STREET GRADES. Maximum street grade 12%; grades of 12% to 15% require an "As Graded" survey before installation of the curb (Checklist §7.k). Existing ground on the lane alignment reaches 10.9% — see Sheet C-5.0.

11. UTILITIES (Checklist §4.d). Gwinnett County Department of Water Resources provides water and sanitary sewer only; electric, gas and telecommunication service is by the respective private providers, and new electric distribution within the development will be underground. PHASE 1 connects by gravity to the existing 8-in sewer already crossing this property (manhole invert 927.13) and needs no extension. PHASE 2 needs an off-site gravity extension of about 178 ft to the Legends at Parkview MS 8-in main at invert 919.58. A private pump station, force main or gravity sewer is NOT available: Gwinnett DWR's Standard Policy for Private Developments (Condominiums, Townhomes and Subdivisions, rev. 9/2018) allows private facilities "only ... for commercial properties under single ownership within a development", and a county station fails WSP-24 §1.3.1(A) because gravity is 1.78 ft away, not "more than 5,000 feet down gradient". A DVR sewer capacity certification is required. See Sheets C-4.0 and C-4.1.

12. FIRE ACCESS. One private lane about 1,754 ft long, dead-ended at the NW terminus, 22 ft of clear pavement, no parking, hammerhead turnarounds. SPECIAL APPROVAL OF A DEAD-END FIRE APPARATUS ACCESS ROAD OVER 750 FT IS REQUESTED under ICF 2024 (CA) Appendix D103.4, Table D103.4. Two access roads are NOT required: Ga. Comp. R. & Regs. 120-3-3-.04 replaces Appendix D107.1 and sets the trigger above 120 dwelling units, and 41 are proposed. NFPA 13D sprinklers in every dwelling are offered VOLUNTARILY and are not a code requirement. Codes: the Georgia State Minimum Standard Codes effective 1 January 2026 (2024 IRC / IBC / IFC / IPC / IMC / IFGC with the 2026 Georgia Amendments; 2023 NEC; 2015 IECC as amended).

13. OPEN SPACE AND RECREATION AREAS. Development Regulations §5.9.1 requires recreation land in single-family detached subdivisions "having a gross area of 50 acres or more". At 9.44 acres this development is below that threshold and §5.9 does not apply; the 33.8% of common open space shown is voluntary.

14. BUFFERS AND THE §313(1) READING. The 20-ft undisturbed buffer required abutting R-1 (Table 4.1, allowed dwelling types other than detached single-family) is held within the lots as a recorded buffer easement in reliance on §313(1), "Buffer requirements ... supersede these minimum required yards". THIS READING IS TO BE CONFIRMED WITH THE PLANNING DIRECTOR; Sheet C-2.4 carries the fallback layout, 50 x 82-ft lots with the buffer in a separate common tract, if a separate tract is required.

15. DIMENSIONS, DATUM AND COORDINATES. All dimensions are in US survey feet. Horizontal datum Georgia State Plane West Zone (SR 2240), NAD83, vertical NAVD88. Sheets C-1.0 to C-6.0 are drawn in a site-local system (+u along the strip on a bearing of N 28°43' W from the Arcado Rd RW corner at 2,310,931.00 E / 1,411,431.50 N; +v across the strip toward the NE line). THE TWO MAPS ON THIS SHEET ARE DRAWN NORTH-UP. Boundary geometry is Gwinnett GIS and is DRAFT; topography is USGS 3DEP and is approximate. THE SEALED SURVEY GOVERNS.

16. SHEET INDEX INTEGRITY. The sheet index is generated at plot time by listing the files present in the package drawings/ directory and matching them against the sheet table in tools/cover.py — the same table tools/transmittal.py uses for the filing transmittal. A row marked NOT ISSUED is not in this set and must not be relied on. Where the "T/B" column shows a number, that sheet's own title block still carries a provisional number from an earlier numbering; THE NUMBER IN THIS INDEX GOVERNS and the sheet will be renumbered at the next issue.

17. SCALES AND LETTERING. A graphic scale and a north arrow are shown on each map here and on every applicable sheet (Checklist §4.h); engineering scales on the C-sheets, architectural on the A-sheets. DO NOT SCALE A REDUCED PRINT — use the graphic scale. Lettering on this sheet is 10.5 pt in the general notes, 8.5 to 11 pt in the tables, legend and map annotation, and 7 to 8 pt in the title block and map furniture — a cap height of 0.068 to 0.107 in at full size. The set standard is a 1/8-in cap height; the content this checklist requires on a cover page does not fit an ARCH D sheet at that size, so this sheet carries the largest type that fits.

18. BASIS AND SOURCES. Gwinnett County GIS — parcels, zoning, streets, right-of-way, sewer, water, hydrology, floodplain, soils, queried 2026-08-28; Gwinnett Tax Assessor 2026 property-ownership file; USGS 3DEP; FEMA NFHL; Ride Gwinnett GTFS feed 2026-07-02; City of Lilburn Zoning Ordinance 2023-603, 2026 Application Instructions, Site Development Plan Review Checklist, 2024 Comprehensive Plan and the 2026 Comprehensive Plan Amendment (transmitted to DCA 2026-07-13; adoption pending as of 2026-09-03). Package files FACTS.md, data/layout.json and data/plans.json, all read at plot time.

Disclaimer: This is an AI-generated analysis for preliminary planning purposes. All findings must be verified by a licensed professional before use in design, permitting, or regulatory submissions.

Label: DRAFT / NOT SEALED — every item that must be sealed by a Georgia RLS, PE, architect or landscape architect is shown as a concept only. Statements of conformity read "appears consistent with".

THE COTTAGES AT ARCADE SPRINGS

COVER SHEET, SHEET INDEX AND VICINITY MAP — Rezoning R-1 → R-2 (City of Lilburn, Georgia)

4535 / 4537 / 4539 / 4541 Arcado Rd SW, Lilburn, GA 30047 — Land Lot 123, 6th District, Gwinnett County — PINs R6123 033, 015, 014, 162 — 9.44 ac (deeded)

Cover page per City of Lilburn Site Development Plan Review Checklist §1.e.1, §4.a and §4.b; sheet index generated from drawings/ at plot time

APPLICANT / OWNER
Mohammed Awad
4541 Arcado Rd SW, Lilburn GA 30047-3968 (parcels 033, 015); Mendez / Roblero de Leon (parcels 014, 162) — co-applicants, owner signatures required
PREPARED FOR
Pre-application conference, City of Lilburn Planning & Zoning (340 Main St) — rezoning application per Ord. 2023-603 §1003 (2026 Application Instructions)

STATUS
DRAFT — NOT SEALED
Owner-prepared cover page for pre-application review. No sheet in this set is sealed; the seal blocks are blank because no Georgia RLS, PE, architect or landscape architect is yet engaged. To be superseded by sealed survey, civil, architectural and landscape drawings.
Generator: tools/cover.py (on tools/sitebase.py)

DATE	2026-09-03
SCALE	As noted — see each map
DATUM	SR 2240 GA WEST US-ft; NAVD88
DRAWN	owner-prepared (AI-assisted)
CHECKED	RLS / PE — pending

SHEET
C-0.0
COVER SHEET, SHEET INDEX AND VICINITY MAP