


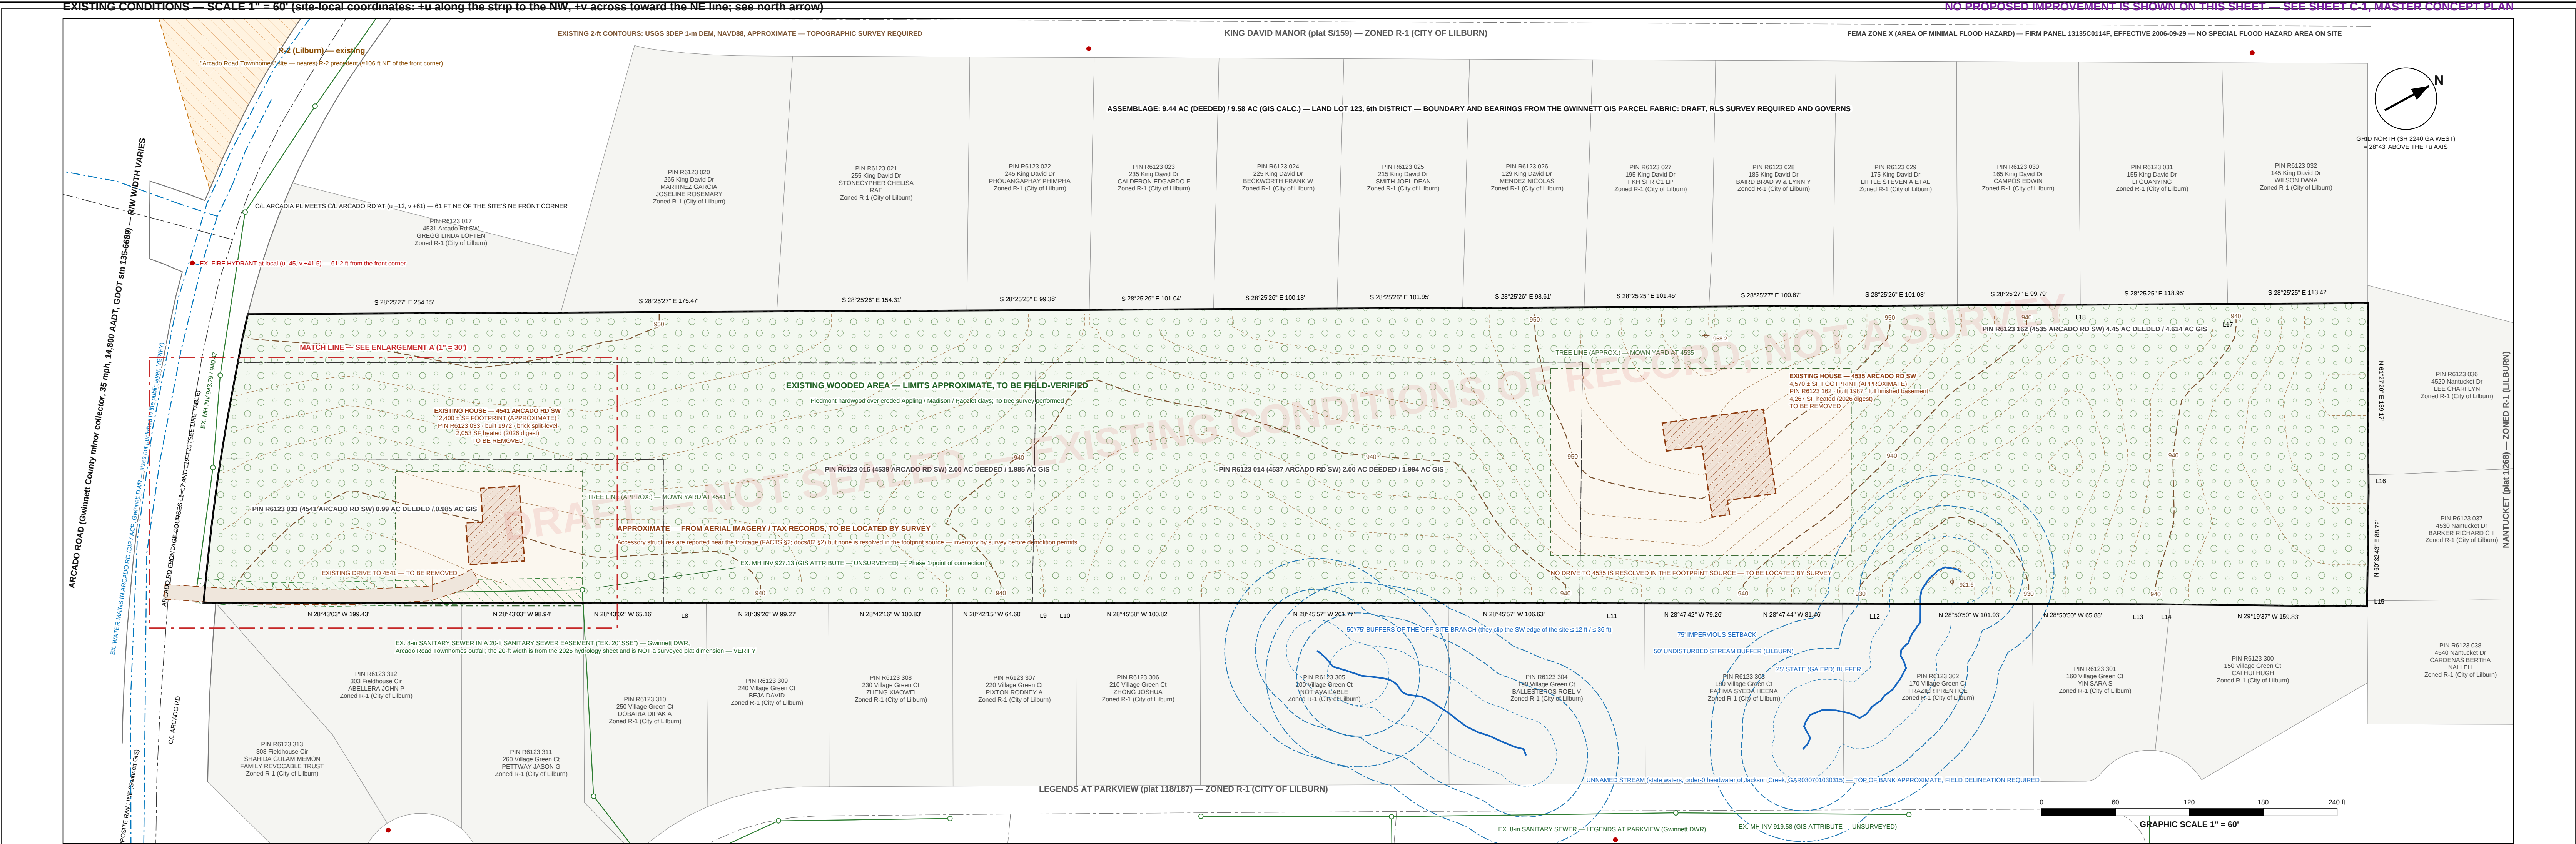

EXISTING SITE DATA — compiled from public records on 2026-09-03

EXISTING SITE DATA	RECORD VALUE (DRAFT — SURVEY GOVERNS)	SOURCE
Address (PINs)	4535, 4537, 4539, 4541 Arcado Rd SW, Lilburn GA 30047 — R6123 162, 014, 015, 033	Gwinnett 2026 digest
Land lot / district	Land lot 123, 6th District, Gwinnett County, City of Lilburn tax district	Gwinnett GIS
Area	9.44 ac (deeded (411,206 SF) = 0.99 ± 2.00 ± 2.00 ± 4.45; 9,577 ac (417,174 SF) GIS-calculated; RLS survey governs	2026 digest / GIS ring
Boundary lengths	Arcado Rd frontage 237.63' SW line 1797.01' NE line 1721.69' rear line 246.41' perimeter 3962.73'	Aerial imagery / 2026 digest
Width across the strip	224.7 ft at Arcado Rd, 246.4 ft at the NW end (measured NE line to SW line)	OSMIML footprints — APPROX.
Existing zoning	R-1, City of Lilburn (all four parcels). Adjoining: R-1 Lilburn on every line, nearest R-2 = 106 ft NE; unincorporated Gwinnett R-100 ± 314 ft	GIS ring
Existing use	Two single-family dwellings with drives near the frontage and at mid-strip, the balance wooded. No commercial or agricultural use.	Gwinnett GIS DRAFT
Existing structures	4541: 2,400 ± SF footprint at (u 203, v -174), built 1972, 2,063 SF heated, 4535: 4,570 ± SF footprint at (u 1202 ± 130, v 180), built 1987, 4,267 SF heated, area ± 250 ft long × 12 ft, all to be removed.	Aerial imagery / 2026 digest
Topography	Range 921.6 — 968.2 ft NAVD88; ridge 958.2 ft at (u 1184, v -18); low 921.6 ft at (u 1384, v -218); cross-slope falls NE — SW; contour interval 2 ft	OSMIML footprints — APPROX.
Floodplain	Zone 1 (area of minimal flood hazard) — FIRM panel 13135C0114F, effective 2006-09-29 — no SFHA, floodway or BFE on site.	USGS 3DEP 1-m DEM (approx.)
Stream / buffers	One unnamed order-0 headwater (state waters) reaching ± 30 ft inside the SW line; 25' GA EPD / 50' undisturbed / 75' impervious setback shown from approximate top of bank.	Stream — state waters (top of bank approx.)
Sanitary sewer	Existing 8-in gravity main in a 20-ft easement inside the SW line, u = -42 to 272; 24" MH invert 927.13 on site and 919.58 off site (Legends at Parkview) — GIS attributes, unsurveyed	25' state (GA EPD) buffer
Water	DIP / ACP mains in Arcado Rd 47–107 ft from the front line; nearest hydrant 61.2 ft from the front corner at (u -45, v +41.5)	50' undisturbed stream buffer (Lilburn)
Right-of-way	Arcado Rd, Gwinnett County minor collector, 35 mph, 14,800 AADT, RW WIDTH VARIES; 64.9 ft at v -40, 60.0 ft at v -120; 60.2 ft at v -200, 69.9 ft at v -235 — scaled perpendicular to the two GIS RW lines, not surveyed	75' impervious setback
Soils	AptR (Appling), AmC2 (Appling/Madison), PkC2 (Pacott), GbE2 (Cecil), GbE2 (Cecil, steep), ARE (Ashlar — gneiss at 22–40 in), HYB (Helena — HSG D)	USGS 3DEP 1-m DEM (approx.)
Vegetation	Existing wooded area over the balance of the site; limits approximate, no tree survey performed	Existing 8-in sanitary sewer + manhole
Adjoining owners	31 private tax parcels (24 NE, 14 SW, 3 NW) in the Gwinnett County right-of-way ± 32 notice recipients; PIN, owner and R-1 zoning labelled on the plan	Existing 20' sanitary sewer easement (VERIFY)

Existing building footprints and the 4541 drive: © OpenStreetMap contributors (ODM), ways 999395123 / 999395265 / 913015145 — aerial imagery footprints, approximate. Owner names and mailing addresses: Gwinnett County Tax Assessor 2026 property ownership file. Zoning: Gwinnett GIS zoning layer (City of Lilburn districts).

EXISTING SANITARY SEWER SCHEDULE — every value is a Gwinnett DWR GIS attribute, UNSURVEYED (an invert survey is required)

FACILITY ID	FROM (u, v) — TO (u, v)	SIZE / MAT.	LENGTH (ft)	SLOPE (in)	INVERT IN — OUT (ft)	PROJECT
3425385	(-2, -157) — (-28, -20)	8-in DIP	134.0	3.59	946.90 — 945.99	Arcado Road Townhomes sewer outfall
3425386	(-22, -50) — (-28, -125)	8-in DIP	75.1	4.42	943.79 — 940.47	Arcado Road Townhomes sewer outfall
3425387	(-28, -125) — (-42, -224)	8-in DIP	100.8	7.30	940.25 — 932.89	Arcado Road Townhomes sewer outfall
3425388	(-42, -224) — (-20, -229)	8-in DIP	62.1	3.98	932.69 — 930.84	Arcado Road Townhomes sewer outfall
3425389	(-20, -229) — (-272, -224)	8-in PVC	251.6	1.40	930.64 — 927.13	Arcado Road Townhomes sewer outfall
3425390	(-272, -224) — (-281, -392)	8-in PVC	167.9	1.05	926.93 — 925.17	Arcado Road Townhomes sewer outfall
2300318	(1340, -406) — (1146, -406)	8-in DIP	199.0	0.17	921.03 — 919.58	Legends At Parkview
2300316	(1160, -405) — (929, -405)	8-in DIP	231.2	0.67	919.38 — 917.83	Legends At Parkview

Slope is computed from the published invert pair and pipe length: (INV IN - INV OUT) / LENGTH. The 927.13 manhole is the Phase 1 point of connection; the 919.58 manhole is the Legends at Parkview tie-in studied in doc008 Memo B.

SOURCES AND ACCESS DATA

- Gwinnett County GIS — parcels, zoning, streets, right-of-way, sanitary sewer, water mains, hydrants, subdivisions, city limits (accolaslas, gwinnett, MapServer layers 2, 7, 21, 23, 25), streams, floodplain, soils (GISDataViewer/GC, Main layers 1, 2, 9), Quinet 2026-09-28.
- Gwinnett County Tax Assessor — 2026 Property Ownership quarterly file (owners, mailing addresses, deeded acreage, year built, heated area), Accessed 2026-09-28.
- USGS 3DEP elevation Imagery Server — 1-meter DEM sampled on a 100 × 50-ft grid, NAVD88 (data/pools/samples-json), Accessed 2026-09-28.
- FEMA National Flood Hazard Layer — flood zone and FIRM panel (doc011 S2), Accessed 2026-09-28.
- OpenStreetMap (© OpenStreetMap contributors, ODM) — aerial imagery building footprints and the 4541 drive, ways 999395123, 999395265, 913015145; Microsoft Bing ML Building Footprints Image, Accessed 2026-09-03.
- Public aerial imagery — visual check of the footprints and of the town-yard (tree-line) limits, 2026-09-03. Imagery is not reproduced on this sheet.
- City of Lilburn Zoning Ordinance 2023-603 §1003-4.6 (site-plan content) and the City of Lilburn Site Development Plan Review Checklist, FACTS.md §1, §2, §2b, doc005 §5, doc006, doc011 §2.

LEGEND


- Assemblage boundary (Gwinnett GIS — DRAFT)
- Interior parcel line (to be combined)
- Adjoining tax parcel (all zoned R-1, Lilburn)
- Arcado Rd right-of-way line (RW width varies)
- Existing road centerline
- Existing index contour, 10 ft (3DEP approx.)
- Existing contour, 2 ft (3DEP approx.)
- Stream — state waters (top of bank approx.)
- 25' state (GA EPD) buffer
- 50' undisturbed stream buffer (Lilburn)
- 75' impervious setback
- Existing 8-in sanitary sewer + manhole
- Existing 20' sanitary sewer easement (VERIFY)
- Existing water main (Gwinnett DWR)
- Existing fire hydrant
- Existing building — approximate, to be removed
- Existing drive — approximate, to be removed
- Existing wooded area (limits approximate)
- Tree line at mean year (approximate)
- Existing R-2 zoning (City of Lilburn)
- Match line — enlargement at 1" = 30'

LINE TABLE — courses under 60 ft (GIS-derived, DRAFT)

LINE	BEARING (SR 2240 GA WEST)	DISTANCE
L1	S 92°37'51" W	12.82
L2	S 53°31'16" W	22.08
L3	S 54°09'44" W	22.20
L4	S 54°51'18" W	21.98
L5	S 55°12'22" W	22.19
L6	S 55°42'53" W	16.64
L7	N 28°43'02" W	30.04
L8	N 28°50'12" W	34.90
L9	N 28°50'12" W	17.92
L10	N 28°45'55" W	17.59
L11	N 28°47'42" W	52.82
L12	N 28°47'42" W	52.20
L13	N 28°50'45" W	39.97
L14	N 29°19'57" W	6.80
L15	N 60°39'26" E	4.59
L16	N 61°35'48" E	13.93
L17	S 28°10'02" E	0.48
L18	S 28°50'02" E	0.75
L19	S 48°41'39" W	21.97
L20	S 50°35'58" W	38.12
L21	S 51°30'08" W	4.12
L22	S 50°41'21" W	22.30
L23	S 50°56'17" W	22.22
L24	S 51°41'48" W	21.96
L25	S 52°28'47" W	8.83

ENLARGEMENT A — ARCADO ROAD FRONTAGE, EXISTING HOUSE AT 4541 AND THE EXISTING SANITARY SEWER (SCALE 1" = 30')

Same data, same coordinates as the plan above, u -80 to 300, v -250 to -35. Frontage courses are tabulated in the line table at the left.

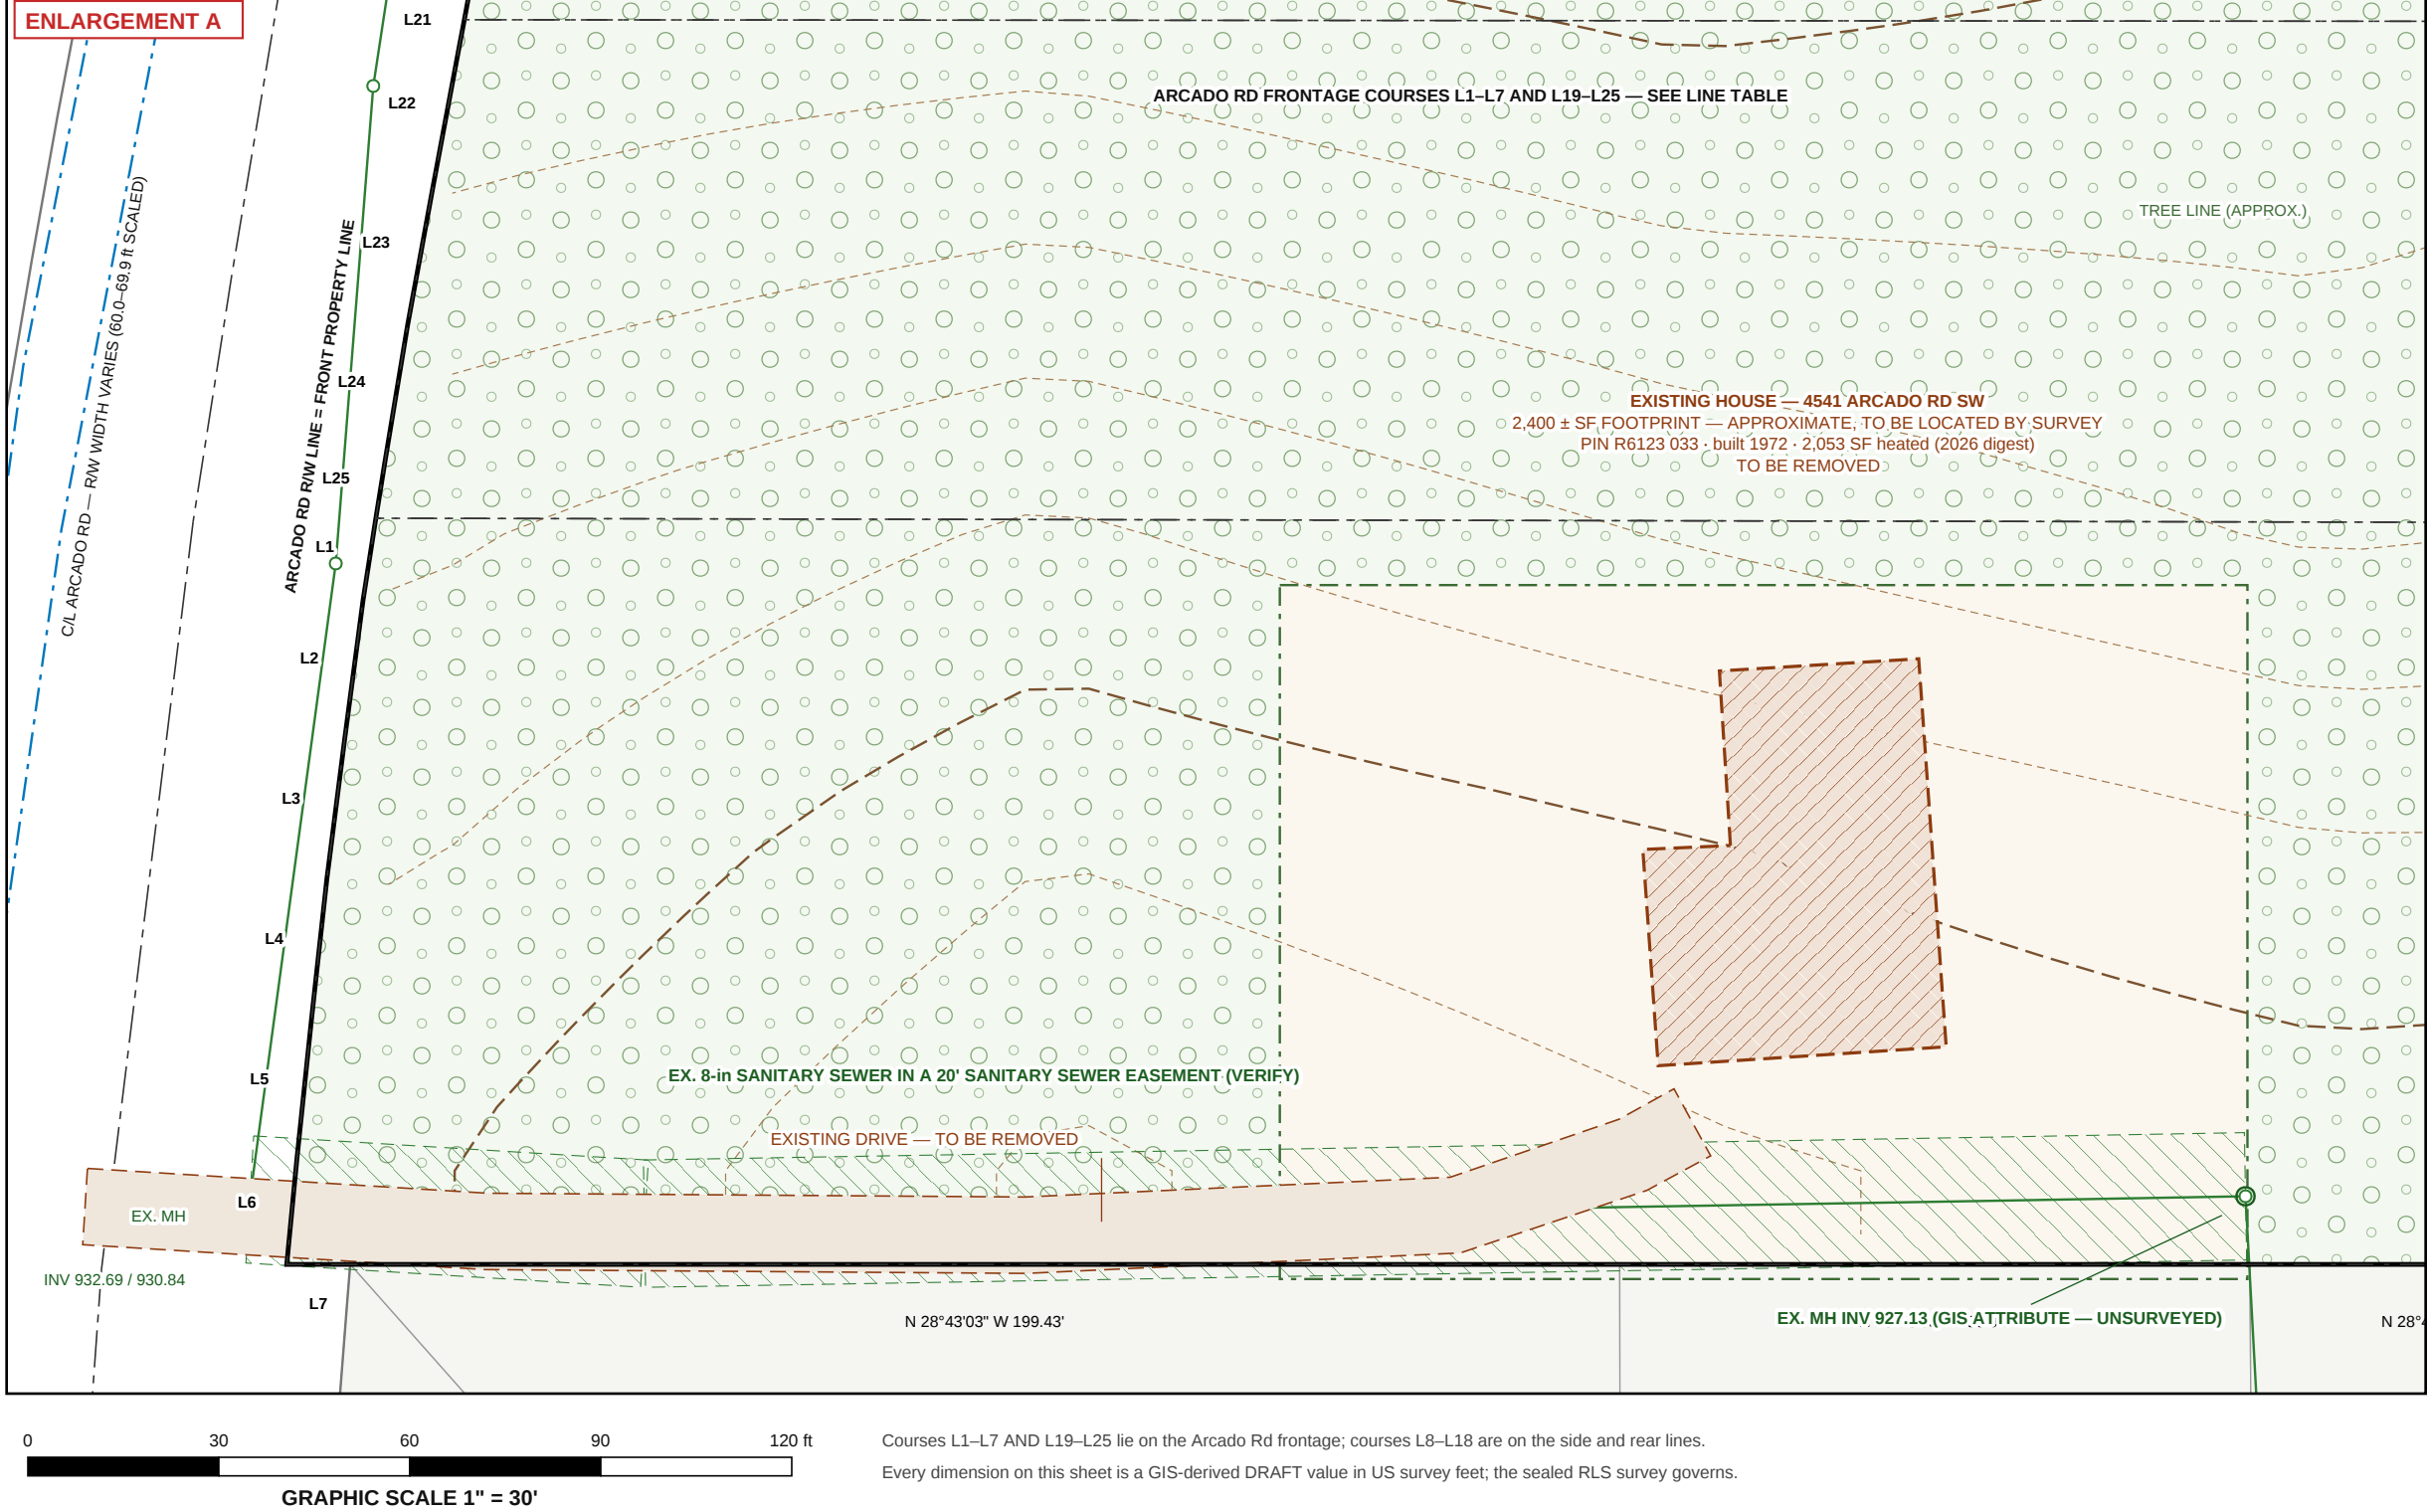

GENERAL NOTES — EXISTING CONDITIONS

- BOUNDARY AND PARCEL LINES: the assemblage boundary, the four interior parcel lines, the bearings, the distances and the acreages shown are computed from the Gwinnett GIS parcel fabric; SR 2240 GA West, US survey feet) and are DRAFT. A boundary survey plat and metes and bounds legal description sealed by a Georgia registered land surveyor are required by Lilburn Zoning Ordinance 2023-603 §1003-4.3 and §1003-4.4 and govern over this sheet. The four parcels are to be combined, the interior lines are shown so the City can read the assemblage.
- TOPOGRAPHY: existing 2-ft contours are interpolated from the USGS 3DEP 1-meter digital elevation model sampled on a 100 × 50-ft grid (NAVDS8) and are APPROXIMATE. Elevations on site range 921.6 to 968.2 ft; the high point is on the ridge at local u 1384, v -18 and the low point is in the rear pocket at (u 1384, v -218). A topographic survey is required before any engineering design. Contour interval 2 ft, index contours at 10 ft.
- EXISTING BUILDINGS AND DRIVES §1003-4.4 (existing buildings and structures): the two dwellings and the drive shown are APPROXIMATE — FROM AERIAL IMAGERY / TAX RECORDS, TO BE LOCATED BY SURVEY. Footprint outlines are public aerial imagery building footprints published by OpenStreetMap (© OpenStreetMap contributors, ODM), Microsoft Bing ML Building Footprints Image — ways 999395123, 999395265 and 913015145, transformed into the site-local system and checked against public aerial imagery on 2026-09-03. Footprint areas scale at 2,400 SF (4541) and 4,570 SF (4535) against 2026 digest heated areas of 2,063 SF (single level, built 1972) and 4,267 SF (built 1987, full finished basement). BOTH DWELLINGS, ALL ACCESSORY STRUCTURES AND ALL EXISTING DRIVES ARE TO BE REMOVED. Accessory structures are reported near the frontage (FACTS §2, doc002 §2) but none is resolved in the footprint source; inventory them by survey before demolition permits. The septic-sewer status of 4535 is unknown — VERIFY. NOTE THE POSITION OF 4535: its dwelling stands about 1,022 ft back from the Arcado Rd right-of-way, on the ridge at mid-strip — NOT at the frontage. FACTS §2 and doc002 §2, which place both houses "near the front", should be corrected to match this sheet.
- EXISTING VEGETATION §1003-4.6 (areas of existing vegetation): EXISTING WOODED AREA — LIMITS APPROXIMATE, TO BE FIELD-VERIFIED. The wooded limit is the site boundary less the two mean yards at the existing dwellings, digitized from public aerial imagery on 2026-09-03 and consistent with doc011 (the rear two-thirds is Piedmont hardwood) and FACTS §2 (wooded rear). NO TREE SURVEY HAS BEEN PERFORMED; species, diameter, species, species and the actual inside the SW line shown. A tree survey and tree protection / replacement plan will be submitted with the Land Disturbance Permit; tree density units at 15 TD/acre are not required of a single-family residential subdivision (City of Lilburn Site Development Plan Review Checklist §6.1).
- STREAM AND BUFFERS: an unnamed order-0 headwater of Jackson Creek (GA0307010303103; Georgia 2024 53036) list for bacteria and toxic, urban runoff reaches about 30 ft inside the SW line and terminates at local (u 1382, v -210). TOP OF BANK IS APPROXIMATE — a field delineation by a qualified professional is required and governs. Buffers shown: 25 ft state (GA EPD, O.C.G.A. §12-2-400(15)), 50 ft undisturbed and 25 ft additional impervious setback ± 75 ft total (City of Lilburn Code tit. 109 Art. VII). The 5075-ft buffers of a second branch that runs 38–58 ft outside the SW line clip the SW edge of the site.
- FLOODPLAIN, FEMA Zone X (area of minimal flood hazard) — FIRM panel 13135C0114F, effective 2006-09-29 (Gwinnett GIS floodplain layer; doc011 §3 Flood, FEMA NFHL, accessed 2026-09-28). No special flood hazard area, floodway or base flood elevation is mapped on the site; the headwater stream is not a FEMA-mapped watercourse, so the local stream buffer, not a BFE, governs the rear pocket.
- SANITARY SEWER: an existing 8-in gravity main (Arcado Road Townhomes sewer outfall) — Gwinnett DWR) enters the site at Arcado Rd and runs 7–13 ft inside the SW line to a manhole at local (u 272, v -224). Both invert elevations shown — 927.13 at that manhole and 919.58 at the Legends at Parkview manhole at (u 1349, v -407) — are GIS ATTRIBUTES, UNSURVEYED; an invert survey is the first field task. The 20-in sanitary sewer easement shown is the TX, 20' SISE of the 2025 hydrology sheet and is NOT a surveyed plat dimension — VERIFY the recorded width and holder. A Gwinnett DWR sewer capacity certification is required for any connection.
- WATER, DIP and ACP mains are in the Arcado Rd right-of-way 47–107 ft from the front line; the public utility does not publish diameters — VERIFY with Gwinnett DWR. The nearest fire hydrant is at local (u -45, v +41.5), 51.2 ft from the front corner. Other hydrants shown are in the adjoining subdivisions.
- ARCADO ROAD RIGHT-OF-WAY, RW WIDTH VARIES. Measured perpendicular between the two Gwinnett GIS right-of-way lines it scales 64.9 ft at v -40, 60.0 ft at v -120, 60.2 ft at v -200, 69.9 ft at v -235 — a GIS-scaled dimension, not a surveyed one; the RW line, its width and any required dedicated easement will be established by the RLS survey. Arcado Rd is a Gwinnett County-maintained minor collector, 35 mph, 14,800 AADT (GDOT station 125+688, 2017). The centerline of Arcado Place meets the Arcado Rd centerline at local (u -12, v +61), 61 ft NE of the site's NE front corner.
- SOILS §1003-4.5 (Soils §1003-4.5, via Gwinnett GIS), AptR (Appling), AmC2 (Appling/Madison), PkC2 (Pacott), GbE2 (Cecil), GbE2 (Cecil, steep), ARE (Ashlar — gneiss at 22–40 in), HYB (Helena — HSG D) is hydrologic soil group D with a seasonal high water table near 24 in; ARE (Ashlar) carries gas, telecommunication and storm-drainage structures are not published in the layers used for this sheet and are NOT shown. Utility locates through Georgia B11 (Georgia Utility Facility Protection Act, O.C.G.A. §25-9) are required before any field work, and a full testing-utility survey is required with the Land Disturbance Permit.
- STATUS: this sheet is a DRAFT record of existing conditions compiled from public data for pre-application review. It is NOT a survey and is NOT SEALED. All dimensions are US survey feet in the site-local system (u along the strip, v across). Every statement of conformity in this submittal reads "appears consistent with" and none is a compliance certification. THE SEALED SURVEY GOVERNS.

Disclaimer: This is an AI-generated analysis for preliminary planning purposes. All findings must be verified by a licensed professional before use in design, permitting, or regulatory submissions.

Label: DRAFT / NOT SEALED — every item that must be sealed by a Georgia RLS, PE, architect or landscape architect is shown as a concept only. Statements of conformity read "appears consistent with".

THE COTTAGES AT ARCADO SPRINGS

EXISTING CONDITIONS — Rezoning R-1 — R-2 (City of Lilburn, Georgia)

4535 / 4537 / 4539 / 4541 Arcado Rd SW, Lilburn, GA 30047 — Land Lot 123, 6th District, Gwinnett County — PINs R6123 033, 015, 014, 162 — 9.44 ac (deeded)

Existing conditions of record — Lilburn Zoning Ordinance 2023-603 §1003-4.6 (existing roads, streams, floodplain, buildings and structures, areas of existing vegetation)

APPLICANT / OWNER
Mohammed Awad
4541 Arcado Rd SW, Lilburn GA 30047-3968 (parcels 033, 015); Mendez / Roblero de Leon (parcels 014, 162) — co-applicants, owner signatures required

PREPARED FOR
Pre-application conference, City of Lilburn Planning & Zoning (340 Main St) — rezoning application per Ord. 2023-603 §1003 (2026 Application Instructions)

STATUS
DRAFT — NOT SEALED
Existing conditions compiled from public records for pre-application review. Boundary from Gwinnett GIS — RLS boundary survey required and governs. Topography USGS 3DEP (approximate). To be superseded by a sealed RLS boundary and topographic survey and PE civil design.
Generator: tools/sitebase.py + tools/existing_conditions.py

DATE
2026-09-03

SCALE
Scale 1" = 60' (ARCH D 36 × 24 in); enlargement 1" = 30'

DATUM
SR 2240 GA West US-ft; NAVD88

DRAWN
owner-prepared (AI-assisted)

CHECKED
RLS / PE — pending

SHEET
C-0
EXISTING CONDITIONS