


1. **SCALE AND MATCH LINE.** Enlargement of Sheet C-2.0 (1" = 30' on ARCH D 36 x 24 in, in the site-local system of Sheet C-0.0 (+u along the strip to the north-west from the Arcado Rd R/W corner, +v across toward the north-east line). C-2.1 = BLOCK A / PHASE 1, u = 40 to +1,000; C-2.2 = BLOCK B / PHASE 2, u 960 to 1,760. THE MATCH LINE AT u = 980 IS ALSO THE BLOCK LINE AND THE PHASE LINE AND FALLS ON LOT LINES, so the work can be platted in blocks (Checklist §4.i). See the key plan.
2. **DIMENSION BASIS.** Every dimension is computed at run time from data/layout.json; none is transcribed. US survey feet, architectural notation, measured to property lines and to the face of the element dimensioned. CONCEPT information on a Gwinnett County GIS boundary: a boundary survey plat and metes-and-bounds description sealed by a Georgia RLS (Ord. 2023-603 §1003-4.3, §1003-4.4) are required and GOVERN. Every statement of conformity reads "appears consistent with".
3. **LOTS AND BLOCKS** (Checklist §4.i). 41 lots — BLOCK A 24 (Phase 1), BLOCK B 17 (Phase 2). This sheet shows BLOCK A: 24 lots, 10 south-west and 14 north-east. Every lot is 50'-0" x 100'-0" = 5,000 SF and is dimensioned on the plan; designations read BLOCK-LOT. Table 4.1 (R-2) requires 3,000 SF, 50 ft width and 100 ft depth for a cottage home — the layout appears consistent with all three. Density 4.34 du/ac deeded (4.28 GIS) against the 8 du/ac maximum. The use is P in R-2 (§602 Use Table).
4. **SETBACK ENVELOPE** (Table 4.1 R-2; Checklist §4.j, §4.k). The dashed envelope on every lot is FRONT 15'-0" from the front lot line (= the lane tract line), SIDE 5'-0", REAR 20'-0". Houses sit inside it with margin: porch face 15'-8", side yard 6'-0" on both plans, rearmost element 20'-6" (Plan A patio) / 20'-10" (Plan B rear porch). Accessory buildings and ground equipment keep 5'-0" (Checklist §4.i). One lot of each row is dimensioned as TYPICAL; all lots are identical.
5. **PERIMETER BUFFER** (Table 4.1; §313(1); Checklist §4.j, §6.b). A 20'-0" UNDISTURBED buffer runs the entire south-west, north-east and north-west lines — every line abutting R-1 — and is dimensioned on the plan. Table 4.1 gives 0 ft for detached single-family in R-2 and 20 ft for "all other allowed dwelling types"; cottage homes are listed separately, so the plan is designed to 20 ft. The buffer lies in the rear 20 ft of each perimeter lot in a RECORDED BUFFER EASEMENT, on the reading that §313(1) lets a buffer supersede and coincide with the 20-ft rear yard. THIS SINGLE READING CARRIES THE LOT MODULE — CONFIRM IT AT THE PRE-APPLICATION CONFERENCE. Fallback (buffer in a separate tract, 50' x 82' lots, §1005 variance): Sheet C-2.4.
6. **GARAGES AND DRIVEWAYS** (Table 4.2 R-2 "A"; Checklist §4.p, §4.t, §7.i). Front-loaded garages are RECESSED 5'-0" BEHIND THE FRONT WALL as Table 4.2 requires; the porch projects a further 6'-0". The garage door stands 26'-8" from the front lot line, so the driveway holds two cars clear of the sidewalk. Driveways are 20'-0" x 26'-8", 4-in concrete on min. 4-in compacted GAB (asphalt alternate 2-in GDOT Type E or F on 4-in GAB, §7.i). 2 garage + 2 driveway spaces per dwelling = 164 on lot against Table 8.1's 2 per unit; the sidewalk crosses every apron with curb ramps to PROWAG / 2010 ADA Standards.
7. **PRIVATE LANE** (§319; Checklist §4.s). One private lane in an HOA tract 35'-11" to

Every dimension is computed from data/layout.json at run time and is DRAFT — the sealed RLS survey and the PE design govern.
 Lot designations read BLOCK–LOT. EG ± is EXISTING ground from the USGS 3DEP DEM, approximate; FFE is set on Sheet C-3.0. Boundary and adjoining parcels: Gwinnett County GIS parcel fabric.

- 46'-1" wide serves every lot; the tract is dimensioned at two stations. Typical section 1'-9" strip + 5'-0" walk + 2'-0" strip + 25'-0" asphalt + 2'-0" strip + 5'-0" walk + 1'-9" strip. Each lot has 50'-0" of frontage against the 30-ft minimum of §319. Labelled PRIVATE: "all components of private streets and alleys must meet minimum standards for public street" (§4.5). Pavement 2-in GDOT Type E or F on min. 4-in GAB; section on Sheet C-8.0. South-west walk from u = 530; travelled way 1754'-0". The 5-ft sidewalk and the 10-ft Arcadio Rd landscape strip appear in the Checklist only under the Highway 29 Overlay comments (§5.b, §5.g) and are therefore provided VOLUNTARILY — confirm applicability at the pre-application conference.
8. FIRE HYDRANTS AND WATER. 5 hydrants on a new 8-in DIP main in the lane tract, 3 on this sheet at the stations shown; spacing 360 / 410 / 355 / 376 ft against Gwinnett DWR Water and Sewer Standards (April 2016) §2.2.15(b), "350 feet to an absolute maximum of 450 feet, with "a fire hydrant near the end of each main". Each stands in a common tract where the lane widens, so IFC 2024 (GA) App. D103.1 (26 ft of width where a hydrant is on the access road) can be met. Existing hydrant at (u -45, v +41), 61 ft from the front corner — Sheet C-0. Fire flow 1,000 gpm / 1 hr (App. B Table B105.1(1)), 500 gpm with the voluntary NFPA 13D sprinklers. Main size, valving and the DWR flow test: Sheet C-4.0.
9. FIRE APPARATUS ACCESS. The lane is a 1754'-0" dead end; IFC 2024 (GA) App. D103.4 SPECIAL APPROVAL of a dead end over 750 ft is requested of the Gwinnett County Fire Marshal. Three 20'-0" x 60'-0" hammerheads at u = 540, 1110, 1690, no interval over 594 ft, and no circular cul-de-sac (Table 4.2 R-2 "A"). A SECOND ACCESS IS NOT REQUIRED; Ga. Comp. R. & Regs. 120-3-3-.04 replaces App. D107.1 and sets the trigger at MORE THAN 120 DWELLING UNITS, not the model code's 30; this development has 41. NFPA 13D sprinklers are offered VOLUNTARILY, not as required mitigation. No on-lane parking; 22'-0" is kept clear.
10. EXISTING SANITARY SEWER IN THE BUFFER EASEMENT. The existing 8-in Arcadio Road Townhomes outfall and its 20-ft easement run inside the south-west line from u = -42 to the existing manhole at (u 272, v -224), so they fall within the rear buffer easement of LOT A-1. The buffer stays undisturbed except for the existing sewer, which pre-dates it; Checklist §6.f allows sanitary sewer conveyance to encroach a buffer "as near perpendicular as possible, up to max 50' width", and this run is parallel — CONFIRM the reading at the pre-application conference. The 20-ft width is from the 2025 hydrology sheet, NOT a surveyed plat dimension; confirm width and holder by title examination. Inverts elsewhere in this set are unsurveyed DWR GIS attributes.
11. FRONT AMENITY TRACT AND ENTRANCE. The clubhouse, village green, two pickleball courts, guest and mail-kiosk parking, the monument entry sign, the 10-ft landscape strip and the 50-ft Arcadio Rd building setback line are shown for continuity and are drawn and dimensioned at 1" = 20' on Sheet C-2.3, which also carries the entrance geometry, the intersection sight distance and sight triangles, and the south-west curb return's encroachment into the 20-ft buffer — a buffer reduction the Letter of Intent requests expressly. No lot fronts Arcadio Rd and no lot has direct access to it,

2. **FINISHED FLOOR ELEVATIONS** (Checklist §4.g). FFE is NOT SET at the REZONING TABLE, "EG 3" in each lot is the EXISTING ground at the centre of the pad (NAVD88), interpolated from the USGS 3DEP 1-m DEM on a 100 x 50-ft grid — APPROXIMATE, for reference only, NOT a proposed elevation; on this sheet it ranges 933 to 949 ft. Finished floors, proposed contours, pad grading, walls and the lane profile are set by the PE on Sheets C-3.0 and C-5.0 after a topographic survey. Each dwelling is 1 story, ridge 17'-10" (Plan A) / 19'-4" (Plan B) above finished floor against the 40-ft Table 4.1 maximum.
13. **OPEN SPACE AND MAINTENANCE** (Checklist §4.o). Every tract other than a numbered lot is common open space or private street tract, conveyed to and maintained by the HOA; none is offered for public dedication. Common open space 141,089 SF = 3.24 ac = 33.8% of the GIS area / 34.3% of 9.44 deeded ac, of which 13,960 SF is built or paved; green-only 127,129 SF = 30.5%. The 41,000 SF of buffer easement on lots is reported separately and is NOT counted. Development Regulations §5.9 "Recreation Areas" applies only at 50 acres or more, so all of this open space is voluntary.
14. **UTILITIES NOT DRAWN HERE**. Storm drainage, sanitary sewer, gas, electric and telecommunications are on Sheets C-3.0 and C-4.0. PHASE 1 NEEDS NO SEWER EXTENSION; the existing 8-in Arcade Road Townhomes outfall crosses the property; the point of connection is the existing manhole at invert 927.13. Phase 2 is a roughly 178-ft OFF-SITE GRAVITY TIE to the Legends at Parkview 8-in main at invert 919.58. AN IN-TRACT PUMP STATION, PRIVATE FORCE MAIN, PRIVATE GRAVITY SEWER OR GRIN IS NOT AVAILABLE. Gwinnett DWR's Standard Policy for Private Developments (rev. 9/2018) allows private facilities "only ... for commercial properties under single ownership"; and WSR-24 §1.3.1(A) allows a county station only where gravity is "more than 5,000 feet down gradient" against an actual 178 ft. DWR capacity certification required; Georgia 811 locates (O.C.G.A. §25-9) precede field work.
15. **ADJOINING PROPERTY**. Every parcel adjoining this sheet is zoned R-1, City of Lilburn, in single-family use — King David Manor (plat §1/159) north-east, Legends at Parkview (plat 118/187) south-west, Nantucket at the north-west end. PINs, addresses, owners and zoning for all 31 adjoining parcels and the county right-of-way are labelled on Sheet C-0 and are not repeated here, so the lot dimensions stay legible.
16. **STATUS, SIGNS AND MAIL. DRAFT — NOT SEALED**. Concept information prepared by the owner for a rezoning application under Ord. 2023-603 §1003; not a survey, not a construction document, not a plat. SIGNS: the only sign proposed is one ground-mounted monument entry sign at the Arcade Rd entrance, face not over 32 SF and height not over 6'-0" above grade (VERIFY against the Lilburn sign regulations); NO WALL SIGNS are PROPOSED on any dwelling, the clubhouse or any accessory structure. ALL SIGNS SHALL BE PERMITTED SEPARATELY (§4.g). MAIL: cluster box units at the amenity tract; contact the Lilburn Post Office Growth Manager (§4.r).

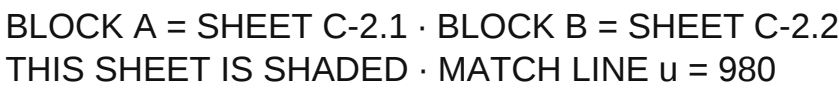

	Assemblage boundary — Gwinnett GIS, DRAFT (RLS survey governs)
	Proposed lot line (fee-simple lot)
	Building setback line — 15' front / 5' side / 20' rear
	20'-0" undisturbed buffer, recorded buffer easement
	Limit of buffer easement on a lot (§313(1))
	Proposed 1-story cottage — Plan A / Plan B body
	Attached 2-car garage (recessed 5'-0")
	Covered front porch, rear porch or patio
	Concrete driveway, 20'-0" x 26'-8"
	Asphalt pavement — lane, turnarounds, parking bays
	5'-0" concrete sidewalk
	Private lane tract line (HOA-owned and maintained)
	Lane centreline
	Common open space — pocket / terminus green (HOA)
	Front amenity tract (HOA)
	Village green
	Clubhouse and mail kiosk (CBU)
	Pickleball pad and court
	Guest / mail-kiosk parking stall, 9' x 18'
	Monument entry sign — see Sheet C-2.3
	Dry detention / water-quality basin, top of bank
	Basin tract (HOA)
	Proposed fire hydrant
	Proposed 8-in water main (see Sheet C-4.0)
	Existing 8-in sanitary sewer and manhole
	Existing 20' sanitary sewer easement (VERIFY)
	25' state (GA EPD) stream buffer
	50' undisturbed stream buffer (Lilburn)
	75' impervious setback
	50' Arcadio Rd building setback line (Table 4.1)
	10' landscape strip along the Arcadio Rd R/W
	Adjoining tax parcel — all zoned R-1, City of Lilburn
	Dimension line and witness line (US survey feet)
	Match line = block line = phase line, u = 980

Disclaimer: This is an AI-generated analysis for preliminary planning purposes. All findings must be verified by a licensed professional before use in design, permitting, or regulatory submissions.
Label: DRAFT / NOT SEALED — every item that must be sealed by a Georgia RLS, PE, architect or landscape architect is shown as a concept only. Statements of conformity read "appears consistent with".

4535 / 4537 / 4539 / 4541 Arcadio Rd SW, Lilburn, GA 30047 — Land Lot 123, 6th District, Gwinnett County — PINs R6123 033, 015, 014, 162 — 9.44 ac (deeded)

Lot-level enlargement of Sheet C-2.0 — Block A / Phase 1, u -40 to +1,000 · every lot, setback envelope, buffer easement, driveway, garage recess, lane tract and hydrants dimensioned

APPLICANT / OWNER Mohammed Awad 4541 Arcadio Rd SW, Lilburn GA 30047-3968 (parcels 033, 015); Mendez / Roblero de Leon (parcels 014, 162) — co-applicants, owner signatures required PREPARED FOR Pre-application conference, City of Lilburn Planning & Zoning (340 Main St) — rezoning application per Ord. 2023-603 §1003 (2026 Application Instructions)	STATUS DRAFT — NOT SEALED Concept lot layout for a rezoning application. Lot lines, setbacks, buffers, basins and easements are DRAFT. A sealed Georgia RLS boundary survey, PE civil design and a registered landscape architect's buffer and landscape plan are required and govern. Not a plat, not a survey. Generator: tools/sitebase.py + tools/enlargements.py	DATE 2026-09-03 SCALE Scale 1" = 30' (ARCH D 36 x 24 in) SOURCE SR 2240 GA West US-ft; NAVD88 DRAWN owner-prepared (AI-assisted) CHECKED RLS / PE — pending	SHEET C-2.1 MASTER CONCEPT PLAN — ENLARGEMENT, BLOCK A
--	---	---	--