



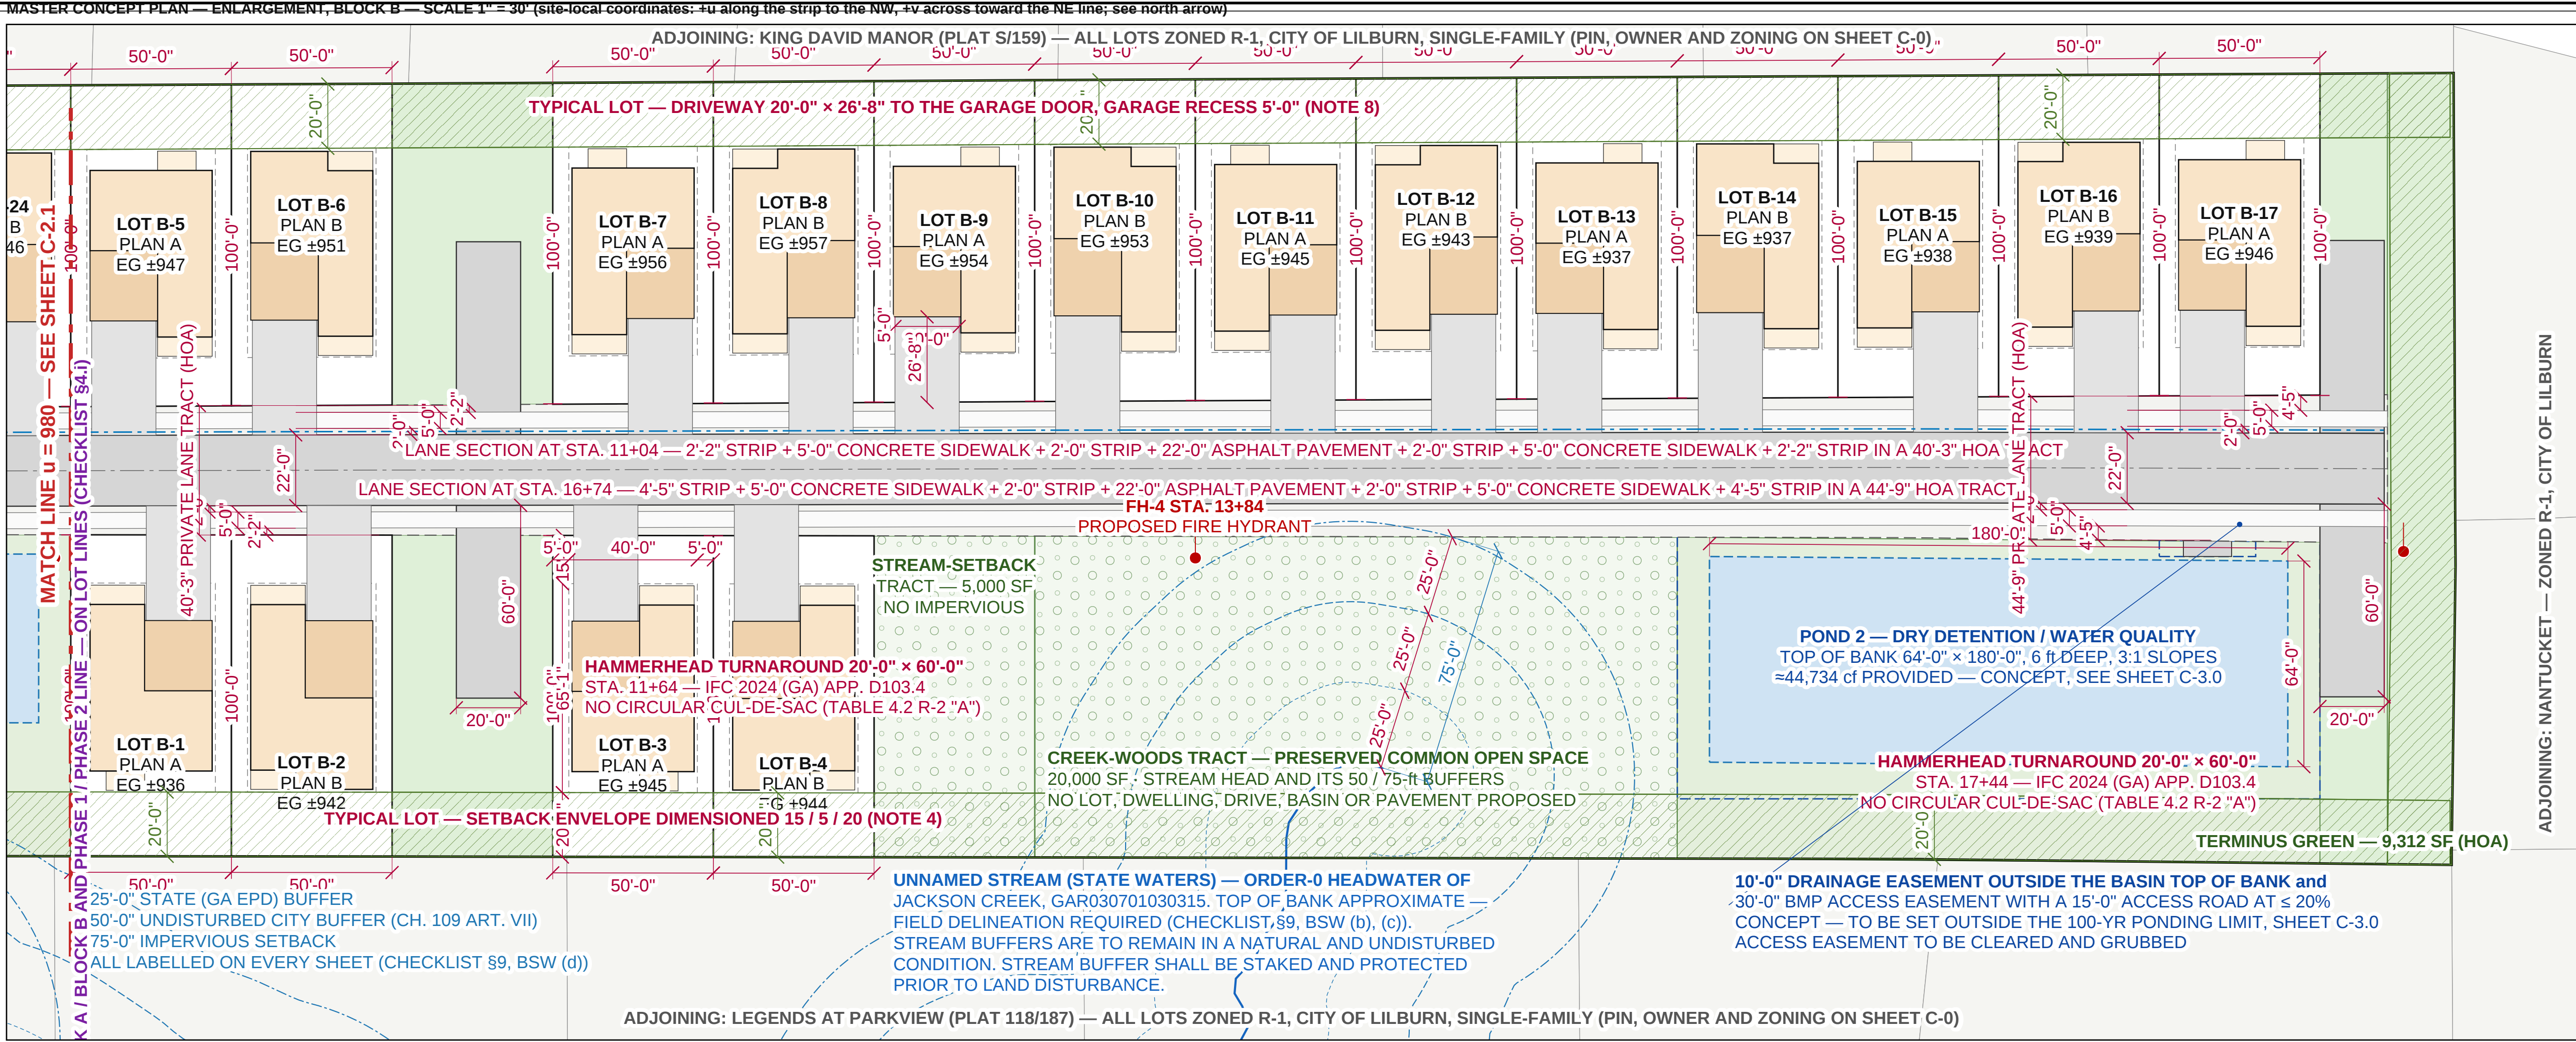


- LEGEND** — every symbol drawn appears below; no unused entry
- Assemblage boundary — Gwinnett GIS, DRAFT (RLS survey governs)
 - Proposed lot line (fee-simple lot)
 - Building setback line — 15' front / 5' side / 20' rear
 - 20'-0" undisturbed buffer, recorded buffer easement
 - Limit of buffer easement on a lot (§313(1))
 - Proposed 1-story cottage — Plan A / Plan B body
 - Attached 2-car garage (recessed 5'-0")
 - Covered front porch, rear porch or patio
 - Concrete driveway, 20'-0" x 26'-8"
 - Asphalt pavement — private lane and turnarounds
 - 5'-0" concrete sidewalk
 - Private lane tract line (HOA-owned and maintained)
 - Lane centreline
 - Common open space — pocket / terminus green (HOA)
 - Dry detention / water-quality basin, top of bank
 - Basin tract (HOA)
 - Creek-woods and stream-setback tracts — preserved
 - Drainage / BMP access easement (concept — Sheet C-3.0)
 - Proposed fire hydrant
 - Proposed 8-in water main (see Sheet C-4.0)
 - Stream — state waters, top of bank approximate
 - 25' state (GA EPD) stream buffer
 - 50' undisturbed stream buffer (Liburn)
 - 75' impervious setback
 - Adjoining tax parcel — all zoned R-1, City of Lilburn
 - Dimension line and witness line (US survey feet)
 - Match line = block line = phase line, u = 980

KEY PLAN — 1" ≈ 392' (SHEET C-2.0 COVERS THE WHOLE SITE AT 1" = 60')

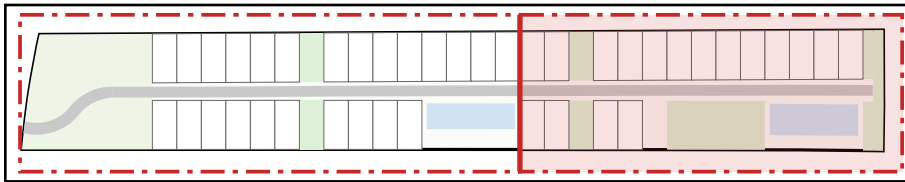

BLOCK A = SHEET C-2.1 · BLOCK B = SHEET C-2.2
THIS SHEET IS SHADED · MATCH LINE u = 980

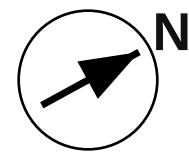

GRID NORTH (SR 2240 GA WEST)
= 28°43' ABOVE THE +u AXIS

DRAFT — NOT SEALED — CONCEPT PLAN FOR PRE-APPLICATION REVIEW

MATCH LINE u = 980 IS ALSO THE BLOCK LINE AND THE PHASE LINE — SEE THE KEY PLAN AND SHEET C-2.1

Every dimension is computed from data/layout.json at run time and is DRAFT — the sealed RLS survey and the PE design govern.

Lot designations read BLOCK–LOT. EG ± is EXISTING ground from the USGS 3DEP DEM, approximate; FFE is set on Sheet C-3.0. Boundary and adjoining parcels: Gwinnett County GIS parcel fabric.

GENERAL NOTES — SHEET C-2.2 (CONT.)

- and the lane is the preserved CREEK-WOODS TRACT. No stream-buffer variance is requested (§9, BSW (g)).
6. POND 2 — DRY DETENTION / WATER QUALITY. Concept basin, top of bank 65'-5" x 180'-0", 6-ft depth, 3:1 slopes, about 44,734 cf. The two basins provide 77,863 cf against 75,410 cf required at the Gwinnett County Stormwater Management Manual rate of 10,000 cf per disturbed acre on 7.54 disturbed acres (RRV zero at concept). WQv = 18,659 cf at 44.1% impervious. The top of bank stands 30.0 ft from the south-west line — 10.0 ft clear of the 20-ft buffer — and 98 ft from the nearest stream reach, outside the 75-ft setback. The 10-ft drainage easement and the 30-ft BMP access easement with its 15-ft road at ≤ 20% are CONCEPT, to be set outside the 100-year ponding limit by the PE on Sheet C-3.0 with forebay, outlet structure, spillway and the note ACCESS EASEMENT TO BE CLEARED AND GRUBBED. Ashlar (ARE) soils map gneiss bedrock at 22-40 in here: rock probes and an undercut allowance are required before the hydrology is trusted.
7. PERIMETER BUFFER (Table 4.1; §313(1); Checklist §4.j, §6.b). A 20'-0" UNDISTURBED buffer runs the entire south-west, north-east and north-west lines — every line abutting R-1 — and is dimensioned on the plan. Table 4.1 gives 0 ft for detached single-family in R-2 and 20 ft for "all other allowed dwelling types"; cottage homes are listed separately, so the plan is designed to 20 ft. The buffer lies in the rear 20 ft of each perimeter lot in a RECORDED BUFFER EASEMENT, on the reading that §313(1) lets a buffer supersede and coincide with the 20-ft rear yard. THIS SINGLE READING CARRIES THE LOT MODULE — CONFIRM IT AT THE PRE-APPLICATION CONFERENCE. Fallback (buffer in a separate tract, 50' x 82' lots, §1005 variance): Sheet C-2.4.
8. GARAGES AND DRIVEWAYS (Table 4.2 R-2 "A"; Checklist §4.p, §4.t, §7.i). Front-loaded garages are RECESSED 5'-0" BEHIND THE FRONT WALL as Table 4.2 requires; the porch projects a further 6'-0". The garage door stands 26'-8" from the front lot line, so the driveway holds two cars clear of the sidewalk. Driveways are 20'-0" x 26'-8", 4-in concrete on min. 4-in compacted GAB (asphalt alternate 2-in GDOT Type E or F on 4-in GAB, §7.i). 2 garage + 2 driveway spaces per dwelling = 164 on-lot against Table 8.1's 2 per unit; the sidewalk crosses every apron with curb ramps to PROWAG / 2010 ADA Standards.
9. PRIVATE LANE (§319; Checklist §4.s). One private lane in an HOA tract 35'-11" to 46'-1" wide serves every lot; the tract is dimensioned at two stations. Typical section 2'-2" strip + 5'-0" walk + 2'-0" strip + 22'-0" asphalt + 2'-0" strip + 5'-0" walk + 2'-2" strip. Each lot has 50'-0" of frontage against the 30-ft minimum of §319. Labelled PRIVATE: "all components of private streets and alleys must meet minimum standards for public street" (§4.s). Pavement 2-in GDOT

GENERAL NOTES — SHEET C-2.2 (CONT.)

- Type E or F on min. 4-in GAB; section on Sheet C-8.0. South-west walk from u = 530; travelled way 1754'-0". The 5-ft sidewalk and the 10-ft Arcado Rd landscape strip appear in the Checklist only under the Highway 29 Overlay comments (§5.b, §5.g) and are therefore provided VOLUNTARILY — confirm applicability at the pre-application conference.
10. FIRE HYDRANTS AND WATER. 5 hydrants on a new 8-in DIP main in the lane tract, 2 on this sheet at the stations shown; spacing 360 / 410 / 355 / 376 ft against Gwinnett DWR Water and Sewer Standards (April 2016) §2.2.15(b), "350 feet to an absolute maximum of 450 feet", with "a fire hydrant near the end of each main". Each stands in a common tract where the lane widens, so IFC 2024 (GA) App. D103.1 (26 ft of width where a hydrant is on the access road) can be met. Existing hydrant at (u -45, v +41), 61 ft from the front corner — Sheet C-0. Fire flow 1,000 gpm / 1 hr (App. B Table B105.1(1)), 500 gpm with the voluntary NFPA 13D sprinklers. Main size, valving and the DWR flow test: Sheet C-4.0.
11. FIRE APPARATUS ACCESS. The lane is a 1754'-0" dead end; IFC 2024 (GA) App. D103.4 SPECIAL APPROVAL of a dead end over 750 ft is requested of the Gwinnett County Fire Marshal. Three 20'-0" x 60'-0" hammerheads at u = 540, 1110, 1690, no interval over 594 ft, and no circular cul-de-sac (Table 4.2 R-2 "A"). A SECOND ACCESS IS NOT REQUIRED: Ga. Comp. R. & Regs. 120-3-3-.04 replaces App. D107.1 and sets the trigger at MORE THAN 120 DWELLING UNITS, not the model code's 30; this development has 41. NFPA 13D sprinklers are offered VOLUNTARILY, not as required mitigation. No on-lane parking; 22'-0" is kept clear.
12. FINISHED FLOOR ELEVATIONS (Checklist §4.g). FFE IS NOT SET AT THE REZONING STAGE. "EG ±" in each lot is the EXISTING ground at the centre of the pad (NAV/D88), interpolated from the USGS 3DEP 1-m DEM on a 100 x 50-ft grid — APPROXIMATE, for reference only, NOT a proposed elevation; on this sheet it ranges 935 to 956 ft. Finished floors, proposed contours, pad grading, walls and the lane profile are set by the PE on Sheets C-3.0 and C-5.0 after a topographic survey. Each dwelling is 1 story, ridge 17'-10" (Plan A) / 19'-4" (Plan B) above finished floor against the 40-ft Table 4.1 maximum.
13. OPEN SPACE AND MAINTENANCE (Checklist §4.o). Every tract other than a numbered lot is common open space or private street tract, conveyed to and maintained by the HOA; none is offered for public dedication. Common open space 141,089 SF = 3.24 ac = 33.8% of the GIS area / 34.3% of 9.44 deeded ac, of which 13,960 SF is built or paved; green-only 127,129 SF = 30.5%. The 41,000 SF of buffer easement on lots is reported separately and is NOT counted. Development Regulations §5.9 "Recreation Areas" applies only at 50 acres or more, so all of this open space is voluntary.

GENERAL NOTES — SHEET C-2.2 (CONT.)

14. UTILITIES NOT DRAWN HERE. Storm drainage, sanitary sewer, gas, electric and telecommunications are on Sheets C-3.0 and C-4.0. PHASE 1 NEEDS NO SEWER EXTENSION — the existing 8-in Arcado Road Townhomes outfall crosses the property; the point of connection is the existing manhole at invert 927.13. Phase 2 is a roughly 178-ft OFF-SITE GRAVITY TIE to the Legends at Parkview 8-in main at invert 919.58. AN IN-TRACT PUMP STATION, PRIVATE FORCE MAIN, PRIVATE GRAVITY SEWER OR GRINDER SYSTEM IS NOT AVAILABLE: Gwinnett DWR's Standard Policy for Private Developments (rev. 9/2018) allows private facilities "only ... for commercial properties under single ownership", and WSR-24 §13.3.1(A) allows a county station only where gravity is "more than 5,000 feet down gradient" against an actual 178 ft. DWR capacity certification required; Georgia 811 locates (O.C.G.A. §25-9) precede field work.
15. ADJOINING PROPERTY. Every parcel adjoining this sheet is zoned R-1, City of Lilburn, in single-family use — King David Manor (plat S/159) north-east, Legends at Parkview (plat 118/187) south-west, Nantucket at the north-west end. PINs, addresses, owners and zoning for all 31 adjoining parcels and the county right-of-way are labelled on Sheet C-0 and are not repeated here, so the lot dimensions stay legible.
16. STATUS, SIGNS AND MAIL. DRAFT — NOT SEALED. Concept information prepared by the owner for a rezoning application under Ord. 2023-603 §1003; not a survey, not a construction document, not a plat. SIGNS: the only sign proposed is one ground-mounted monument entry sign at the Arcado Rd entrance, face not over 32 SF and height not over 6'-0" above grade (VERIFY against the Lilburn sign regulations); NO WALL SIGNS ARE PROPOSED on any dwelling, the clubhouse or any accessory structure. ALL SIGNS SHALL BE PERMITTED SEPARATELY (§4.q). MAIL: cluster box units at the amenity tract; contact the Lilburn Post Office Growth Manager (§4.r).

Disclaimer: This is an AI-generated analysis for preliminary planning purposes. All findings must be verified by a licensed professional before use in design, permitting, or regulatory submissions.

Label: DRAFT / NOT SEALED — every item that must be sealed by a Georgia RLS, PE, architect or landscape architect is shown as a concept only. Statements of conformity read "appears consistent with".

THE COTTAGES AT ARCADE SPRINGS

MASTER CONCEPT PLAN — ENLARGEMENT, BLOCK B — Rezoning R-1 → R-2 (City of Lilburn, Georgia)

4535 / 4537 / 4539 / 4541 Arcado Rd SW, Lilburn, GA 30047 — Land Lot 123, 6th District, Gwinnett County — PINs R6123 033, 015, 014, 162 — 9.44 ac (deeded)

Lot-level enlargement of Sheet C-2.0 — Block B / Phase 2, u 960 to the north-west end - lots, creek-woods tract, stream buffers, Pond 2 and its easements, terminus green and hammerhead

APPLICANT / OWNER

Mohammed Awad

4541 Arcado Rd SW, Lilburn GA 30047-3968 (parcels 033, 015); Mendez / Roblero de Leon (parcels 014, 162) — co-applicants, owner signatures required

PREPARED FOR

Pre-application conference, City of Lilburn Planning & Zoning (340 Main St) — rezoning application per Ord. 2023-603 §1003 (2026 Application Instructions)

STATUS

DRAFT — NOT SEALED

Concept lot layout for a rezoning application. Lot lines, setbacks, buffers, basins and easements are DRAFT. A sealed Georgia RLS boundary survey, PE civil design and a registered landscape architect's buffer and landscape plan are required and govern. Not a plat, not a survey. Generator: tools/sitebase.py + tools/enlargements.py

DATE 2025-09-03

SCALE Scale 1" = 30' (ARCH D 36 x 24 in)

DATUM SR 2240 GA West US-ft; NAVD88

DRAWN owner-prepared (AI-assisted)

CHECKED RLS / PE — pending

SHEET

C-2.2

MASTER CONCEPT PLAN — ENLARGEMENT, BLOCK B