


ENTRY, FRONTAGE & AMENITY ENLARGEMENT — SCALE 1" = 20'

Site-local coordinates: +u along the strip to the NW, +v across toward the NE line (see north arrow). All dimensions in US survey feet, DRAFT — the sealed RLS boundary and right-of-way survey governs.

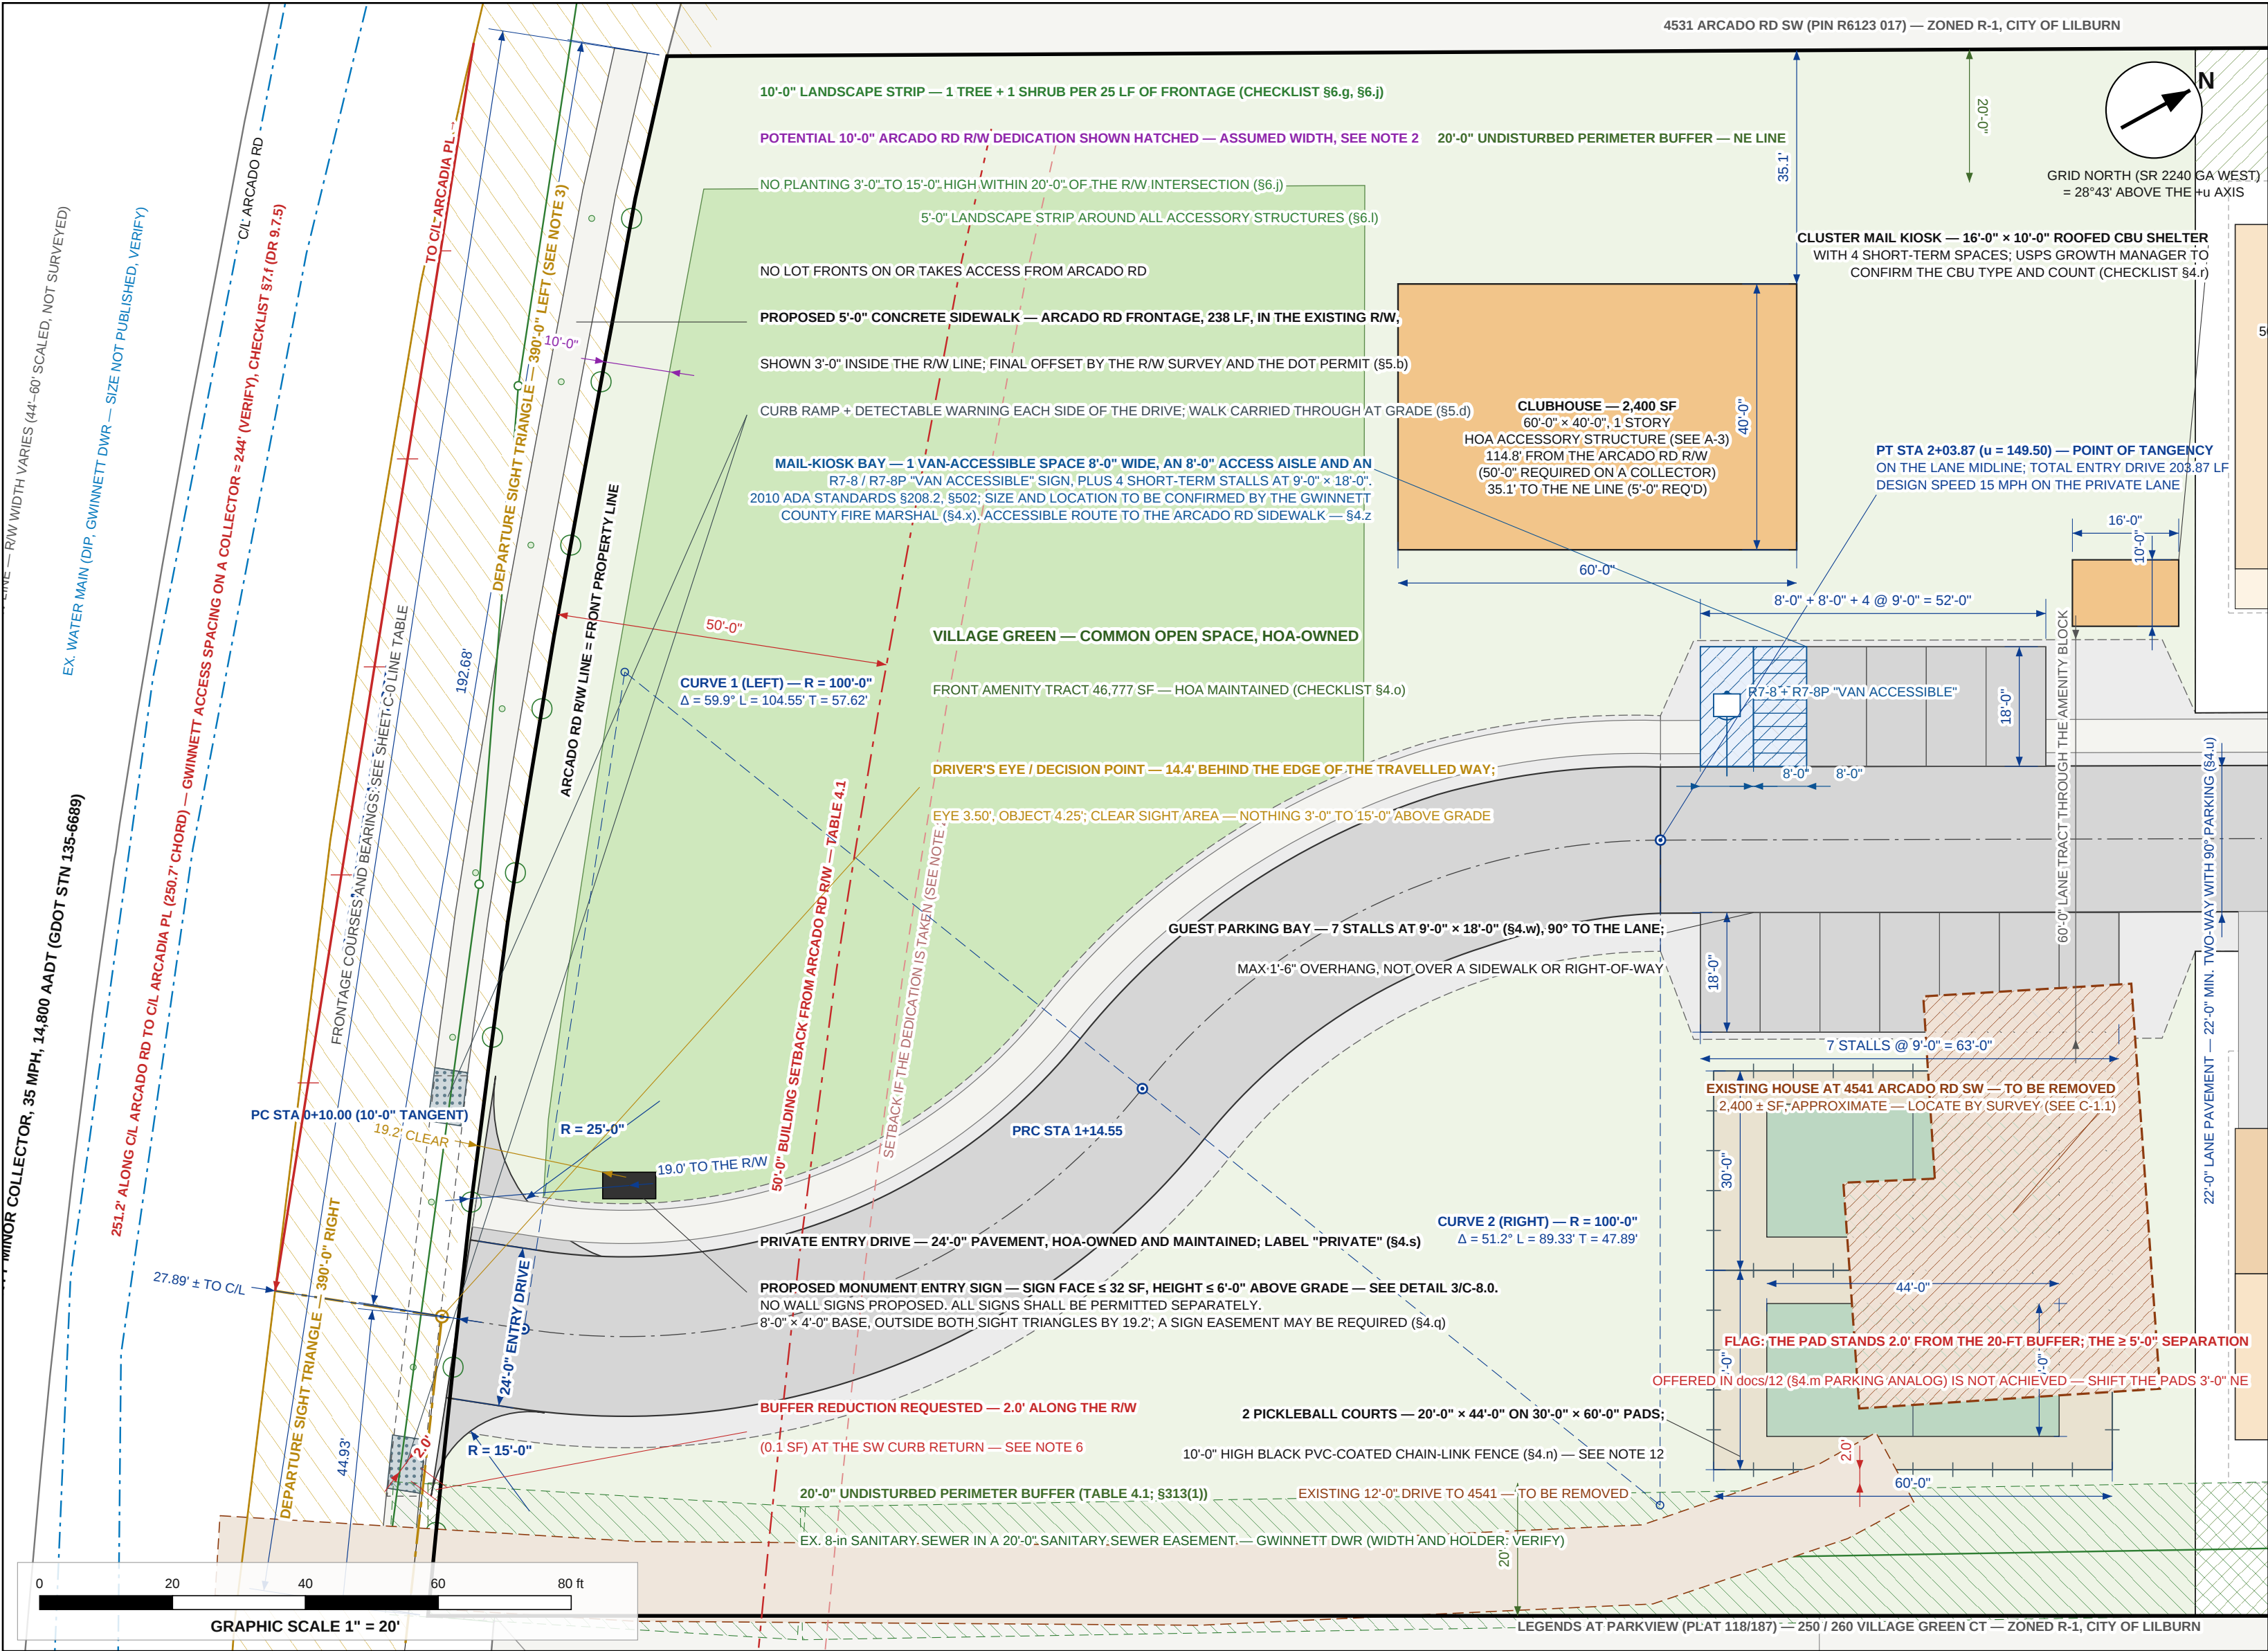

GENERAL NOTES — SHEET C-2.3

Ordinance citations: City of Lilburn Zoning Ordinance, Ord. 2023-603. "Checklist S" = City of Lilburn Site Development Plan Review Checklist. Every statement of conformity reads "appears consistent with".

- SCOPE AND STATUS.** This sheet enlarges the frontage, entrance and front amenity block of Sheet C-2.0 at 1" = 20'. Coordinates are site-local (u, v) US survey feet from the Gwinnett GIS parcel fabric and data/layout.json. DRAFT, NOT SEALED; a Georgia RLS boundary and R/W survey, a PE sight-distance certificate and PE civil design are required and govern. Nothing here certifies compliance.
- RIGHT-OF-WAY AND DEDICATION.** R/W WIDTH VARIES — 44-60 ft scaled between the two Gwinnett GIS R/W lines. 27.89 ft from the entrance to the mapped centreline; scaled, not surveyed. A Gwinnett minor collector section is wider, so a dedication is likely: the 10'-0" strip is SHOWN HATCHED AS AN ASSUMPTION ONLY. If taken, the 50-ft setback line moves inboard 10 ft (dashed), the landscape strip moves with it and the monument sign, at 9.0 ft from the new R/W, must be re-set. Establish the R/W by survey and the Gwinnett DOT permit.
- INTERSECTION SIGHT DISTANCE.** 390'-0" required each way at 35 mph (Gwinnett UDO §900.40.4 Table 900.2; AASHTO case B1). Triangles are

drawn from a decision point on the drive centreline 14.4 ft behind the edge of the travelled way, eye 3.50 ft, object 4.25 ft, to points 390 ft each way on the mapped centreline. Edge of travelled way ASSUMED 11'-0" from the CIL — verify. THE AVAILABLE SIGHT DISTANCE IS NOT CERTIFIED HERE: the certificate is blank (Checklist §7.i, DR 9.7.4). Vertical (crest) sight distance must be field-measured too.

- CLEAR SIGHT AREA.** Nothing between 3'-0" and 15'-0" above the roadway grade may stand in either triangle — no sign, wall, fence, berm, cabinet, parked vehicle or landscape planting (Checklist §6.j bars planting 3-15 ft high within 20 ft of a R/W intersection). The monument sign is clear by 19.2 ft at its nearest corner. Keeping the area clear is an HOA covenant obligation.
- ACCESS.** One full-movement private entrance; no lot fronts Arcadio Rd or takes a driveway from it. The entrance CIL is 251.2 ft from the CIL of Arcadia Pl along the Arcadio Rd centreline (250.7 ft chord) against a collector spacing of about 244 ft — VERIFY with

Gwinnett DOT. Arcadia Pl cannot be aligned with the drive: it meets Arcadio Rd 61 ft NE of the NE front corner. Checklist §7.f (DR 9.7.5) offsets: no other access is mapped within 400 ft.

- BUFFER REDUCTION REQUESTED.** With the SW curb return cut from R = 25'-0" to R = 15'-0", 2.0 ft of it measured along the R/W (0.1 SF of pavement) still lies inside the 20-ft perimeter buffer at the R/W corner. It is requested as a buffer reduction under Ord. 2023-603 §1003-4; Checklist §6.1 allows drives and utilities to encroach up to 50 ft of width and no further without a ZBA variance. The letter of intent and the voluntary conditions must match.
- PRIVATE STREET AND PAVING.** The entry drive and lane are private, HOA-owned and labelled "PRIVATE" per Checklist §4.s; all components must meet minimum public-street standards. Paving 4" GAB with 2" Type E or F asphalt minimum (§7.i), to be confirmed against the Lilburn Development Regulations and a Gwinnett Fire apparatus-load check. Materials and details on C-8.0 (§4.i).

- SIDEWALKS AND ACCESSIBLE ROUTE.** A 5'-0" concrete walk runs the full 238-LF frontage, shown 3'-0" inside the R/W line; the final offset (2'-0" min. behind back of curb, 6'-0" with street trees) is set by the R/W survey and the DOT permit. It is carried through the drive at grade with a curb ramp and detectable warning each side (§5.d). A 5'-0" walk on the NE side of the drive and lane links the clubhouse, kiosk and guest bay to the public walk (§4.2).
- LANDSCAPE.** 10'-0" landscape strip along the R/W: 1 tree + 1 shrub per 25 LF = 10 trees and 10 shrubs over 237.63 LF (§6.g, §6.j); parking lot planting 1 tree per 7 spaces with every space within 60 ft of a trunk (§6.k); 5'-0" landscape strip around every accessory structure (§6.i). The tree-protection, buffer and landscape plan must be sealed by a registered landscape architect, forester or arborist (§6.a) and is not part of this sheet.
- BUFFERS AND SETBACKS.** 20'-0" undisturbed perimeter buffer on the NE and SW lines (Table 4.1, R-2 abutting R-1, "all other allowed dwelling types"); §313(1) buffers supersede the minimum yards; none

on the Arcadio Rd frontage. Collector building setback 50'-0": the clubhouse, the nearest structure, is 114.8 ft from the R/W and 35.1 ft from the NE line against a 5'-0" accessory setback. Buffers in recorded easements (§4.i, §4.k, §4.l, §4.o).

- SIGNS.** One ground-mounted monument entry sign, face not exceeding 32 SF and height not exceeding 6'-0" above grade — see Detail 3/C-8.0 for the elevation and area computation. NO WALL SIGNS ARE PROPOSED on any dwelling, the clubhouse or any accessory structure. ALL SIGNS SHALL BE PERMITTED SEPARATELY (§4.q); a sign easement may be required. The sign regulations' area, height, setback and illumination limits to be confirmed at the pre-application.
- MAIL AND FENCING.** Cluster box units in a roofed 16'-0" x 10'-0" kiosk with four short-term spaces; the Lilburn Post Office Growth Manager confirms CBU type, count and the single street name used for house numbering (§4.r). The two pickleball pads are enclosed by a 10'-0" high black PVC-coated chain-link fence (§4.n); VERIFY the

residential fence-height limit for a 10-ft sport-court fence. No court lighting (voluntary condition 11).

- EXISTING CONDITIONS SHOWN.** The house and drive at 4541 Arcadio Rd SW are dashed and ARE TO BE REMOVED (C-1.1); the footprints are aerial-imagery approximations to be located by survey. The existing 8-in Gwinnett DWR gravity sewer and its 20-ft easement run inside the SW line through the buffer; the easement width and holder are from the 2025 hydrology sheet and are NOT surveyed. Georgia 811 locates (O.C.G.A. §25-9) are required before field work. Electric, gas, telecom and storm structures are NOT shown. The nearest existing fire hydrant is 61 ft from the front corner, NE of this sheet — see C-0.
- PERMITS STILL REQUIRED.** Gwinnett DOT driveway / encroachment permit and sight-distance certification; Gwinnett DWR sewer capacity certification; City of Lilburn Land Disturbance Permit; §1106 site and design review; a separate sign permit.

THE COTTAGES AT ARCADIO SPRINGS

ENTRY, FRONTAGE & AMENITY ENLARGEMENT — Rezoning R-1 → R-2 (City of Lilburn, Georgia)

4535 / 4537 / 4539 / 4541 Arcadio Rd SW, Lilburn, GA 30047
Land Lot 123, 6th District, Gwinnett County — PINs R6123 033, 015, 014, 162 — 9.44 ac (deeded)
Enlargement of Sheet C-2.0 at the Arcadio Rd frontage — right-of-way and dedication, sight triangles and ISD lines, curb returns and curve data, buffers, landscape strip, frontage sidewalk, clubhouse, courts, parking, sign, mail kiosk

APPLICANT / OWNER
Mohammed Awad
4541 Arcadio Rd SW, Lilburn GA 30047-3968 (parcels 033, 015); Mendez / Roblero de Leon (parcels 014, 162) — co-applicants, owner signatures required
PREPARED FOR
Pre-application conference, City of Lilburn Planning & Zoning (340 Main St) — rezoning per Ord. 2023-603 §1003

STATUS
DRAFT — NOT SEALED
Entry geometry, sight triangles and dimensions are DRAFT, from the Gwinnett GIS parcel fabric and data/layout.json. A sealed RLS boundary and right-of-way survey, a PE sight-distance certificate (blank at right) and a Gwinnett County DOT driveway permit are required and govern. Generator: tools/sitebase.py + tools/entry.py

DATE 2026-09-03
SCALE Scale 1" = 20' (ARCH C 24 x 18 in)
DATUM SR 2240 GA West US-ft; NAVD88
DRAWN owner-prepared (AI-assisted)
CHECKED RLS / PE — pending

SHEET
C-2.3
ENTRY, FRONTAGE & AMENITY ENLARGEMENT
ARCH C 24" x 18"


DRAFT — NOT SEALED — SEE SHEET C-2.0 FOR THE WHOLE SITE AND C-2.1 FOR THE LOTS

LEGEND — every symbol drawn on this sheet appears here

- Property line / Arcadio Rd R/W line
- Adjoining parcel — zoned R-1 (Lilburn)
- Opposite R/W line (R/W width varies)
- Existing road centreline
- Potential R/W dedication (10'-0" assumed)
- 10'-0" landscape strip + planting
- 20'-0" undisturbed perimeter buffer
- 50'-0" building setback from the R/W
- Setback line if the dedication is taken
- Proposed pavement (drive, lane, bays)
- Proposed 5'-0" concrete sidewalk
- Curb ramp + detectable warning
- HOA tract line (amenity / lane / drive)
- Front amenity tract — common open space
- Village green
- Clubhouse / mail kiosk (accessory)
- Pickleball pad 30'-0" x 40'-0"
- Court surface 20'-0" x 44'-0"
- 10'-0" black chain-link fence
- Parking stall 9'-0" x 18'-0"
- Van-accessible space + access aisle
- Sight triangle — clear sight area
- Sight line — 390' ISD leg
- Driver's eye / decision point
- Curve point — PC / PRC / PT
- Monument entry sign (face ≤ 32 SF)
- Proposed cottage, garage and porch
- Existing 8-in sanitary sewer + MH
- Existing 20'-0" sewer easement
- Existing water main (Gwinnett DWR)
- Existing building / drive — to be removed

SIGHT DISTANCE & ACCESS SPACING DIAGRAM

Both departure sight triangles at full length. Scale 1" = 200' — NOT the scale of the plan above.

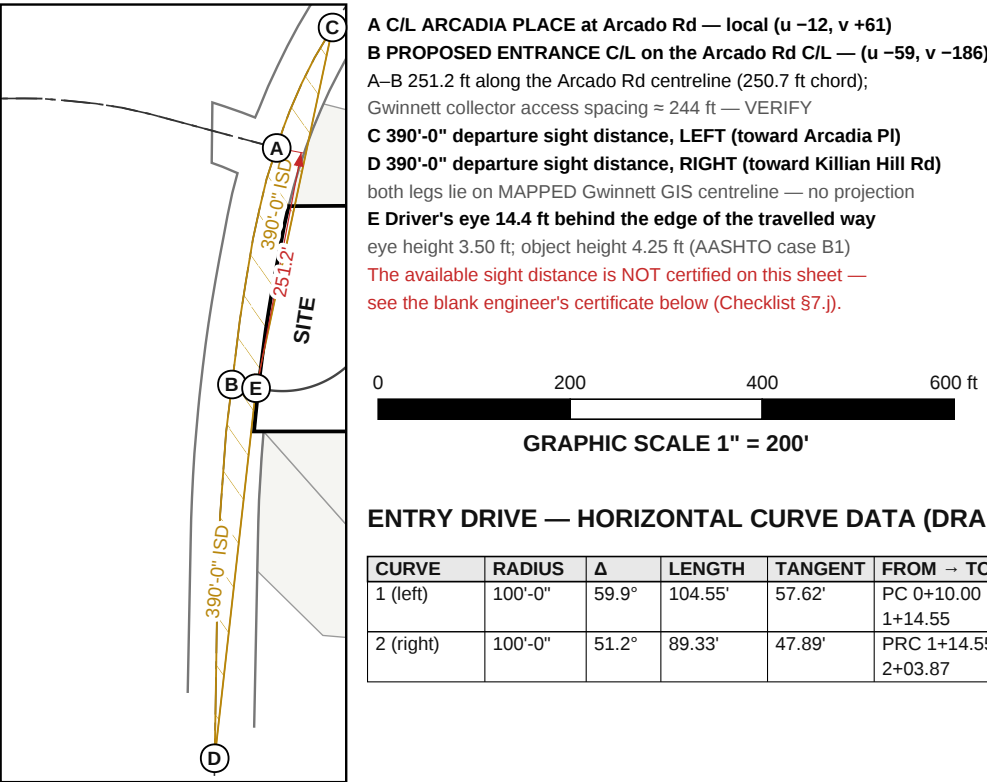

- A CIL ARCADIA PLACE** at Arcadio Rd — local (u -12, v +61)
- B PROPOSED ENTRANCE CIL** on the Arcadio Rd CIL — (u -59, v -186)
A-B 251.2 ft along the Arcadio Rd centreline (250.7 ft chord);
Gwinnett collector access spacing = 244 ft — VERIFY
- C 390'-0" departure sight distance, LEFT** (toward Arcadia Pl)
- D 390'-0" departure sight distance, RIGHT** (toward Killian Hill Rd)
both legs lie on MAPPED Gwinnett GIS centreline — no projection
- E Driver's eye 14.4 ft behind the edge of the travelled way**
eye height 3.50 ft; object height 4.25 ft (AASHTO case B1)
The available sight distance is NOT certified on this sheet — see the blank engineer's certificate below (Checklist §7.j).

0 200 400 600 ft
GRAPHIC SCALE 1" = 200'

ENTRY DRIVE — HORIZONTAL CURVE DATA (DRAFT)

CURVE	RADIUS	Δ	LENGTH	TANGENT	FROM — TO
1 (left)	100'-0"	59.9°	104.55'	57.62'	PC 0+10.00 → PRC 1+14.55
2 (right)	100'-0"	51.2°	89.33'	47.89'	PRC 1+14.55 → PT 2+03.87

ENGINEER'S CERTIFICATE — SIGHT DISTANCE (BLANK — TO BE COMPLETED AND SEALED)

City of Lilburn Site Development Plan Review Checklist §7.j; Gwinnett Dev. Regulations 9.7.4. To be completed, signed, dated and sealed across the seal by a Georgia registered professional engineer. NOT COMPLETED — this sheet makes no sight-distance claim.

I certify that I have field-measured the intersection sight distance available at the entrance shown on this sheet, from a driver's eye height of 3.50 ft located 14.4 ft behind the edge of the travelled way to an object height of 4.25 ft, and that the available sight distance is:
LEFT (toward Arcadia Pl) _____ ft RIGHT (toward Killian Hill Rd) _____ ft
REQUIRED _____ ft at _____ mph. Vertical (crest) sight distance: YES ___ NO ___
Clearing required in the R/W or the landscape strip: YES ___ NO ___
Signature _____ Printed _____ GA P.E. No. _____ Date _____

ENTRANCE AND ACCESS DATA (DRAFT — Checklist §4.p, §7.f, §7.j)

ITEM	VALUE / BASIS
Entrance on the R/W	u -31.43, v -190.00 — SW third of the frontage; 192.68' from the NE front corner, 44.93' from the SW corner, along the R/W
Entry drive	24'-0" pavement, private, two-way; 203.87 LF, R/W to the lane midline
Curb returns	NE R = 25'-0"; SW R = 15'-0", reduced from 25'-0" to clear the buffer
Access spacing	251.2' to the CIL of Arcadia Pl along the Arcadio Rd CIL (250.7' chord) against ≈ 244 ft — VERIFY (Checklist §7.i)
Sight distance	390'-0" required each way at 35 mph; drawn, NOT certified here (Checklist §7.j)
Left-turn lane	Not warranted below 75 lots (41 proposed) — VERIFY with Gwinnett DOT
Buffer reduction	2.0' along the R/W (0.1 SF) at the SW curb return — §1003-4, Checklist §6.f

PARKING AND ACCESSIBILITY (Checklist §4.v, §4.w, §4.x)

ITEM	REQUIRED / PROVIDED
Required, 41 dwellings	2 per dwelling unit, no maximum (Table 8.1) = 82 spaces
Provided on lot	164 — 2-car garage + 2-car driveway on every lot (Sheet C-2.1)
Guest bay	7 stalls at 9'-0" x 18'-0", 90° to the lane (Checklist §4.w)
Mail-kiosk bay	1 van-accessible 6'-0" stall + 8'-0" access aisle + R7-8 / R7-8P sign, and 4 stalls at 9'-0" x 18'-0"
Accessible required	1 of the 12 front-block spaces; 1 in 6 van-accessible (2010 ADA §208.2, §502.2) — 1 provided; size and location to be confirmed by the Gwinnett County Fire Marshal (Checklist §4.x)
Drive aisle	22'-0" minimum two-way with 90° parking (Checklist §4.u) — 22'-0" provided

Disclaimer: This is an AI-generated analysis for preliminary planning purposes. All findings must be verified by a licensed professional before use in design, permitting, or regulatory submissions.
DRAFT / NOT SEALED — every item that must be sealed by a Georgia RLS, PE, architect or landscape architect is shown as a concept only. Statements of conformity read "appears consistent with"; nothing on this sheet certifies compliance.