


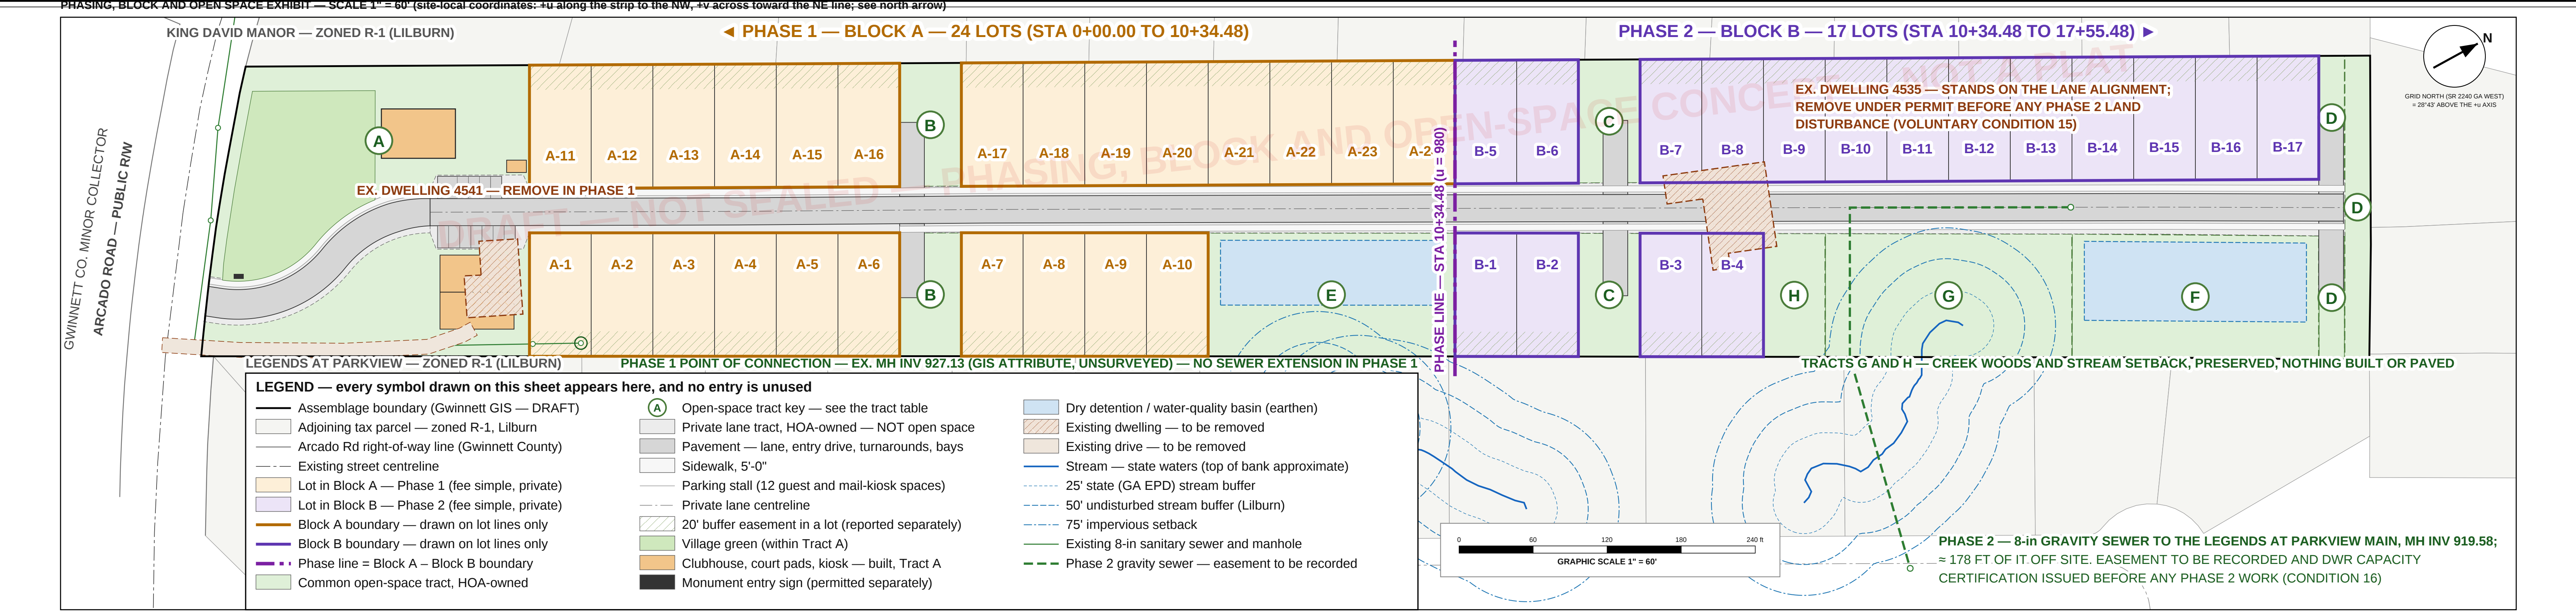

LOT SCHEDULE — BLOCK A (PHASE 1), 24 LOTS

LOT	C-2.0	SIDE	STATION u, ft	AREA SF	WIDTH	DEPTH	PLAN
A-1	1	SW	230 – 280	5,000	50'-0"	100'-0"	A
A-2	2	SW	280 – 330	5,000	50'-0"	100'-0"	B
A-3	3	SW	330 – 380	5,000	50'-0"	100'-0"	A
A-4	4	SW	380 – 430	5,000	50'-0"	100'-0"	B
A-5	5	SW	430 – 480	5,000	50'-0"	100'-0"	A
A-6	6	SW	480 – 530	5,000	50'-0"	100'-0"	B
A-7	7	SW	580 – 630	5,000	50'-0"	100'-0"	A
A-8	8	SW	630 – 680	5,000	50'-0"	100'-0"	B
A-9	9	SW	680 – 730	5,000	50'-0"	100'-0"	A
A-10	10	SW	730 – 780	5,000	50'-0"	100'-0"	B
A-11	15	NE	230 – 280	5,000	50'-0"	100'-0"	A
A-12	16	NE	280 – 330	5,000	50'-0"	100'-0"	B
A-13	17	NE	330 – 380	5,000	50'-0"	100'-0"	A
A-14	18	NE	380 – 430	5,000	50'-0"	100'-0"	B
A-15	19	NE	430 – 480	5,000	50'-0"	100'-0"	A
A-16	20	NE	480 – 530	5,000	50'-0"	100'-0"	B
A-17	21	NE	580 – 630	5,000	50'-0"	100'-0"	A
A-18	22	NE	630 – 680	5,000	50'-0"	100'-0"	B
A-19	23	NE	680 – 730	5,000	50'-0"	100'-0"	A
A-20	24	NE	730 – 780	5,000	50'-0"	100'-0"	B
A-21	25	NE	780 – 830	5,000	50'-0"	100'-0"	A
A-22	26	NE	830 – 880	5,000	50'-0"	100'-0"	B
A-23	27	NE	880 – 930	5,000	50'-0"	100'-0"	A
A-24	28	NE	930 – 980	5,000	50'-0"	100'-0"	B

LOT SCHEDULE — BLOCK B (PHASE 2), 17 LOTS

LOT	C-2.0	SIDE	STATION u, ft	AREA SF	WIDTH	DEPTH	PLAN
B-1	11	SW	980 – 1,030	5,000	50'-0"	100'-0"	A
B-2	12	SW	1,030 – 1,080	5,000	50'-0"	100'-0"	B
B-3	13	SW	1,130 – 1,180	5,000	50'-0"	100'-0"	A
B-4	14	SW	1,180 – 1,230	5,000	50'-0"	100'-0"	B
B-5	29	NE	980 – 1,030	5,000	50'-0"	100'-0"	A
B-6	30	NE	1,030 – 1,080	5,000	50'-0"	100'-0"	B
B-7	31	NE	1,130 – 1,180	5,000	50'-0"	100'-0"	A
B-8	32	NE	1,180 – 1,230	5,000	50'-0"	100'-0"	B
B-9	33	NE	1,230 – 1,280	5,000	50'-0"	100'-0"	A
B-10	34	NE	1,280 – 1,330	5,000	50'-0"	100'-0"	B
B-11	35	NE	1,330 – 1,380	5,000	50'-0"	100'-0"	A
B-12	36	NE	1,380 – 1,430	5,000	50'-0"	100'-0"	B
B-13	37	NE	1,430 – 1,480	5,000	50'-0"	100'-0"	A
B-14	38	NE	1,480 – 1,530	5,000	50'-0"	100'-0"	B
B-15	39	NE	1,530 – 1,580	5,000	50'-0"	100'-0"	A
B-16	40	NE	1,580 – 1,630	5,000	50'-0"	100'-0"	B
B-17	41	NE	1,630 – 1,680	5,000	50'-0"	100'-0"	A

GENERAL NOTES — PHASING, BLOCKS AND OPEN SPACE

- BLOCKS. Site Development Plan Review Checklist §4.i: "Subdivision — add number of lots/units ... Lot and Block Numbers if applicable. Phasing is not permitted unless platted in Blocks." Block A (Phase 1, 24 lots) and Block B (Phase 2, 17 lots) are platted as blocks, and every block boundary drawn here lies on a lot line or a tract line. Numbers A-1...A-24 and B-1...B-17 carry to the plat; column 2 of each schedule gives the C-2.0 lot number.
- PHASE LINE. STA 10+34.48 along the travelled way from the Arcado Rd right-of-way (204-ft entry drive plus lane) = local station u 980. NE side: the common lot line of Lots A-24 and B-5. SW side: the tract line between Tract E (Pond 1) and Lot B-1. Between them it crosses only the private lane tract. IT DIVIDES 0 LOTS.
- PHASE 1 IS DESIGNED TO STAND ALONE. Block A carries the entrance, the entire amenity block (Tract A), Pond 1 (Tract E), the first turnaround (Tract B) and 24 of the 41 lots, served by gravity to the existing 8-in county main already crossing the property (MH inv 927.13). No sewer extension, no off-site easement, no second access; complete whether or not Phase 2 is built.
- PHASE 2 CONDITION. No Phase 2 work and no land-disturbance permit until (a) the off-site sewer easement for the ≈ 178-ft gravity tie to the Legends at Parkview main (MH inv 919.58) is RECORDED and (b) Gwinnett County DWR has issued its SEWER CAPACITY CERTIFICATION (condition 16). Gravity only: no private pump station, force main, private gravity sewer, grinder pump or low-pressure system (Gwinnett DWR Standard Policy for Private Developments, rev. 9/2018; WSR-24 §1.3.1(A)). If either fails, Phase 2 is not built, and 4535 Arcado Rd — which stands on the lane alignment — comes down under permit first (condition 15).
- OPEN SPACE IS VOLUNTARY. Table 4.1 refers the R-2 open-space requirement to §5.9 of the Development Regulations; §5.9.1 "Recreation Areas" reaches detached subdivisions "having a gross area of 50 acres or more." At 9.44 ac it is not engaged: none of the 141,089 SF is required.
- BUFFER EASEMENT — REPORTED SEPARATELY. The rear 20 ft of each of the 41 lots is undisturbed buffer in a recorded easement inside the private lot (Ord. 2023-603 §313(1)); 41,000 SF. It is not a common tract, is not in the 141,089 SF total, and is in no percentage on this sheet.
- AREA BASIS. 417,174 SF = 9.577 ac GIS; 411,206 SF = 9.44 ac deeded; percentages given against both. Tract areas are the published residual — GIS area less lots less the lane and entry-drive tracts — so the eight sum exactly. Tract A is NET: its outline encloses ≈ 58,956 SF, of which = 12,164 SF is entry drive and lane tract.
- BUILT AND PAVED INSIDE THE OPEN SPACE. 13,960 SF of 141,089 SF; the balance, 127,129 SF (30.5% of the GIS area), is green. Turnaround legs are counted at the full 1,200 SF each although only ≈ 6,041 SF of the 7,200 SF really falls inside the greens, so the figure is conservative. The 12 guest and kiosk spaces (2,070 SF of bays) lie in the lane tract and are not counted at all.
- MAINTENANCE (§4.o). A mandatory HOA owns and maintains Tracts A–H, the lane tract and its sidewalks, both ponds, the buffers and buffer easements, the entry sign and the lighting, and provides yard maintenance to every lot (condition 10). NOTHING IS OFFERED FOR DEDICATION TO THE CITY; only the sanitary mains and their easements become public, to Gwinnett DWR.
- NOT SHOWN, AND SOURCES. Dwellings, driveways and setback envelopes — Sheets C-2.0/2.1/2.2; bearings and topography — C-1.0; grading — C-3.0; utilities — C-4.0/4.1. Only the sewer reaches on or adjoining the property are drawn. Every area, count and station here is read at run time from data/layout.json (2026-09-03) and data/plans.json.

PHASE DATA — 41 LOTS IN TWO BLOCKS, 4.34 DU/AC ON THE DEEDED 9.44 AC

PHASE 1 · BLOCK A · STA 0+00.00–10+34.48 · 24 lots · 237,293 SF (5.45 ac) · 4.41 du/ac
Tracts A, B, E = 76,777 SF · Pond 1, 33,129 cf · turnaround 1 · gravity to the on-site main
PHASE 2 · BLOCK B · STA 10+34.48–17+55.48 · 17 lots · 179,880 SF (4.13 ac) · 4.12 du/ac
Tracts C, D, F, G, H = 64,312 SF · Pond 2, 44,734 cf · turnarounds 2, 3 · ≈ 178 ft off-site sewer tie
Every lot 5,000 SF · 50 ft x 100 ft · 50 ft of frontage on the private lane (§319 requires 30 ft)
PLAN A = "The Springbrook", 1,406 SF conditioned · PLAN B = "The Laurel", 1,492 SF conditioned (data/plans.json)

COMMON OPEN-SPACE TRACT TABLE — 141,089 SF = 3.239 AC = 33.8% OF THE 417,174-SF GIS AREA / 34.3% OF THE DEEDED 9.44 AC

TR.	NAME AND LOCATION	AREA SF	% GIS	% 9.44 AC	PH/BLK	WHAT THE TRACT CONTAINS — BUILT AND PAVED AREA STATED	MAINT.
A	Front amenity tract, Arcado Rd frontage to u 230	46,777	11.21%	11.38%	1 / A	Clubhouse 2,400 SF + two court pads 3,600 SF + mail kiosk 160 SF + walks 600 SF = 6,760 SF BUILT OR PAVED, 14.5% of the tract. Also the village green, landscape strip and monument sign. The 12 guest and kiosk spaces (2,070 SF of bays) are NOT in it — note 8.	HOA
B	Pocket green, both sides, u 530–580	10,000	2.40%	2.43%	1 / A	Lawn and plantings. Hammerhead turnaround 1 — 2,400 SF of pavement in two legs.	HOA
C	Pocket green, both sides, u 1,080–1,130	10,000	2.40%	2.43%	2 / B	Lawn and plantings. Hammerhead turnaround 2 — 2,400 SF of pavement in two legs.	HOA
D	Terminus green + rear buffer, u 1,680–1,722	9,312	2.23%	2.26%	2 / B	Lawn; rear 20-ft buffer in common ownership. Hammerhead turnaround 3 — 2,400 SF of pavement in two legs.	HOA
E	Pond 1 tract, SW side, u 780–980	20,000	4.79%	4.86%	1 / A	Dry detention / water-quality basin, 9,450 SF at top of bank — earthen, NOT impervious. Buffer, drainage and BMP access easements inside the tract.	HOA
F	Pond 2 tract, SW side, u 1,480–1,680	20,000	4.79%	4.86%	2 / B	Dry detention / water-quality basin, 11,520 SF at top of bank — earthen, NOT impervious. Buffer, drainage and BMP access easements inside the tract.	HOA
G	Creek woods, SW side, u 1,280–1,480	20,000	4.79%	4.86%	2 / B	Stream head, 50-ft undisturbed buffer and 75-ft impervious setback, preserved. NOTHING BUILT OR PAVED.	HOA
H	Stream-setback tract, SW, u 1,230–1,280	5,000	1.20%	1.22%	2 / B	The one 50 x 100-ft lot slot that fails the 75-ft screen, left unlotted. NOTHING BUILT OR PAVED.	HOA
TOTAL — EIGHT TRACTS		141,089	33.8%	34.3%	BOTH	Of which 13,960 SF is built or paved (note 8); 127,129 SF, 30.5% of the GIS area, is green. NO open space is required here — note 5.	HOA

TRACT A HOLDS 6,760 SF OF BUILT AND PAVED AREA — 14.5% OF THE TRACT — AND ITS 46,777 SF IS NET OF THE ≈ 12,164 SF OF ENTRY DRIVE AND LANE TRACT CROSSING IT; THE 12 GUEST AND MAIL-KIOSK PARKING SPACES (2,070 SF OF BAYS) ARE NOT IN IT — THEY LIE IN THE PRIVATE LANE TRACT. SEE NOTE 8.

OTHER COMMON PROPERTY AND EASEMENTS — MAINTENANCE RESPONSIBILITY (CHECKLIST §4.o). NONE OF IT IS COUNTED AS COMMON OPEN SPACE

ITEM	AREA / DIMENSION	PHASE	OWNERSHIP	MAINTENANCE — HOA OR PUBLIC
Private lane tract, including the entry drive	71,085 SF	1 and 2	HOA in fee	HOA — pavement, sidewalks, curb, drainage, lighting and street trees. Private street (§4.s), built to public-street standards.
20-ft buffer easement on the rear of all 41 lots	41,000 SF	1 and 2	Lot owner in fee, subject to a recorded buffer easement (§313(1))	HOA maintains and enforces it; the owner may not clear, grade, fence or build in it.
Existing 20-ft sanitary sewer easement (Arcado Rd Townhomes outfall)	20' wide, u –42 to 272; width to be confirmed from the recorded plat	existing	Gwinnett County (DWR)	PUBLIC — DWR maintains the main; HOA mows the surface.
Phase 1 sanitary sewer easement, on site, to MH inv 927.13	20' wide, ≈ 814 ft; area by survey	1	To be dedicated to Gwinnett County (DWR)	PUBLIC — DWR maintains the main after acceptance; HOA the surface.
Phase 2 sanitary sewer easement, off site, to the Legends at Parkview main (MH inv 919.58)	20' wide, ≈ 178 ft of it OFF SITE; to be acquired	2	To be dedicated to Gwinnett County (DWR)	PUBLIC — DWR maintains the main. MUST BE RECORDED BEFORE ANY PHASE 2 WORK (condition 16).
Drainage and 30-ft BMP access easements at each pond	Within Tracts E and F; Sheet C-3.0	1 and 2	HOA in fee	HOA under a recorded Storm Water BMP Maintenance Agreement with the City (§9.g.3).
Arcado Road right-of-way	R/W width varies — Sheet C-1.0	existing	Gwinnett County	PUBLIC — Gwinnett County DOT. Nothing here is offered for dedication to the City.

PHASE 1 STANDS ALONE. PHASE 2 SHALL NOT COMMENCE UNTIL THE OFF-SITE SANITARY SEWER EASEMENT IS RECORDED AND GWINNETT COUNTY DWR HAS ISSUED ITS SEWER CAPACITY CERTIFICATION (LETTER OF INTENT, VOLUNTARY CONDITIONS 15 AND 16 — SEE NOTES 3 AND 4).

Disclaimer: This is an AI-generated analysis for preliminary planning purposes. All findings must be verified by a licensed professional before use in design, permitting, or regulatory submissions.

Label: DRAFT / NOT SEALED — every item that must be sealed by a Georgia RLS, PE, architect or landscape architect is shown as a concept only. Statements of conformity read "appears consistent with".

THE COTTAGES AT ARCADE SPRINGS

PHASING, BLOCK AND OPEN SPACE EXHIBIT — Rezoning R-1 → R-2 (City of Lilburn, Georgia)

4535 / 4537 / 4539 / 4541 Arcado Rd SW, Lilburn, GA 30047 — Land Lot 123, 6th District, Gwinnett County — PINs R6123 033, 015, 014, 162 — 9.44 ac (deeded)

Blocks, phases, common open-space tracts, easements and maintenance responsibility — Site Development Plan Review Checklist §4.i and §4.o; Ord. 2023-603 §313(1)

APPLICANT / OWNER

Mohammed Awad

4541 Arcado Rd SW, Lilburn GA 30047-3968 (parcels 033, 015); Mendez / Roblero de Leon (parcels 014, 162) — co-applicants, owner signatures required

PREPARED FOR

Pre-application conference, City of Lilburn Planning & Zoning (340 Main St) — rezoning application per Ord. 2023-603 §1003 (2026 Application Instructions)

STATUS

DRAFT — NOT SEALED

Phasing, block and open-space CONCEPT compiled from public records for pre-application review. NOT A PLAT. Block and lot plating, tract and easement descriptions and every area shown are to be prepared and sealed by a Georgia RLS; utilities and stormwater by a Georgia PE. Generator: tools/sitebase.py + tools/phasing.py

DATE

2025-09-03

SCALE

Scale 1" = 60' (ARCH D 36 x 24 in)

DATUM

SR 2240 GA West US-ft; NAVD88

DRAWN

owner-prepared (AI-assisted)

CHECKED

RLS / PE — pending

SHEET

C-6.0

PHASING, BLOCK AND OPEN SPACE EXHIBIT